


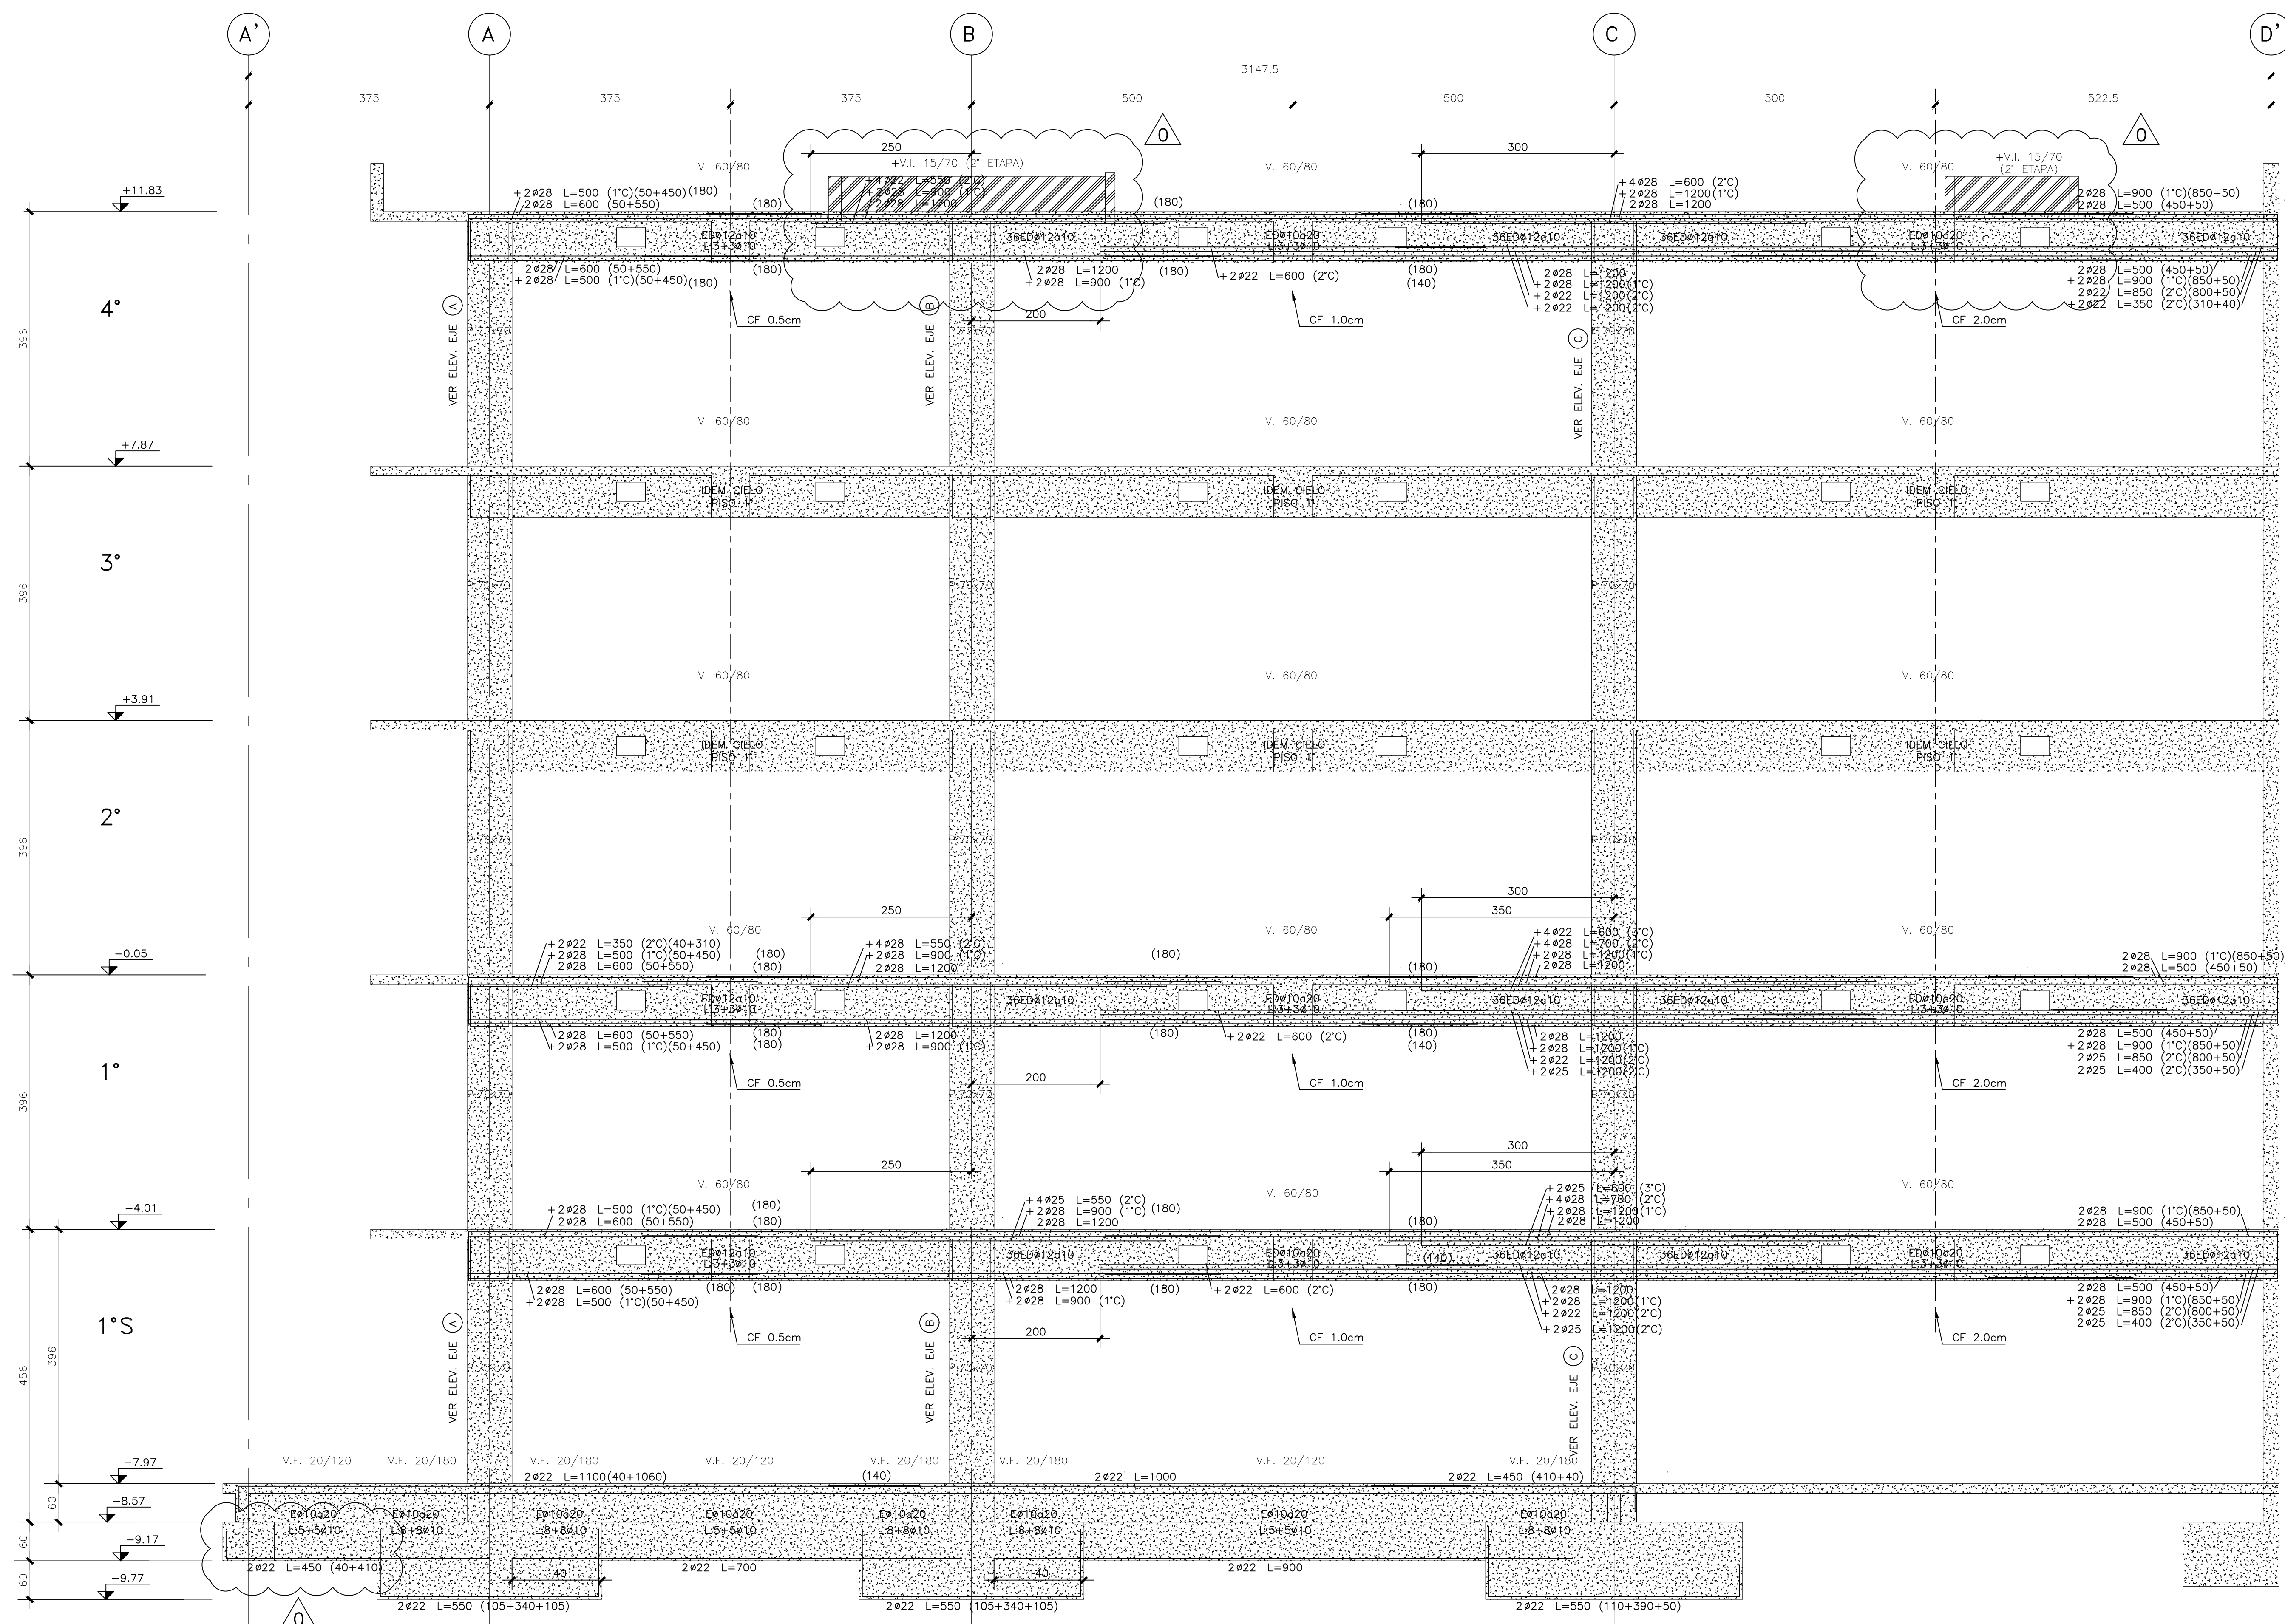

ELEVACION EJE 2
ESCALA 1:50

NOTA 1:
LOS ESTRIBOS DE COLUMNAS
DEBERAN SER CONTINUOS EN
TODA LA ALTURA, ES DECIR PASAR
POR EL NUDO VIGA-COLUMNA.

NOTA 2:
VER REFUERZOS TIPOS DE
PASADA EN VIGAS EN PLANO
N° 002.