



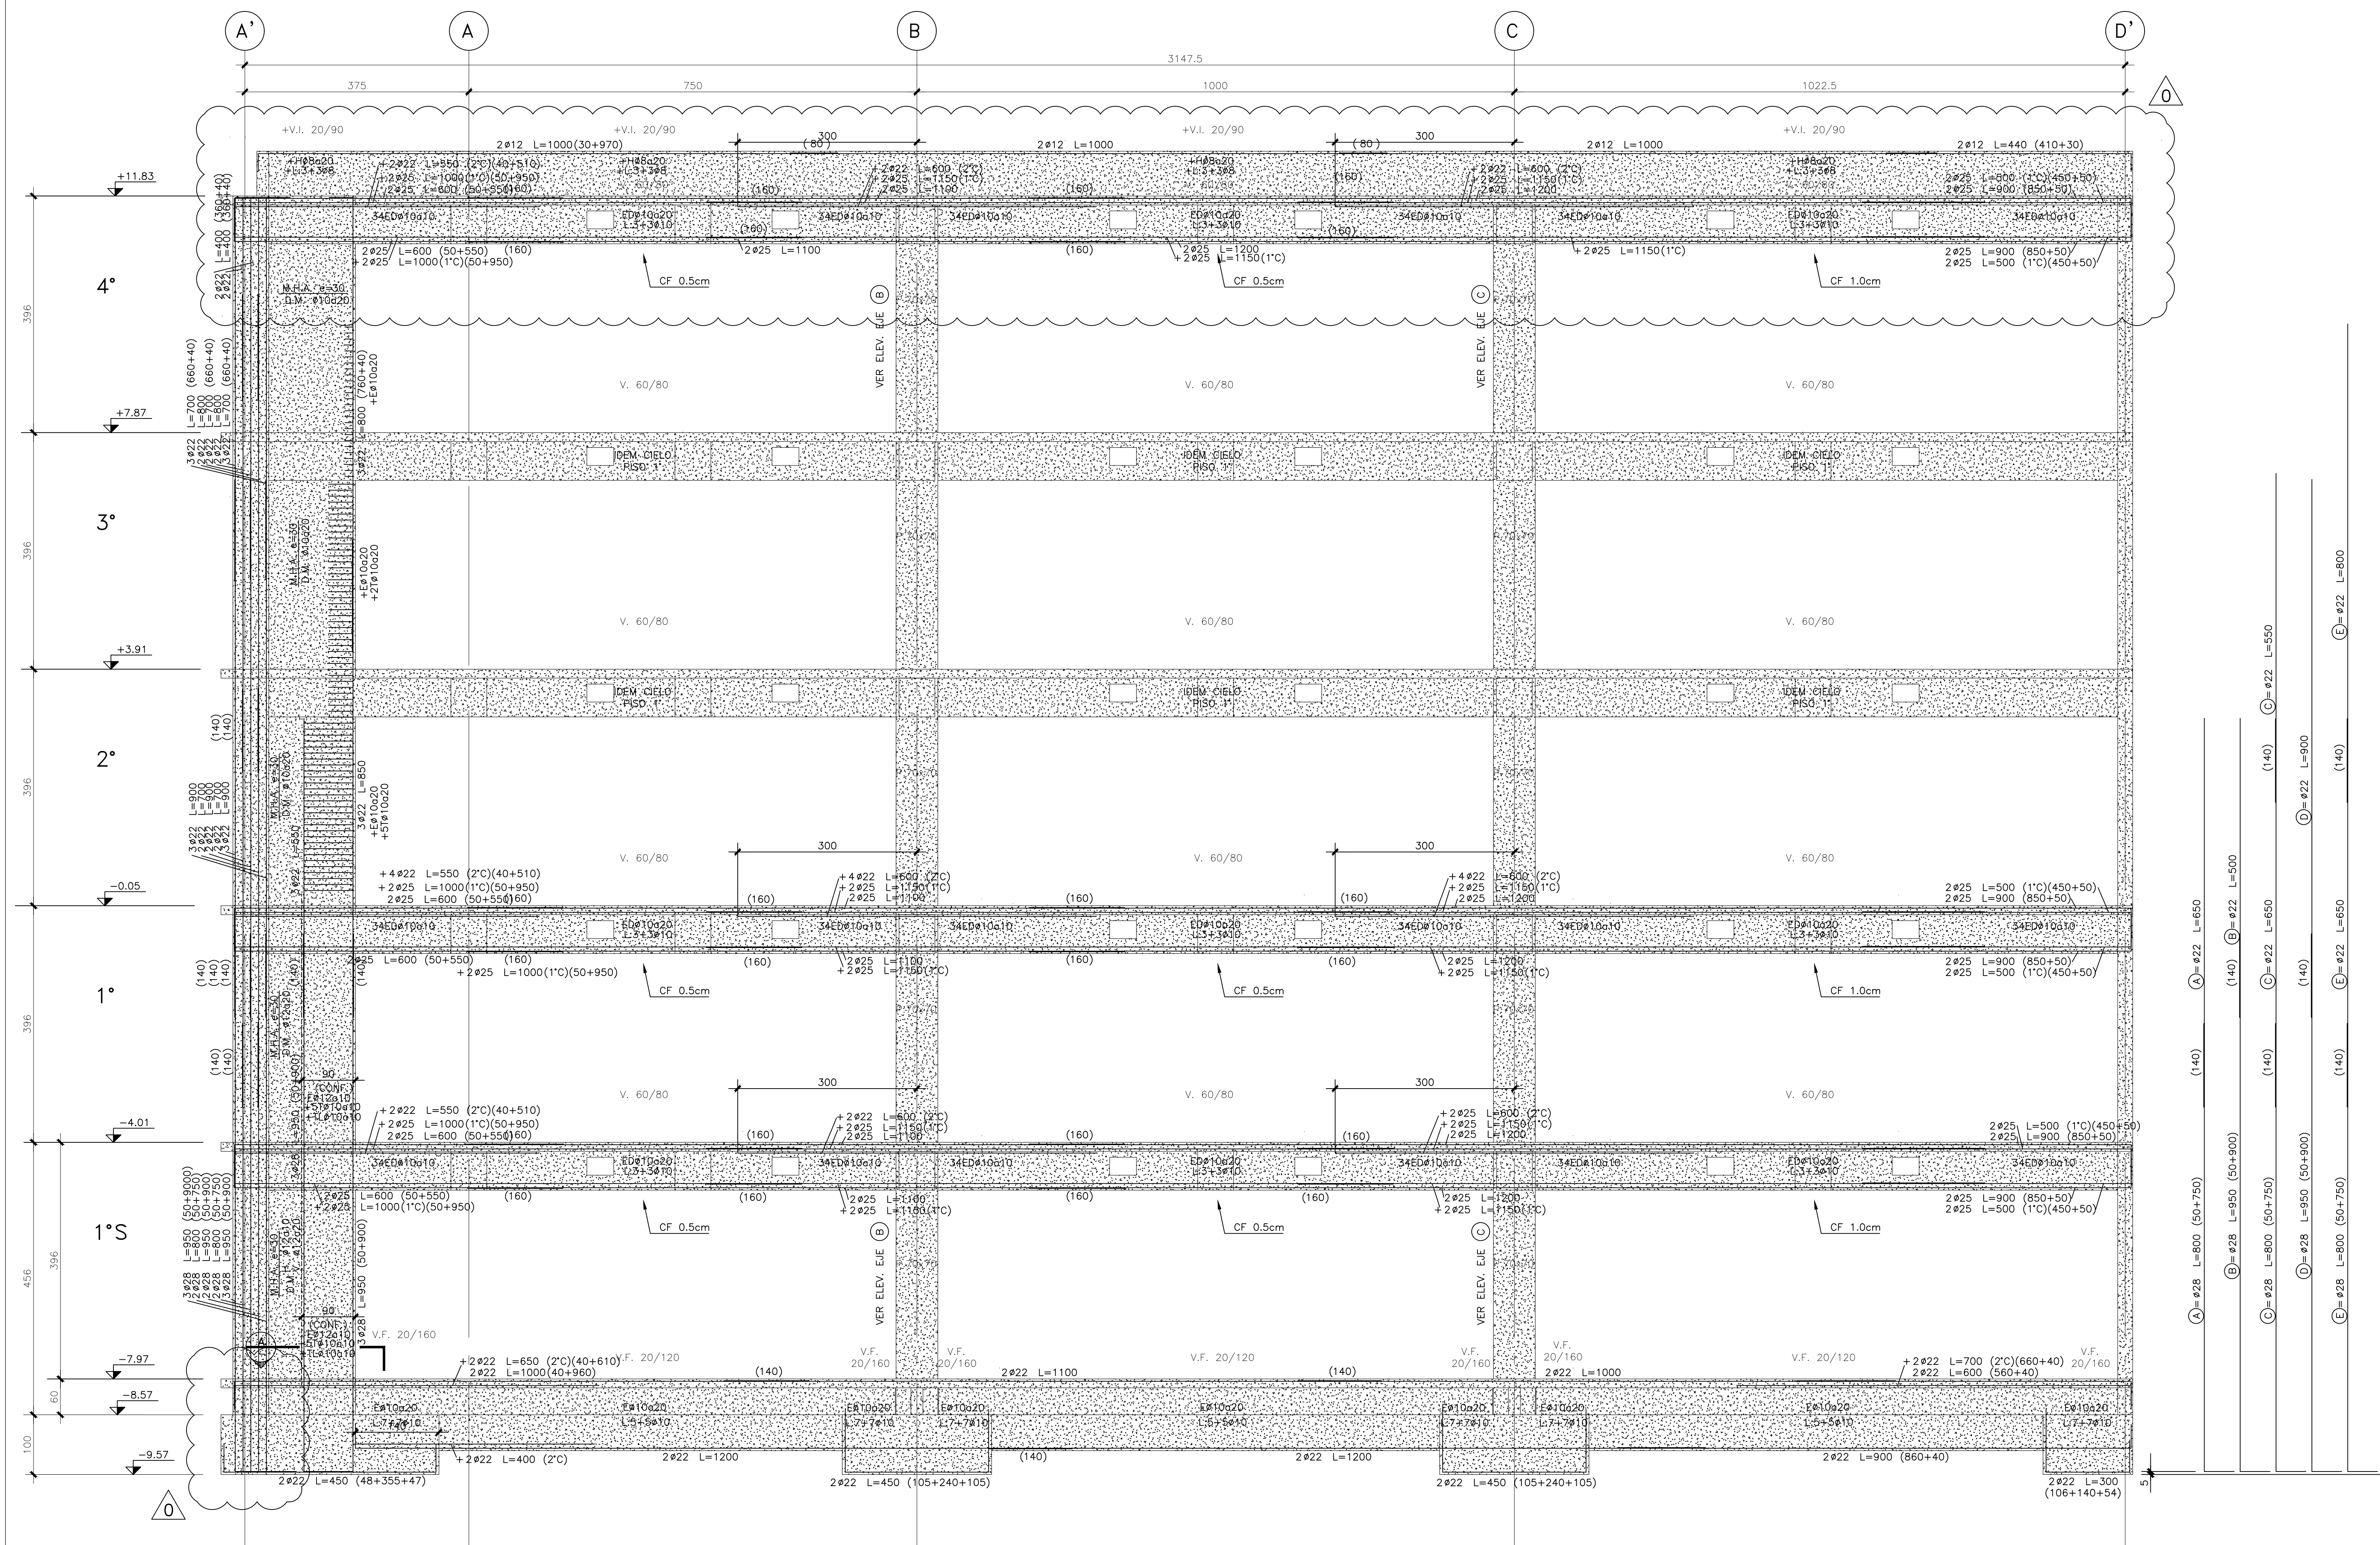


ELEVACION EJE 3  
ESCALA 1:50

NOTA 1:  
LOS ESTRIBOS DE COLUMNAS  
DEBERAN SER CONTINUOS EN  
TODA LA ALTURA, ES DECIR PASAR  
POR EL NUDO VIGA-COLUMNA.

NOTA 2:  
VER REFUERZOS TIPOS DE  
PASADA EN VIGAS EN PLANO  
N° 002.

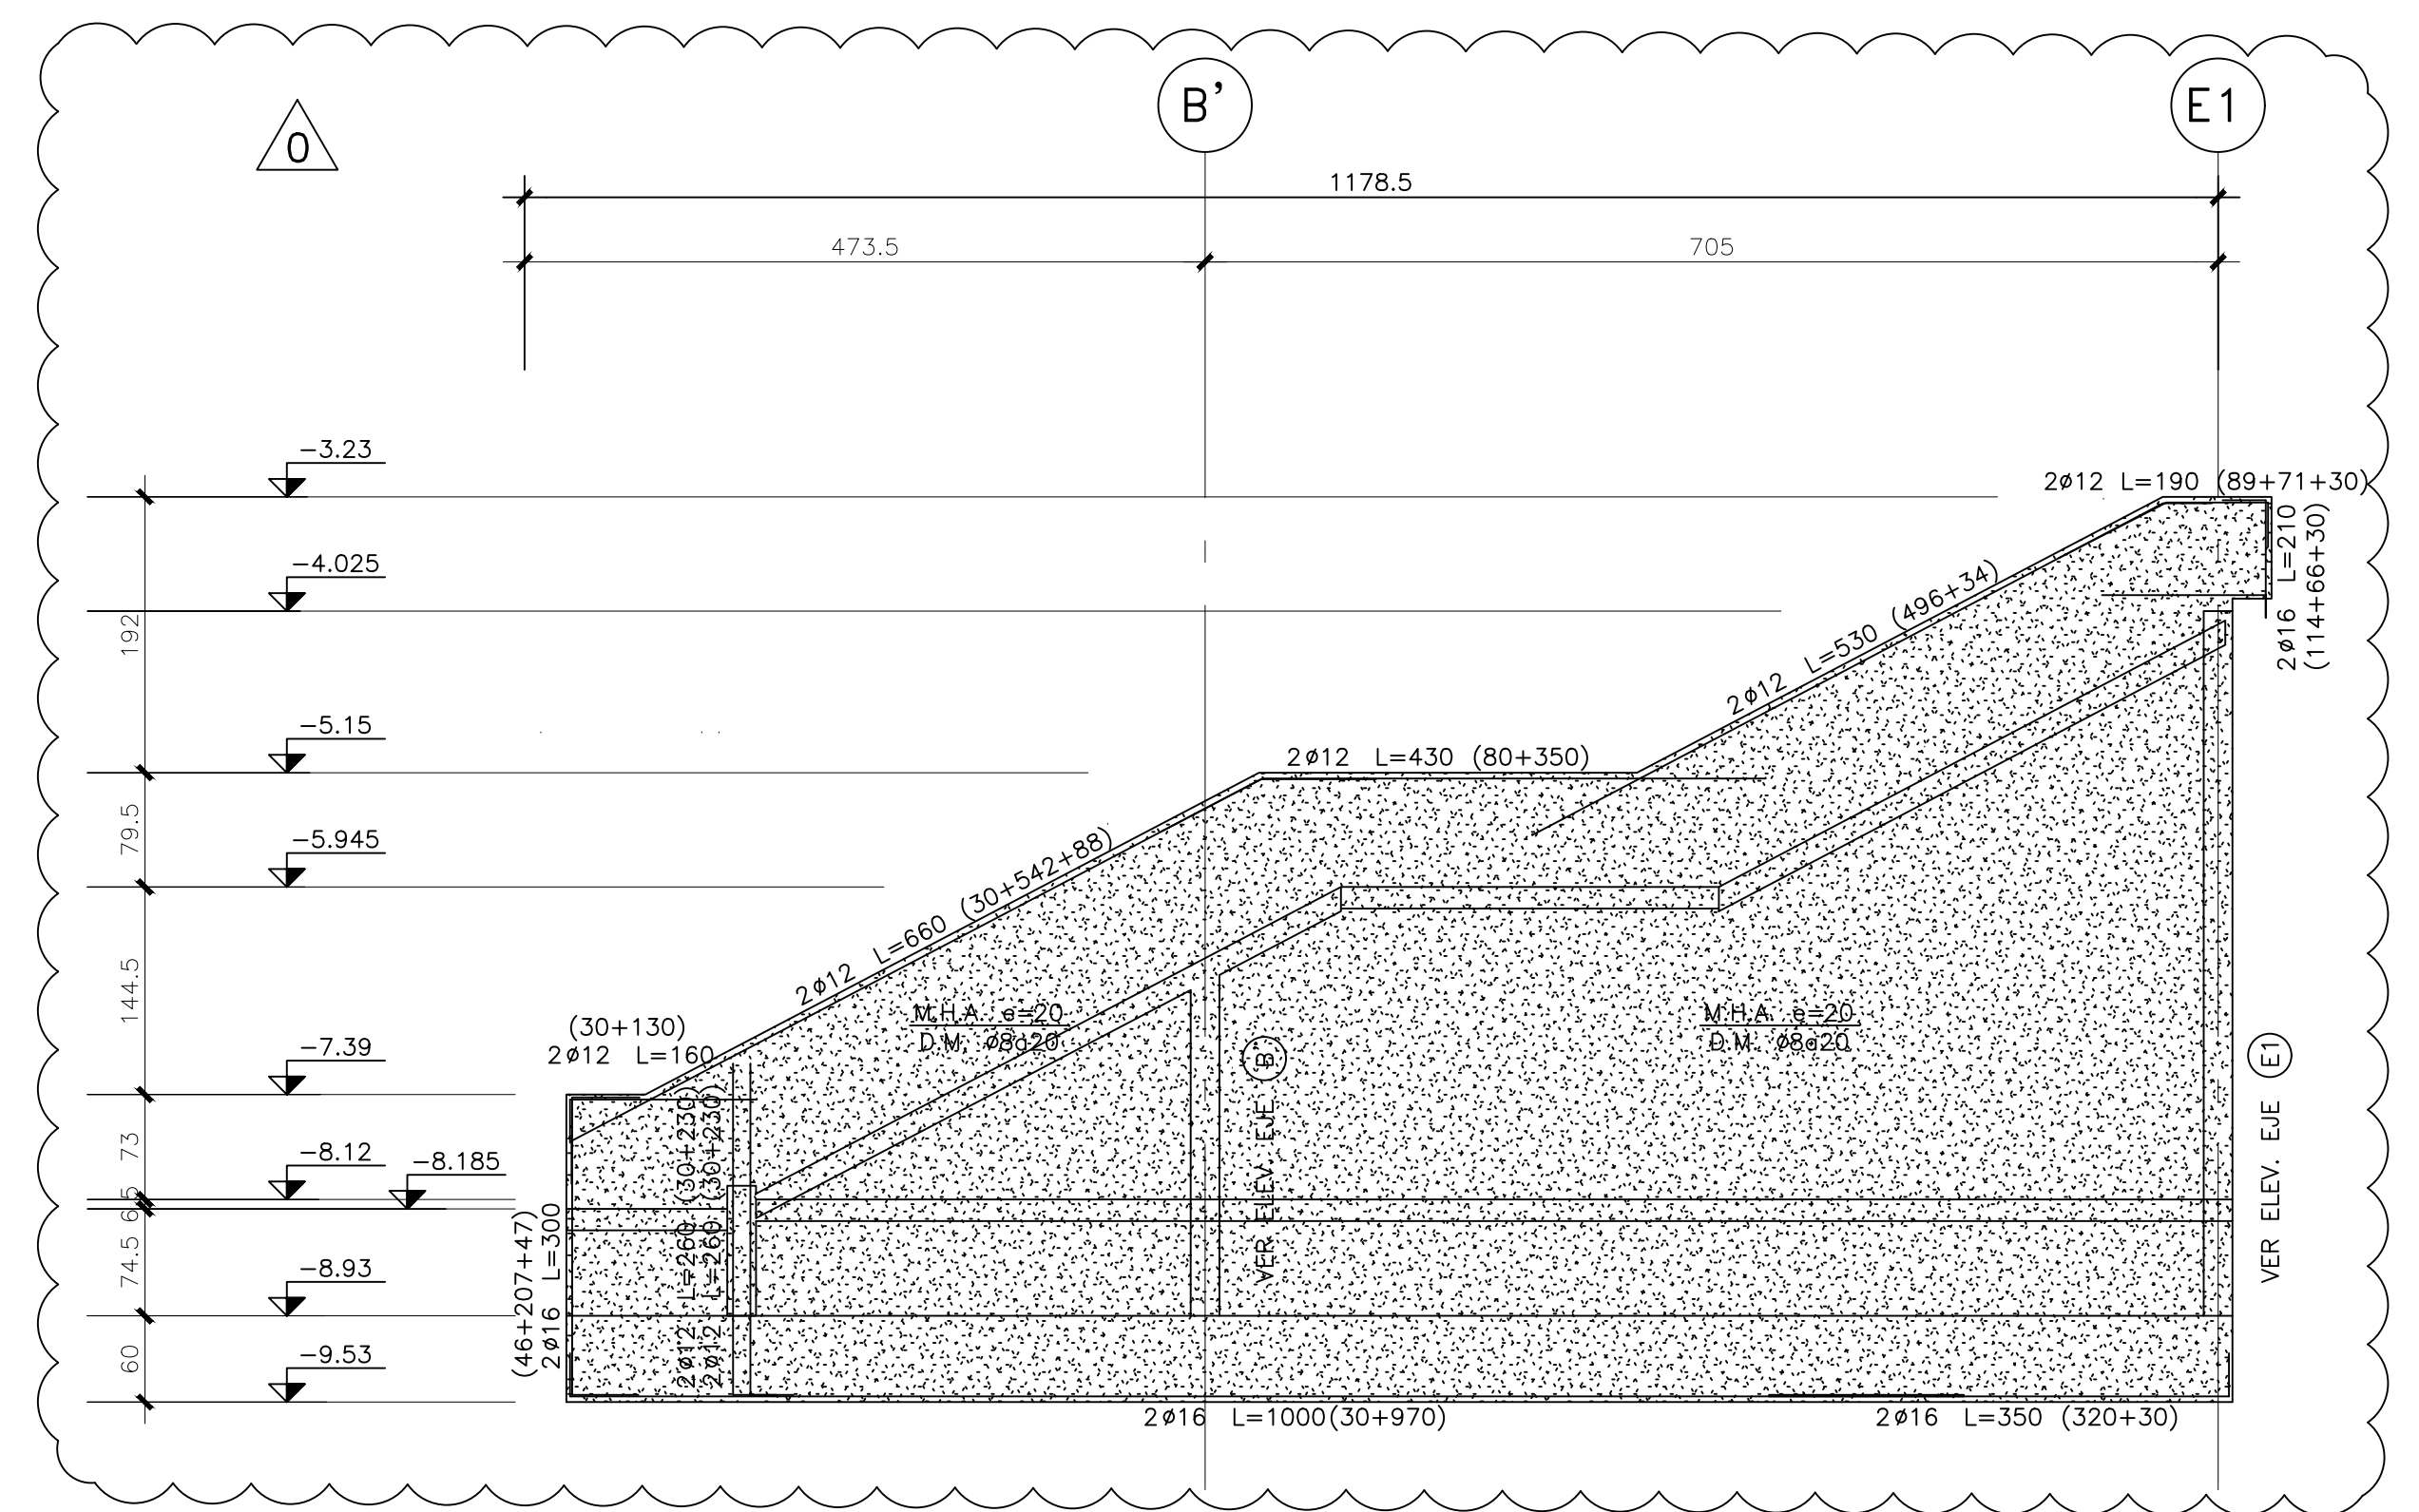

ELEVACION EJE 8B  
ESCALA 1:50

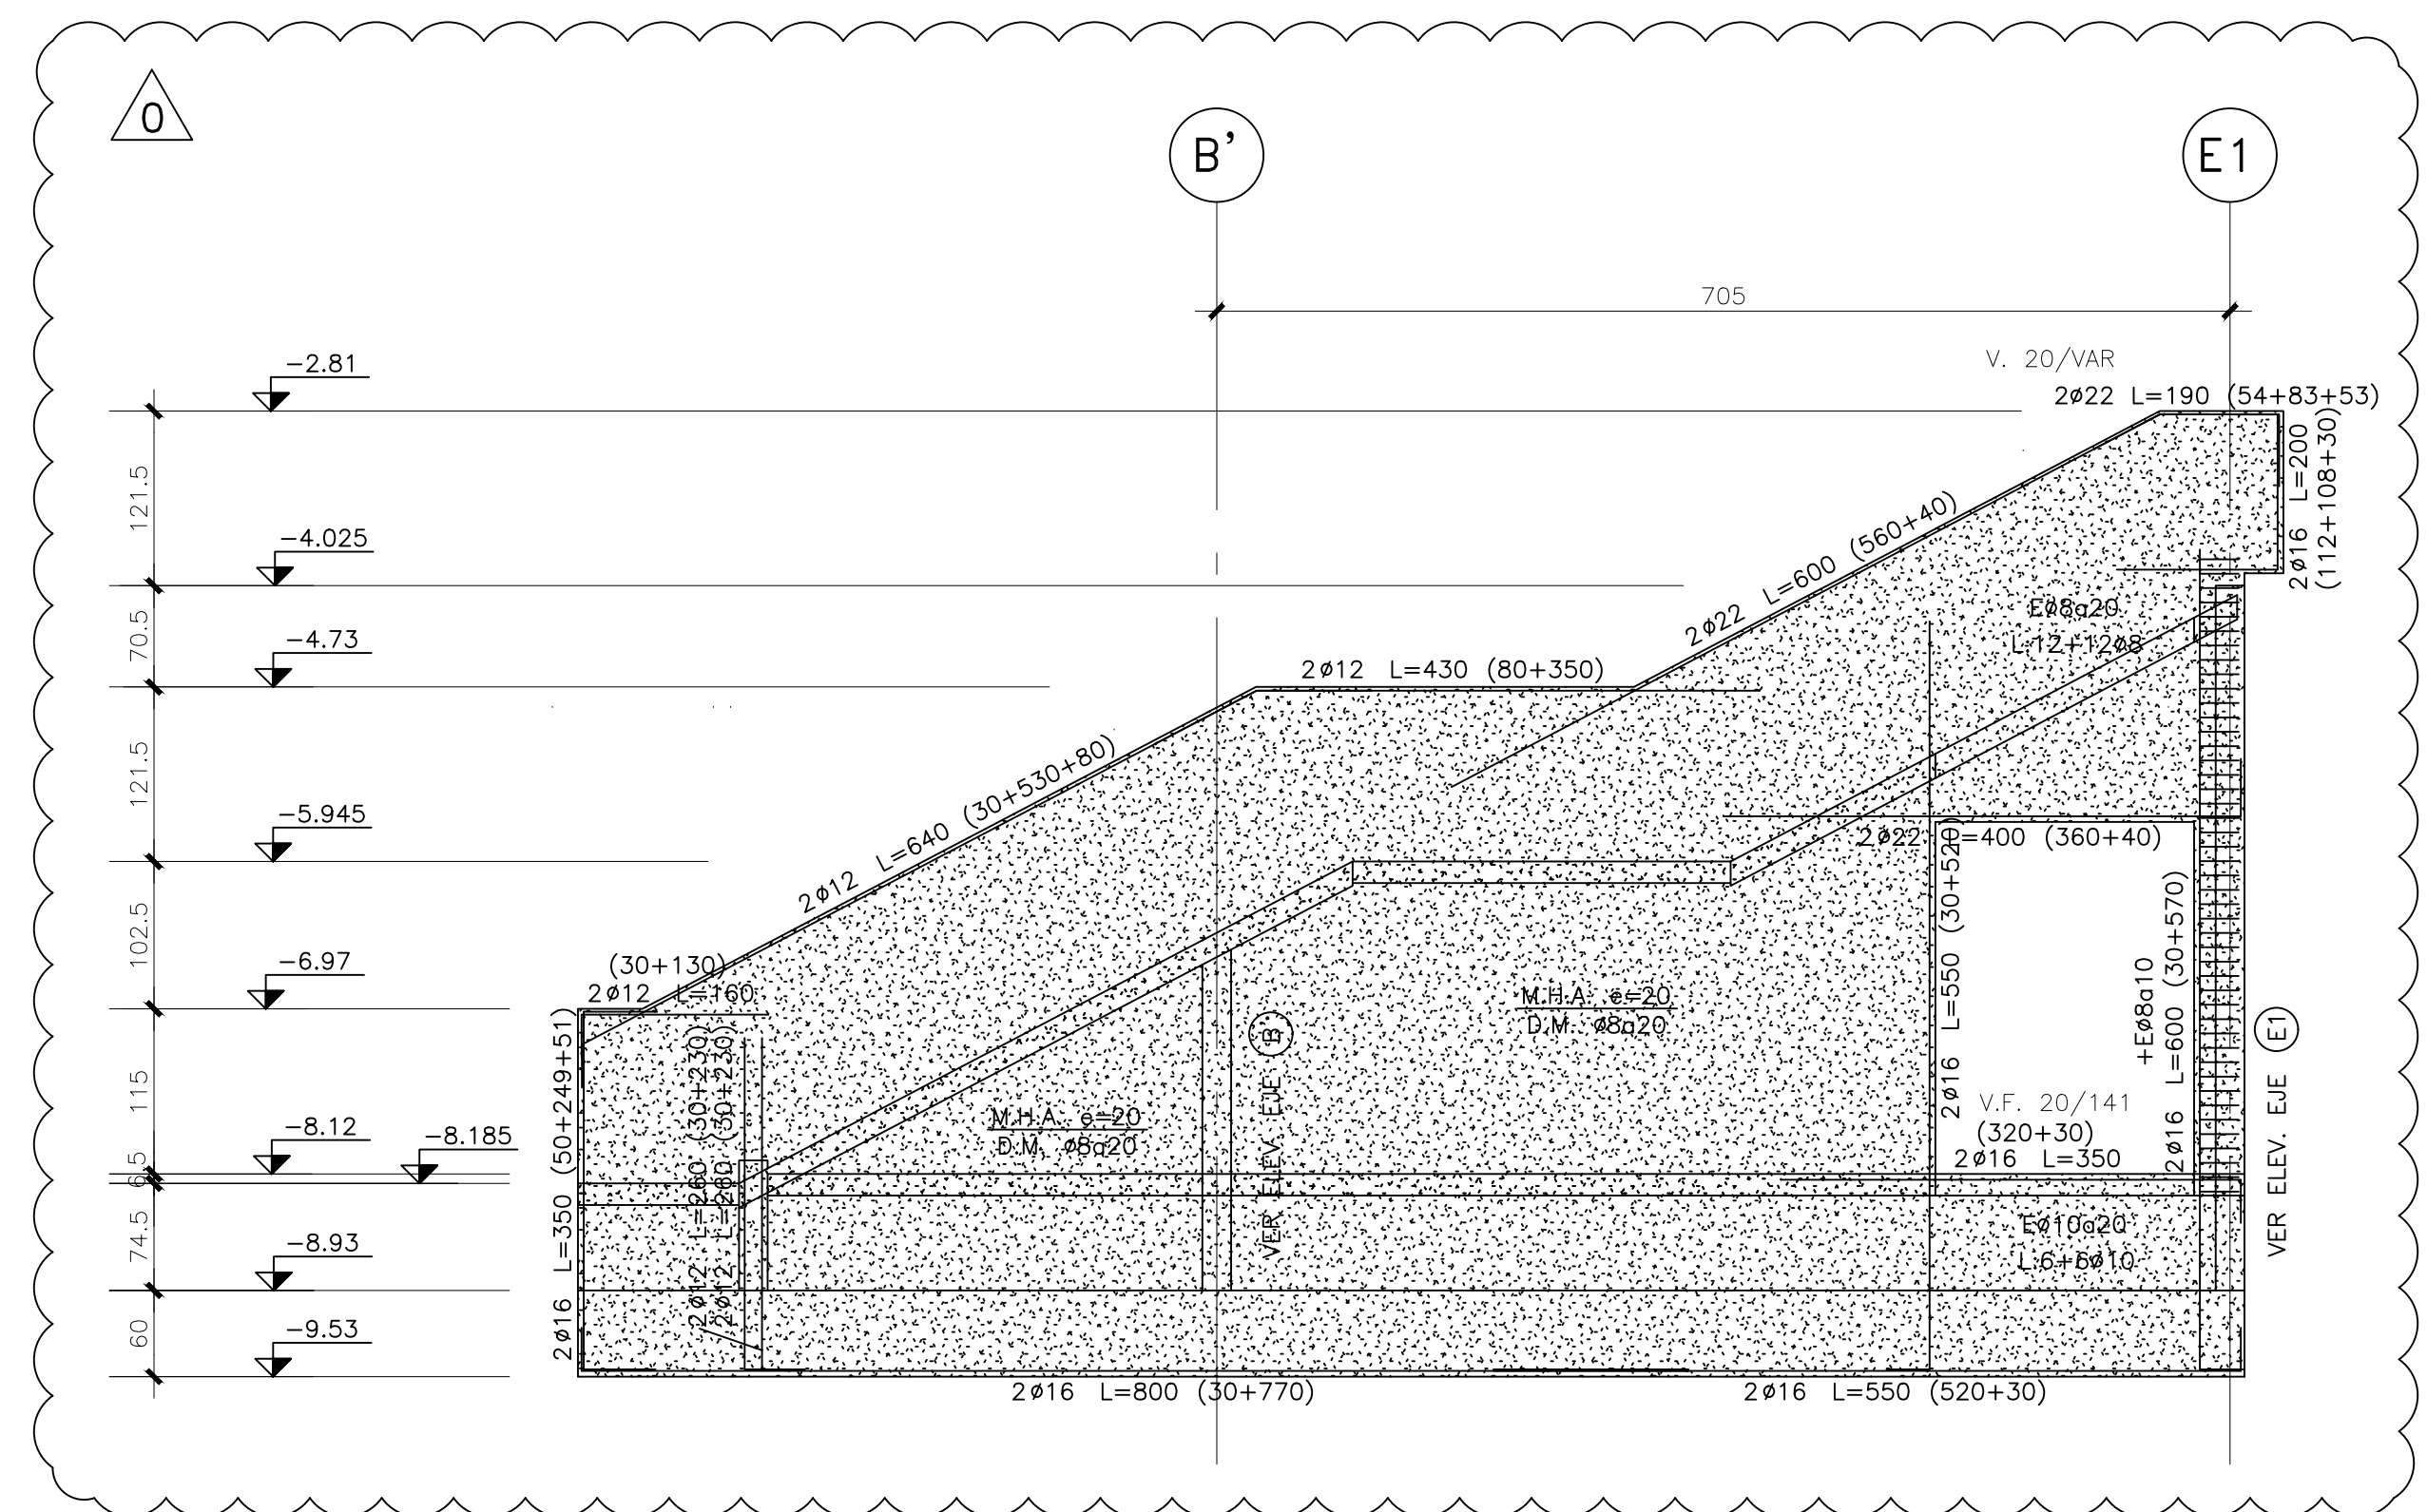

ELEVACION EJE 8A  
ESCALA 1:50