

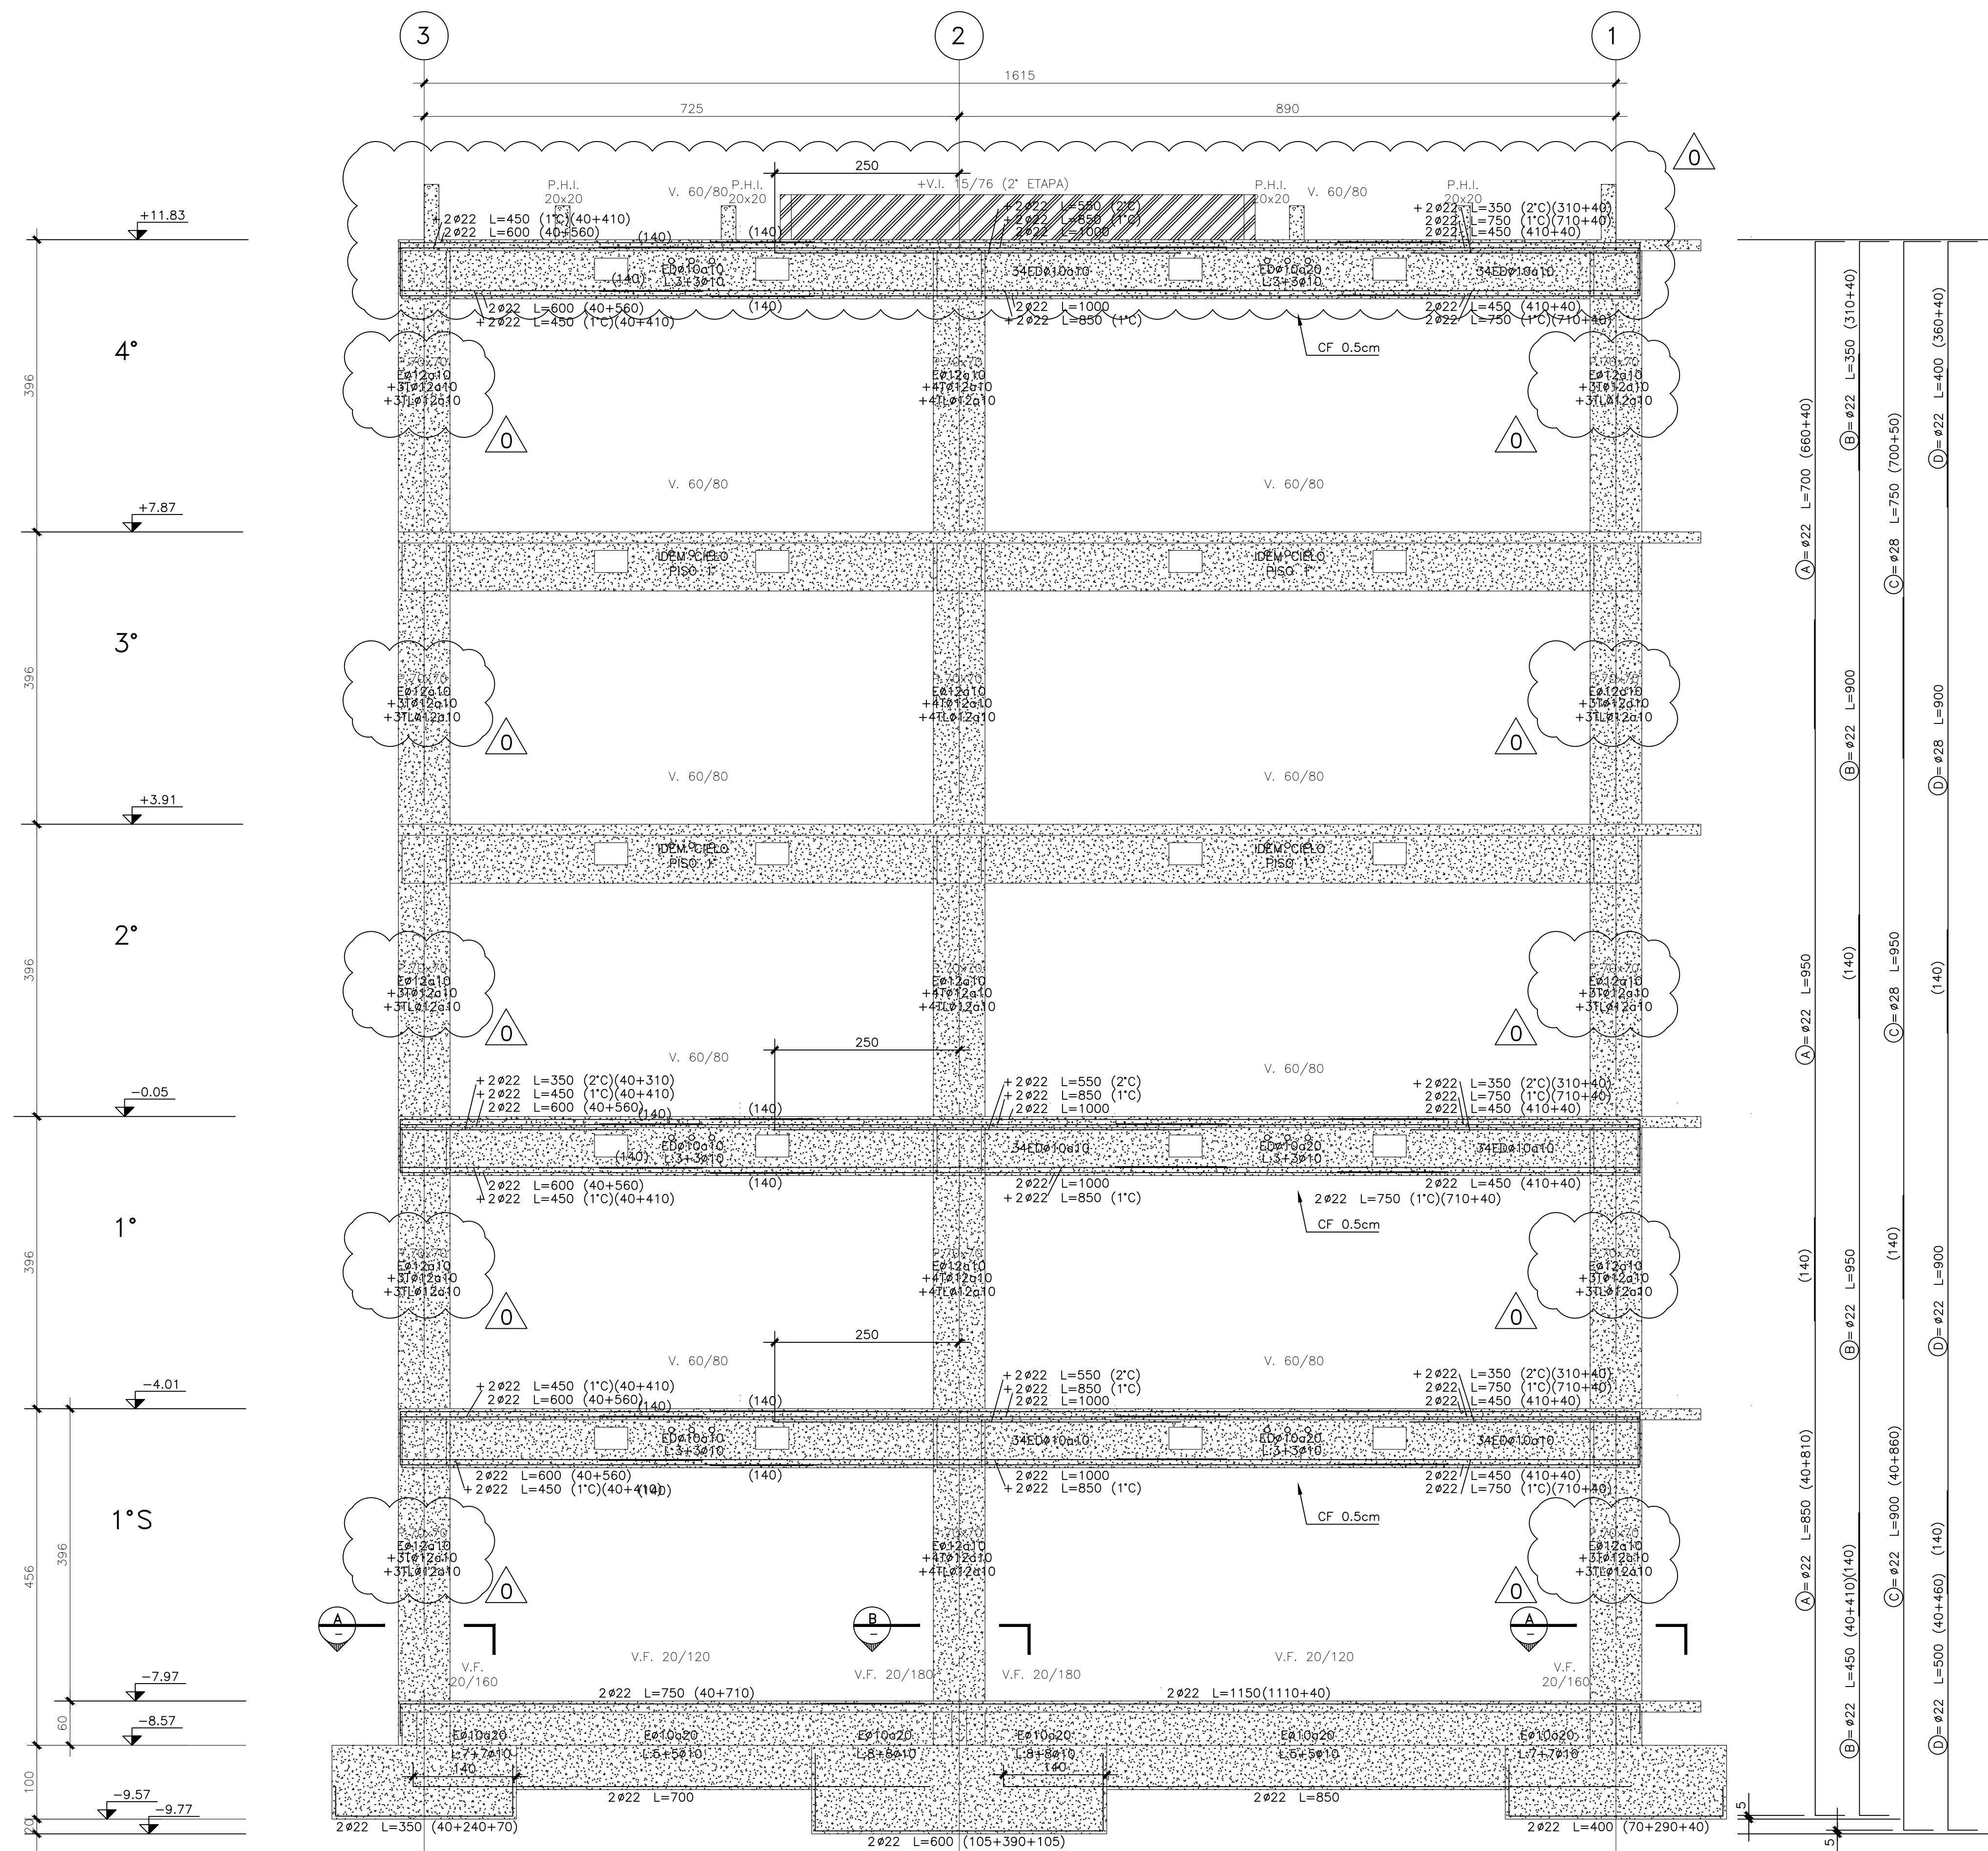


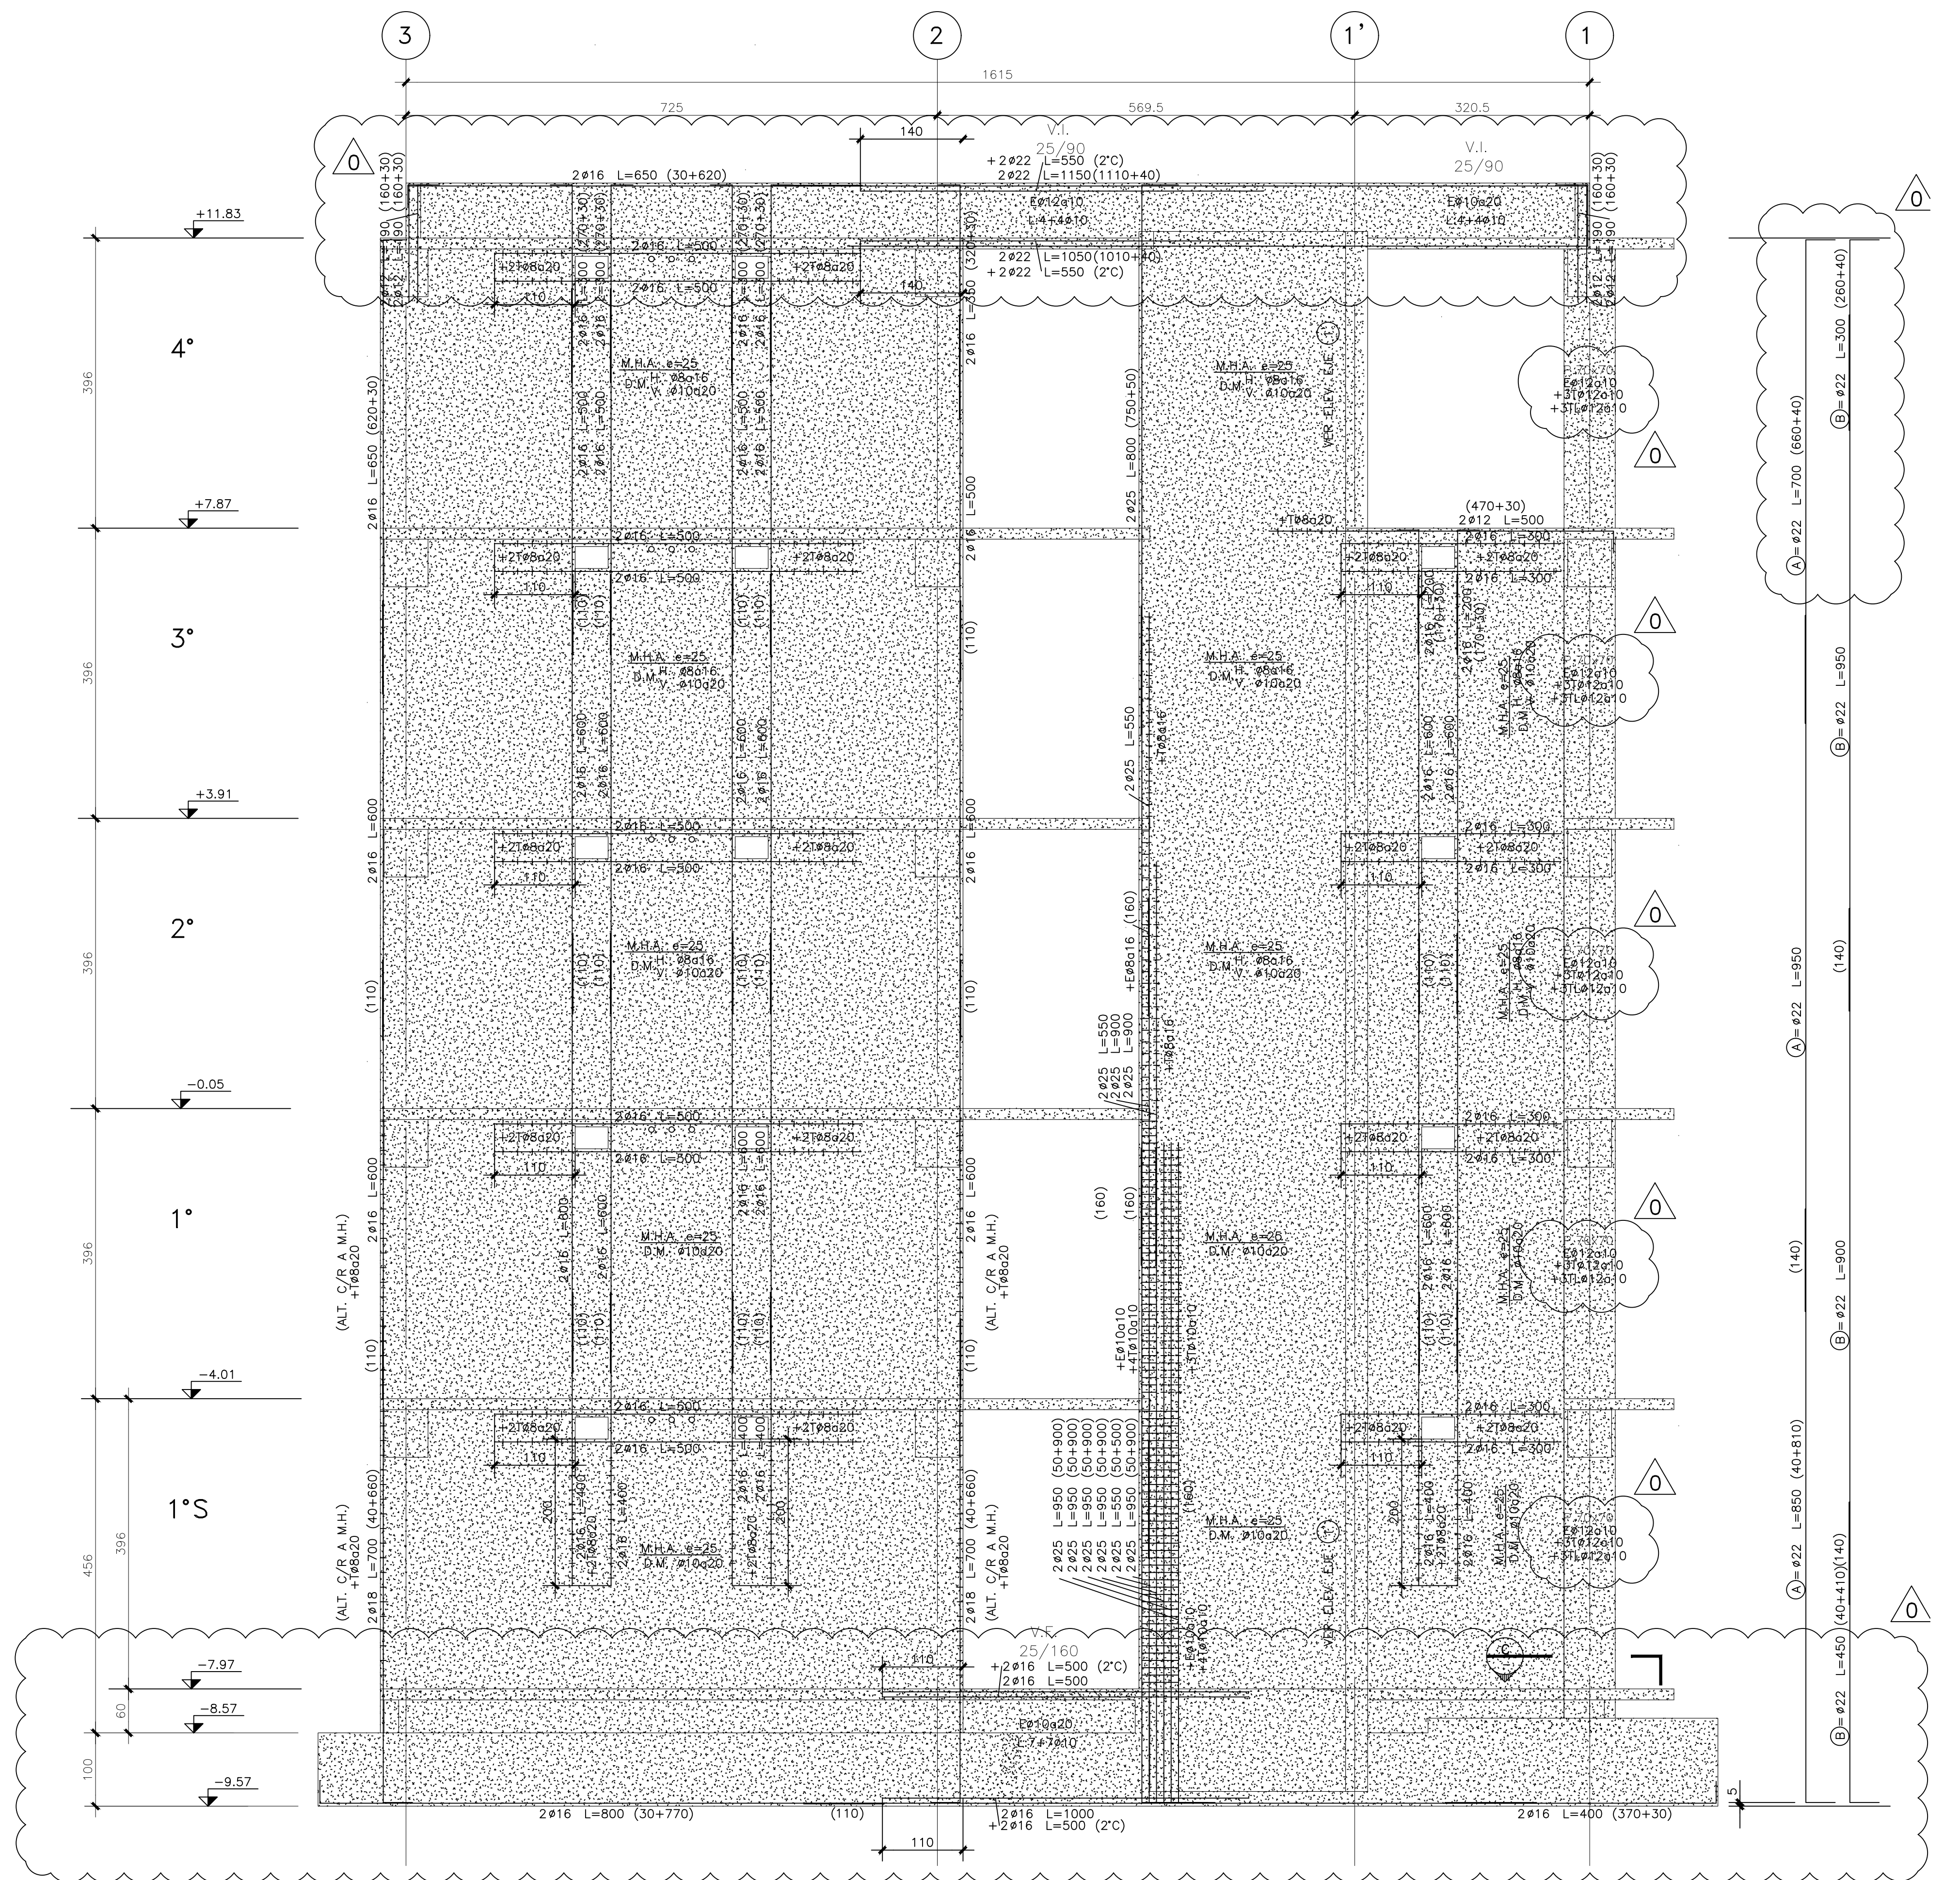

ELEVACION EJE C
ESCALA 1:50

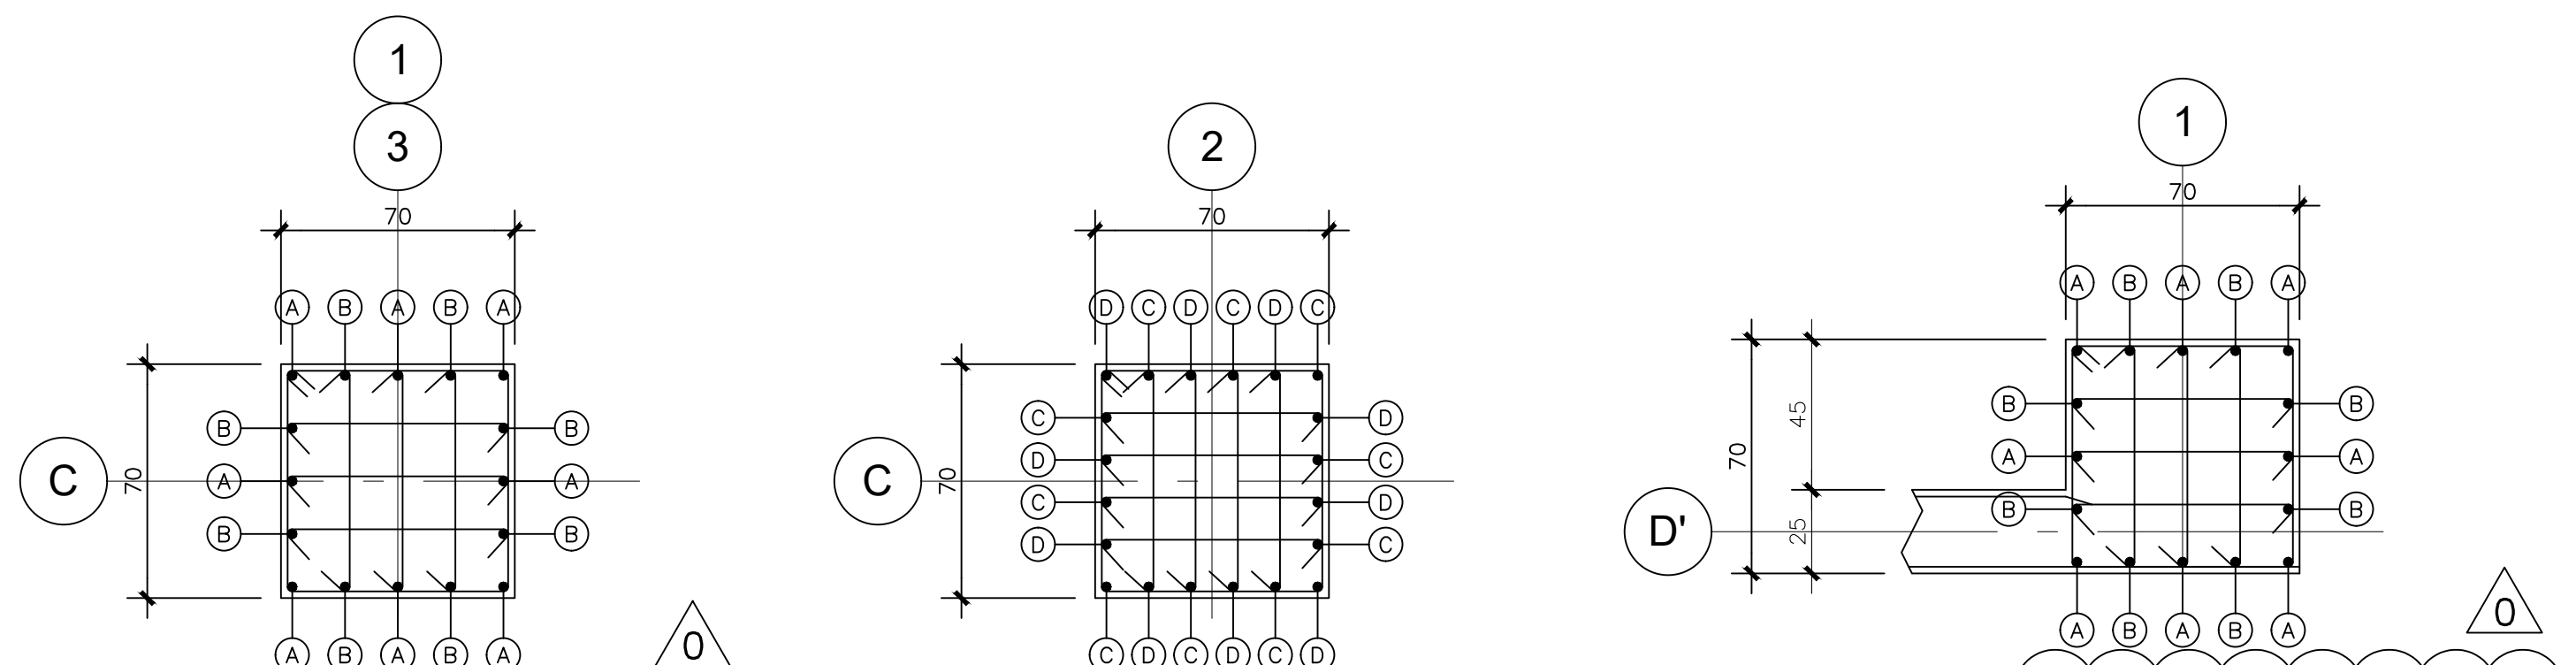

ELEVACION EJE D-D'
ESCALA 1:50