


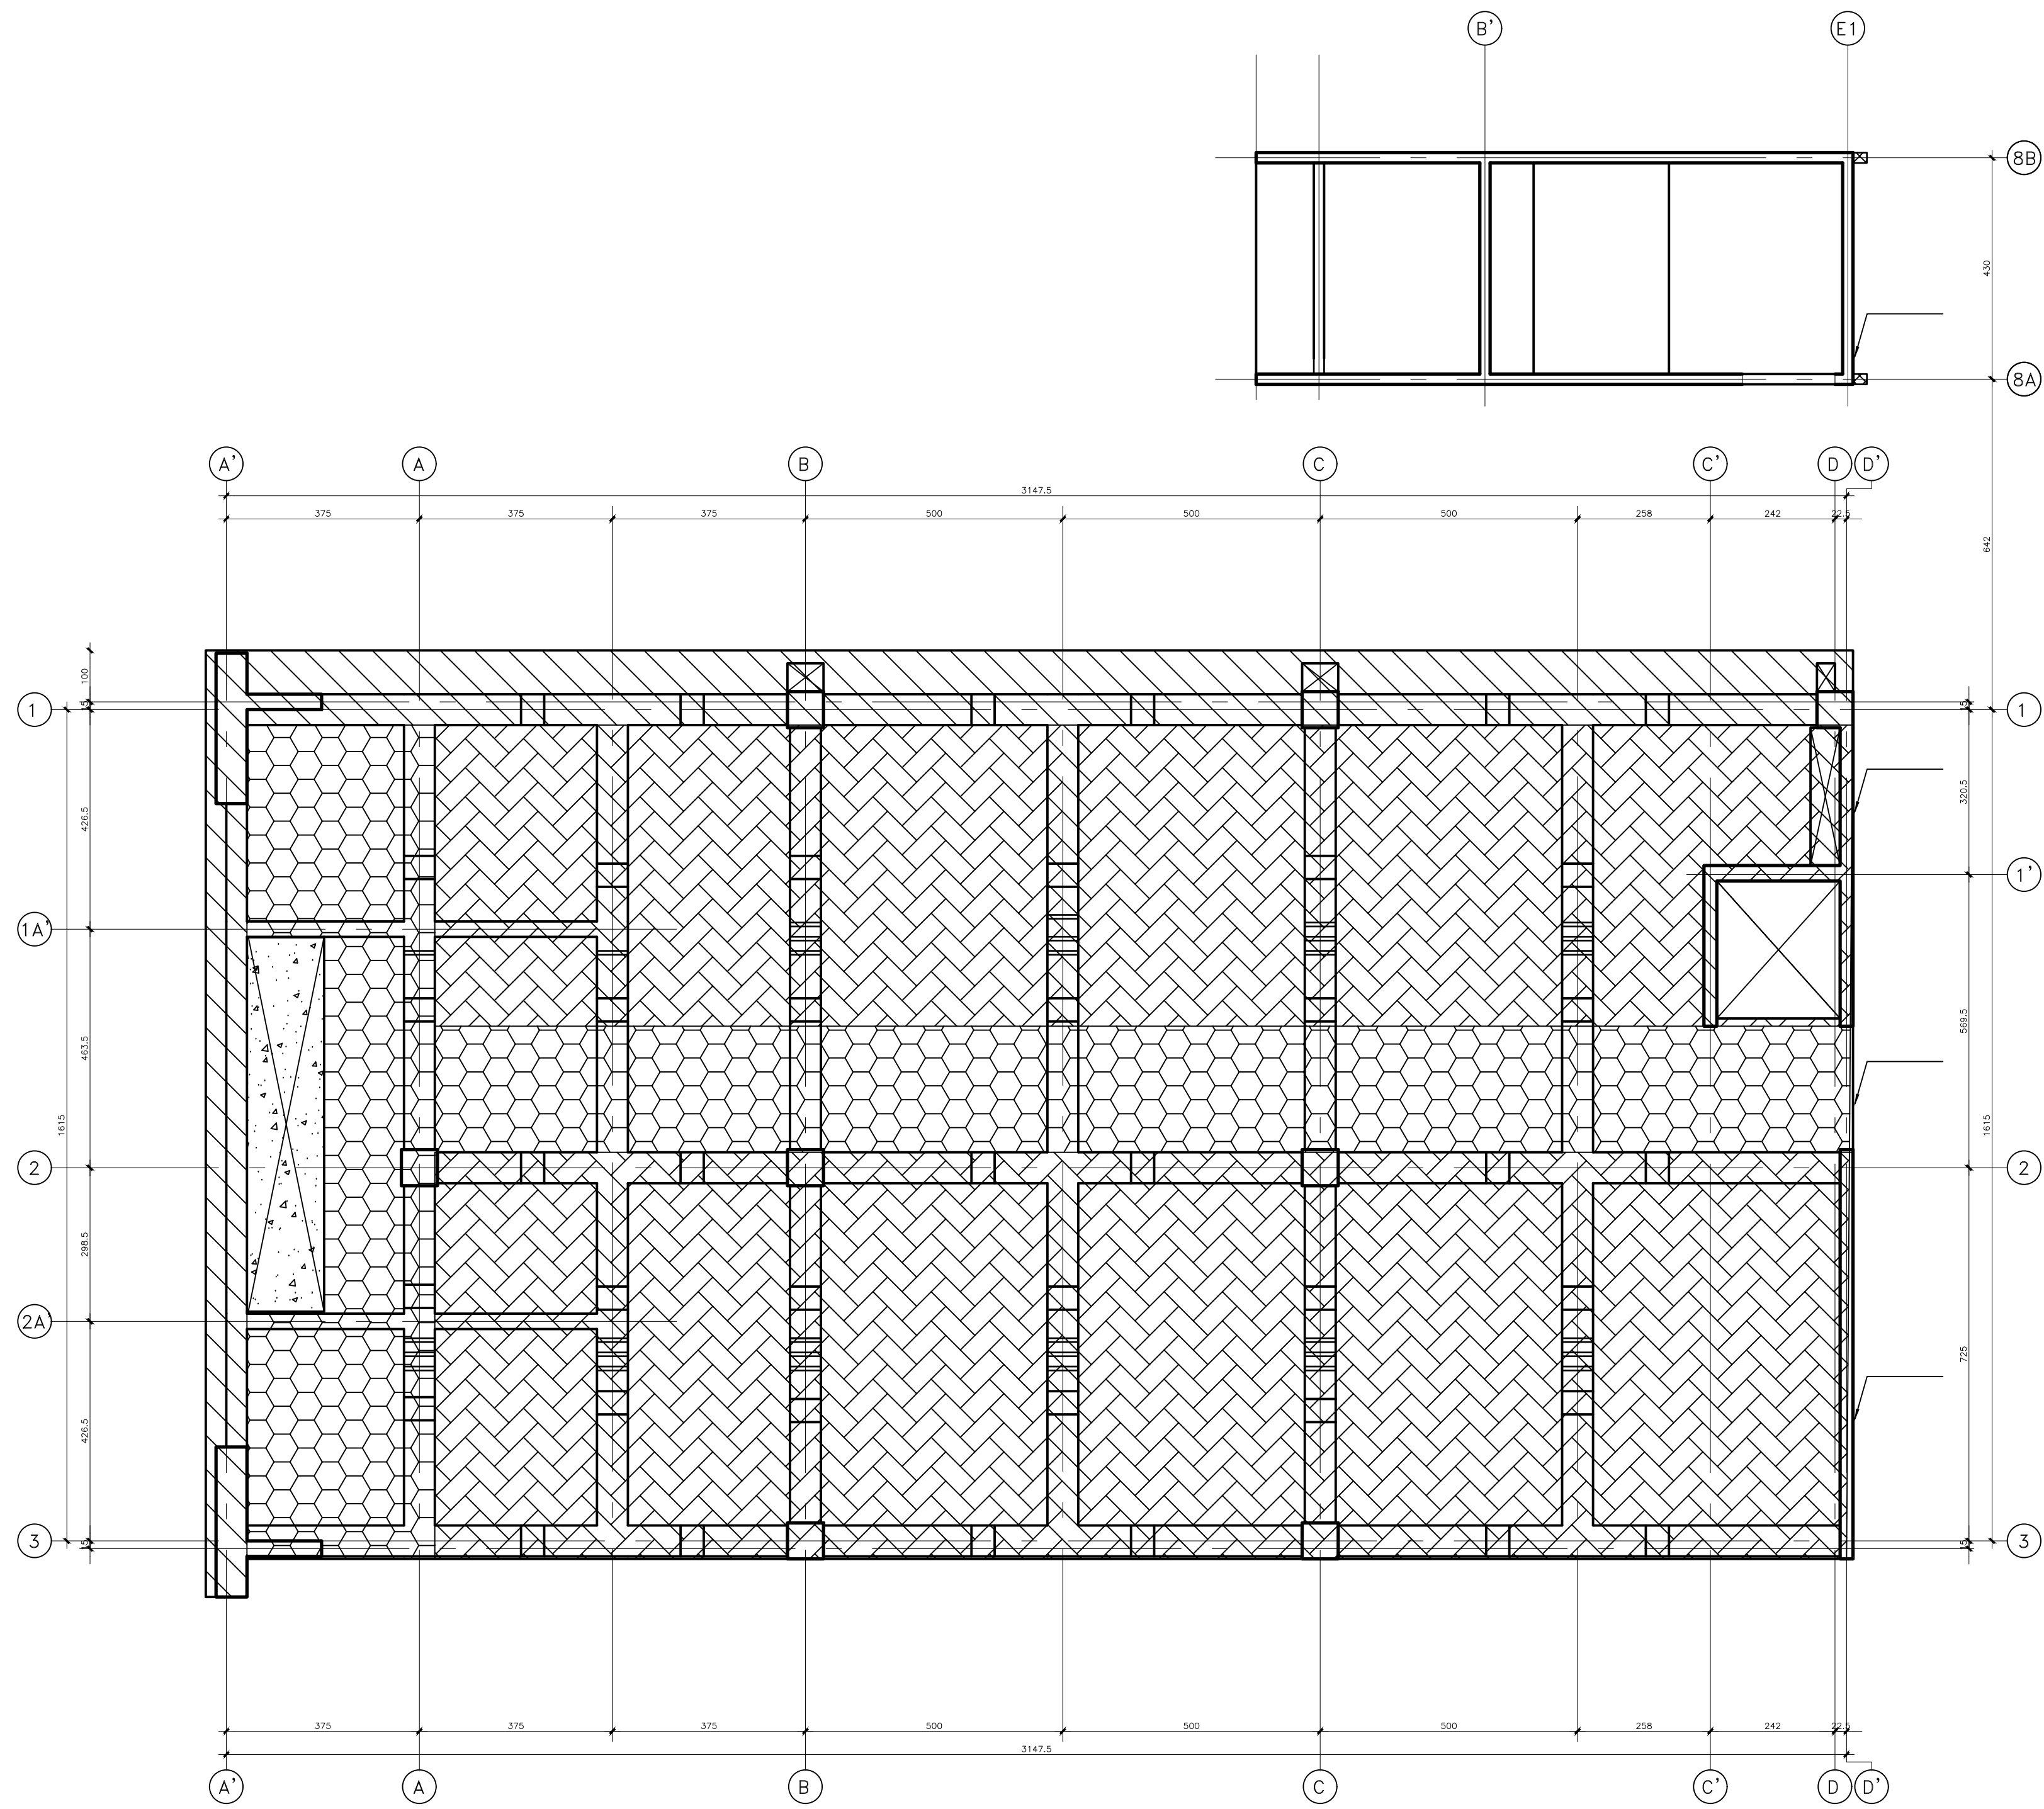


PLANTA CARGAS CIELO 1°SUBTERRANEO a CIELO PISO 3°

ESCALA 1:150

CARGAS DE DISEÑO		CARGAS DE DISEÑO	
PP. LOSA	= e(m)x2500 Kg/m ³	PP. LOSA	= e(m)x2500 Kg/m ³
PM. ADIC.	= 260 Kg/m ²	PM. ADIC.	= 260 Kg/m ²
SC	= 500 Kg/m ²	SC	= 300 Kg/m ²

CARGAS DE DISEÑO		CARGAS DE DISEÑO	
PP. LOSA	= e(m)x2500 Kg/m ³	PP. LOSA	= e(m)x2500 Kg/m ³
PM. ADIC.	= 260 Kg/m ²	PM. ADIC.	= 260 Kg/m ²
SC	= 200 Kg/m ²	SC	= 500 Kg/m ²

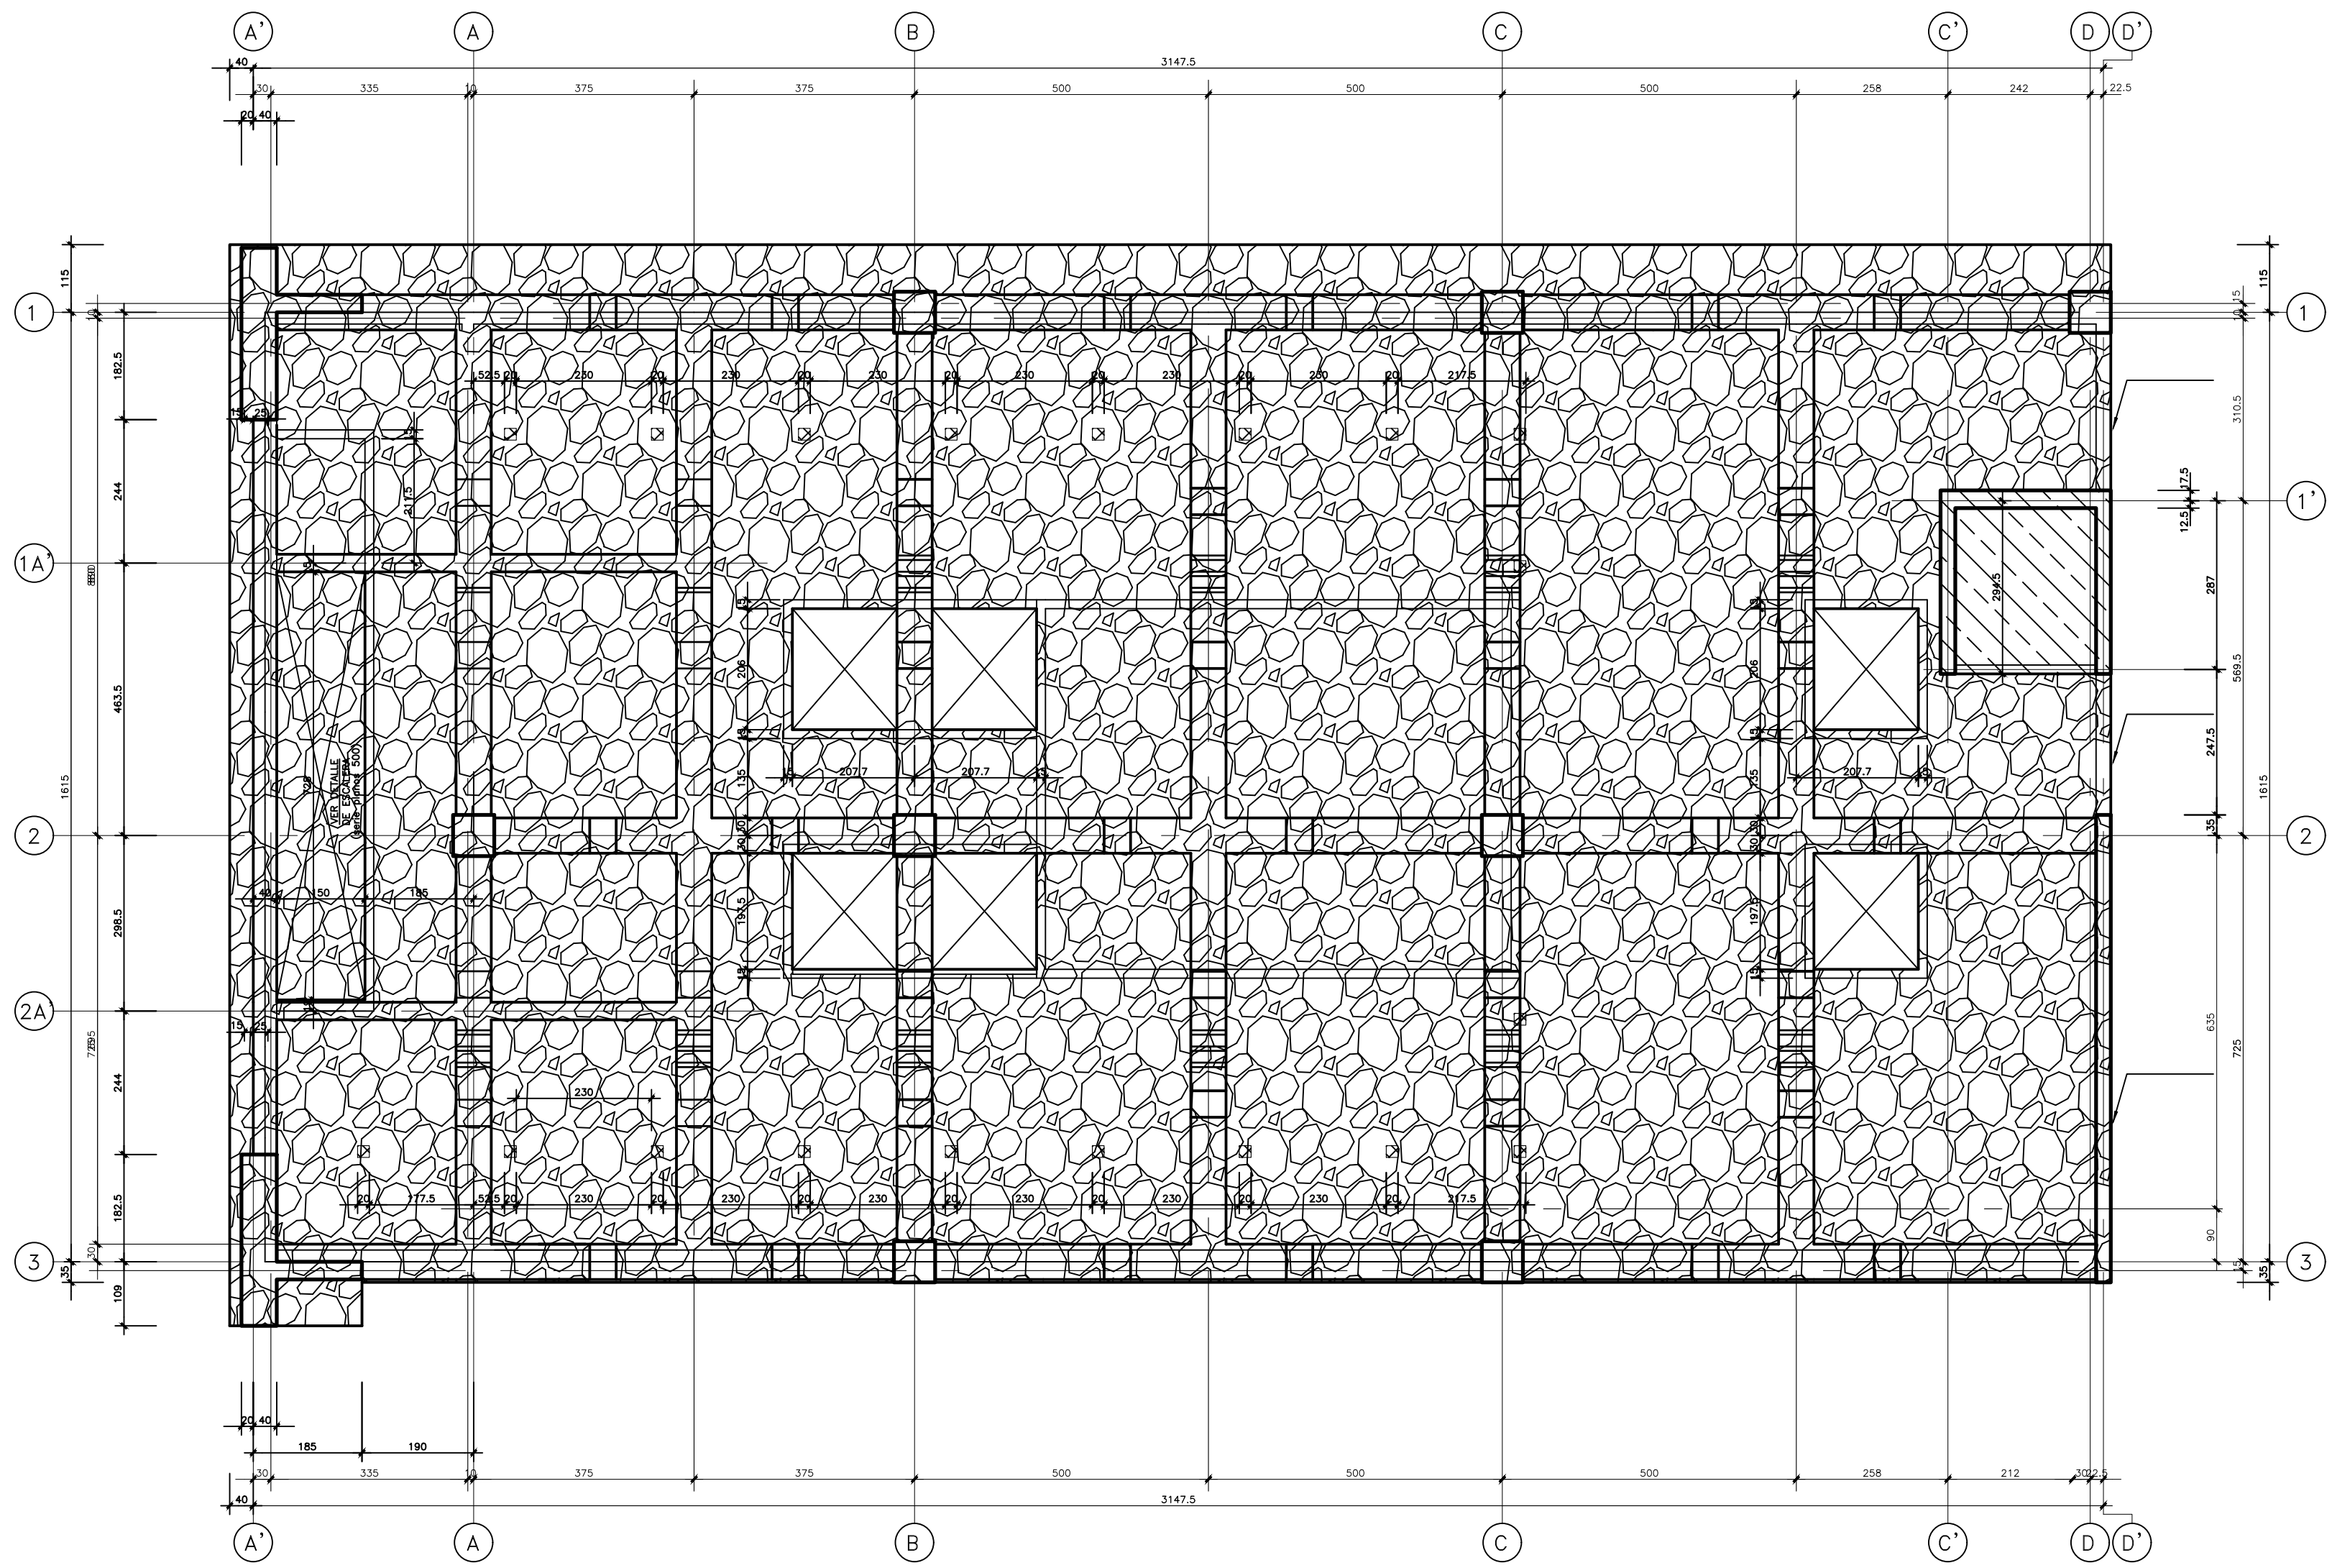

PLANTA CARGAS CIELO PISO 4°

ESCALA 1:150

CARGAS DE DISEÑO		CARGAS DE DISEÑO (CARGA LINEAL)	
PP. LOSA	= e(m)x2500 Kg/m ³	PP. LOSA	= e(m)x2500 Kg/m ³
PM. ADIC.	= 200 Kg/m ²	PM. ADIC.	= 1500 Kg/m
SC	= 200 Kg/m ²	SC	= 100 Kg/m