


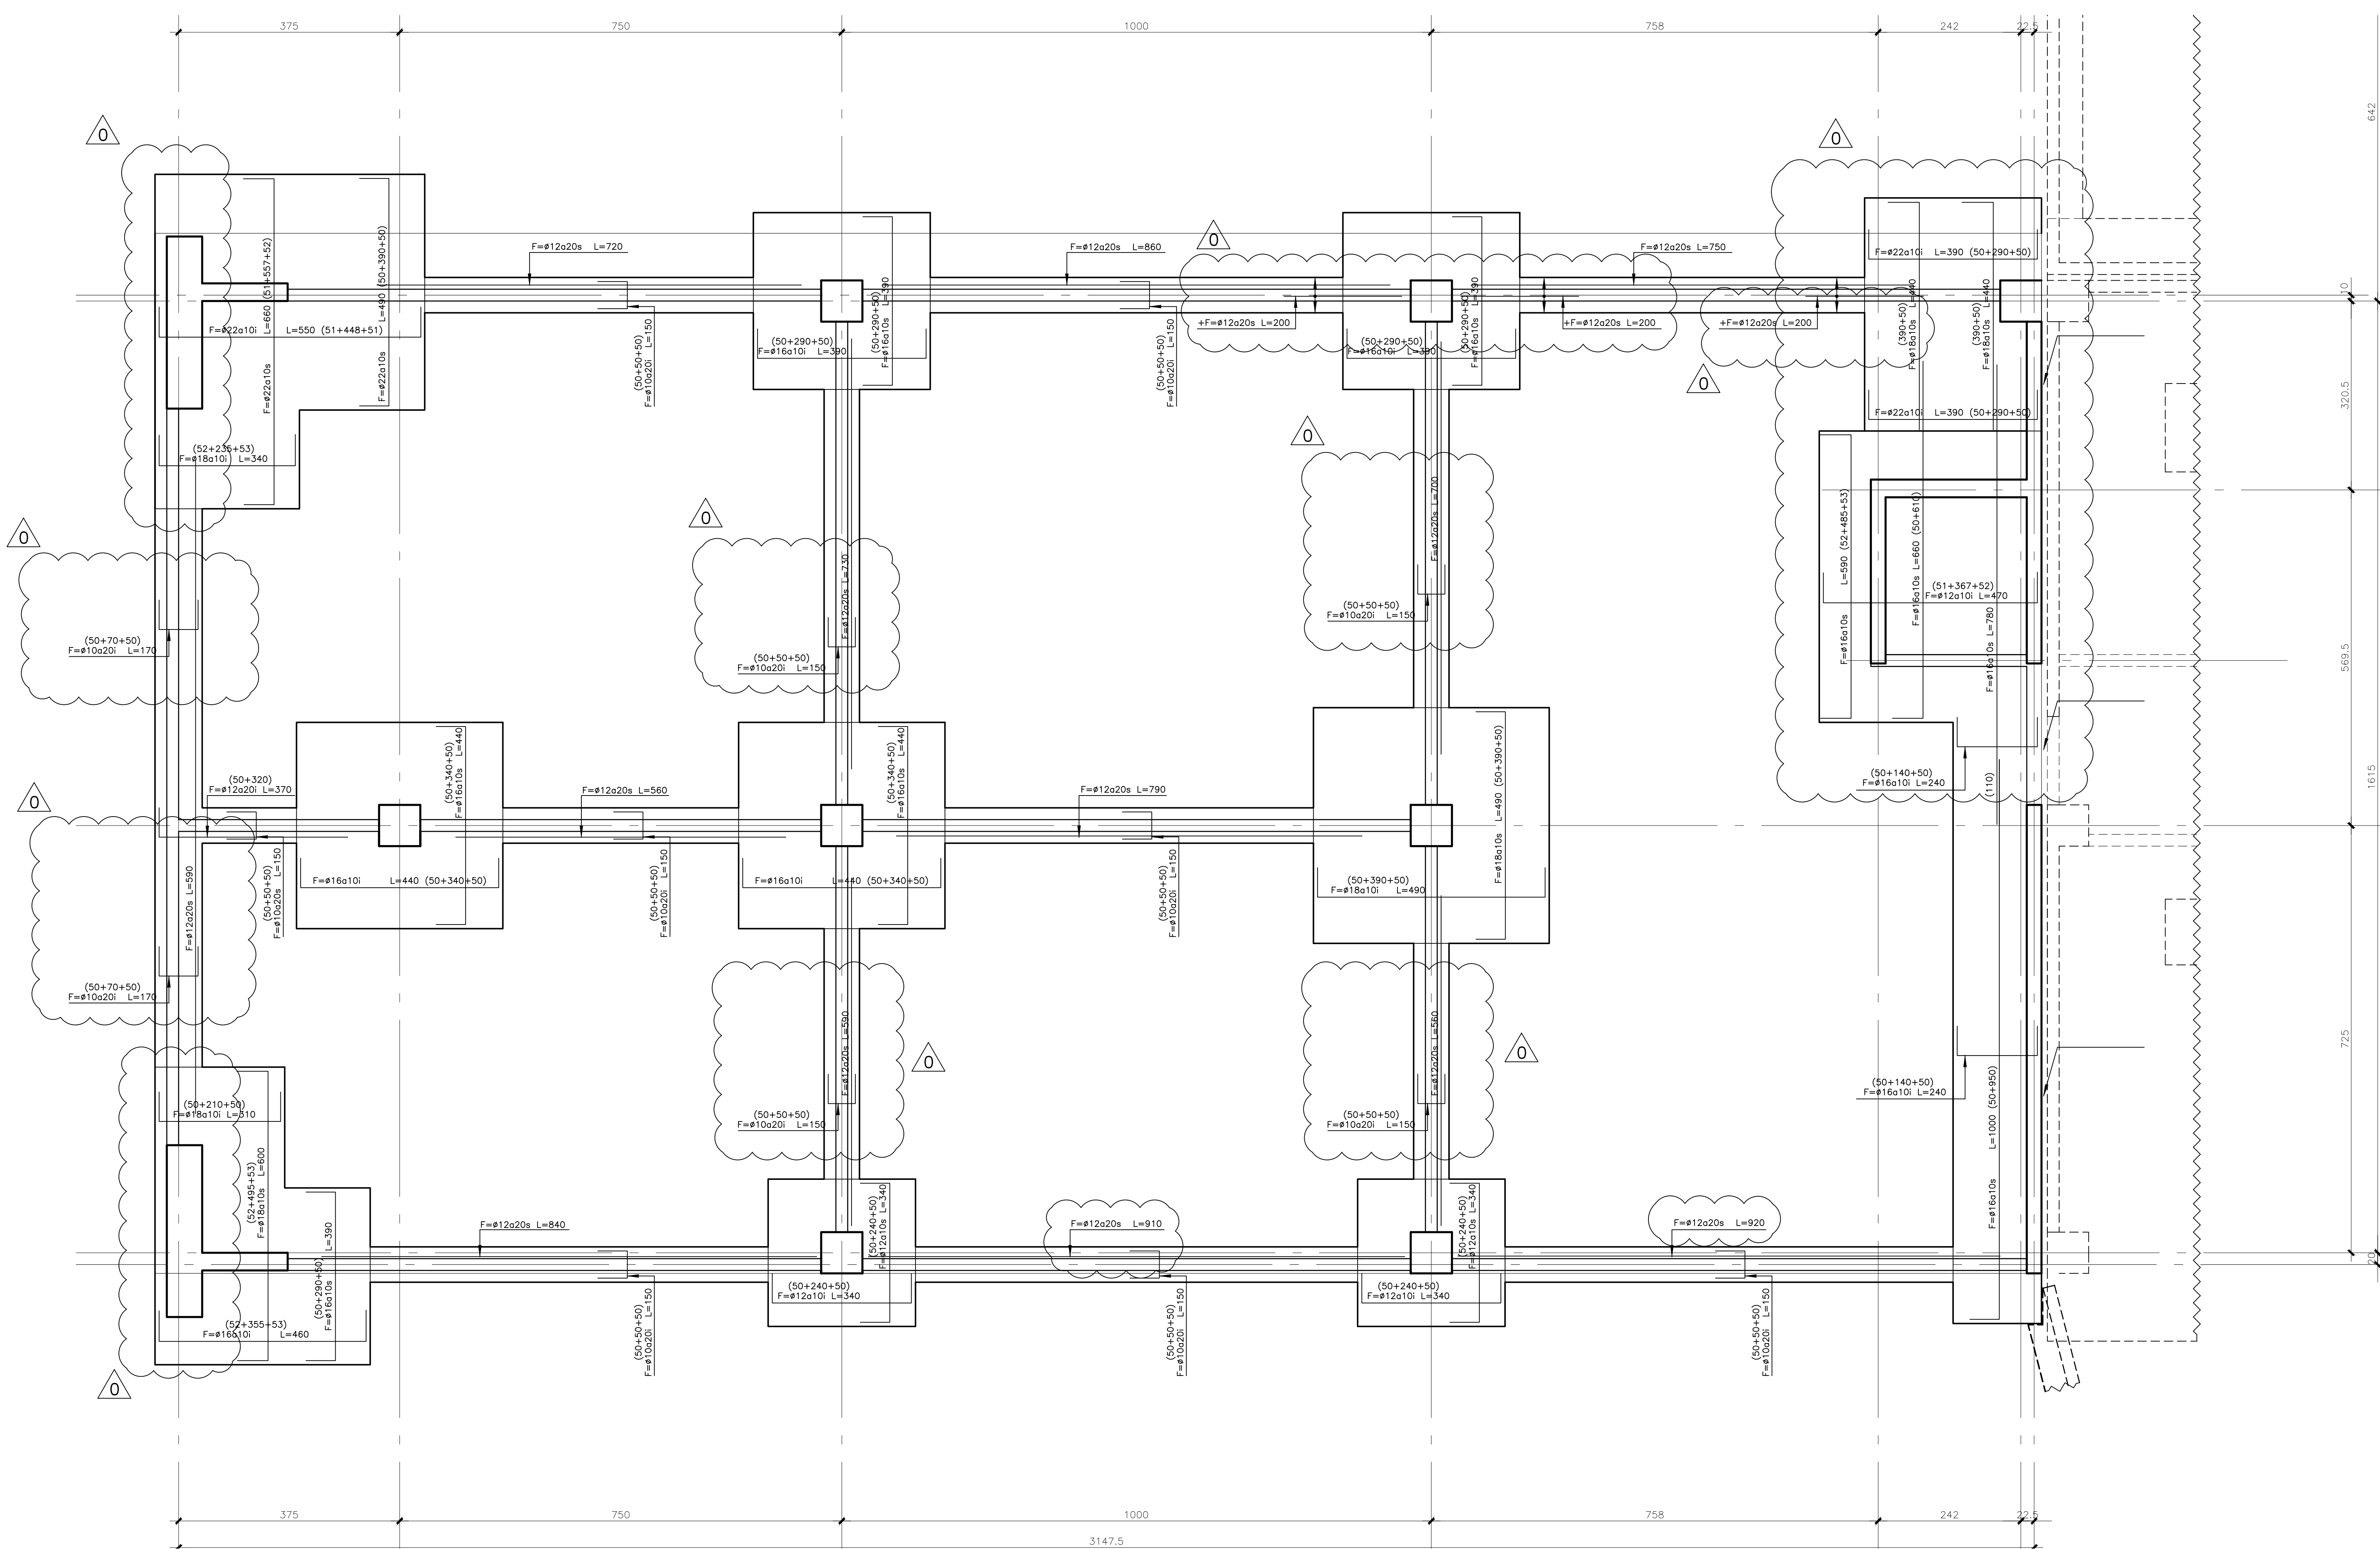

PLANTA ARMADURA INFERIOR FUNDACIONES (F)

ESCALA 1:50

ESTADO:		APROBADO PARA:	
EN DESARROLLO	PRELIMINAR	PROPUESTA	CONSTRUCCION
Nº	REVISION	ING. / DIB.	FECH
1	SE EMITE PARA CONSTRUCCION	MKC/ARB	24/10/