


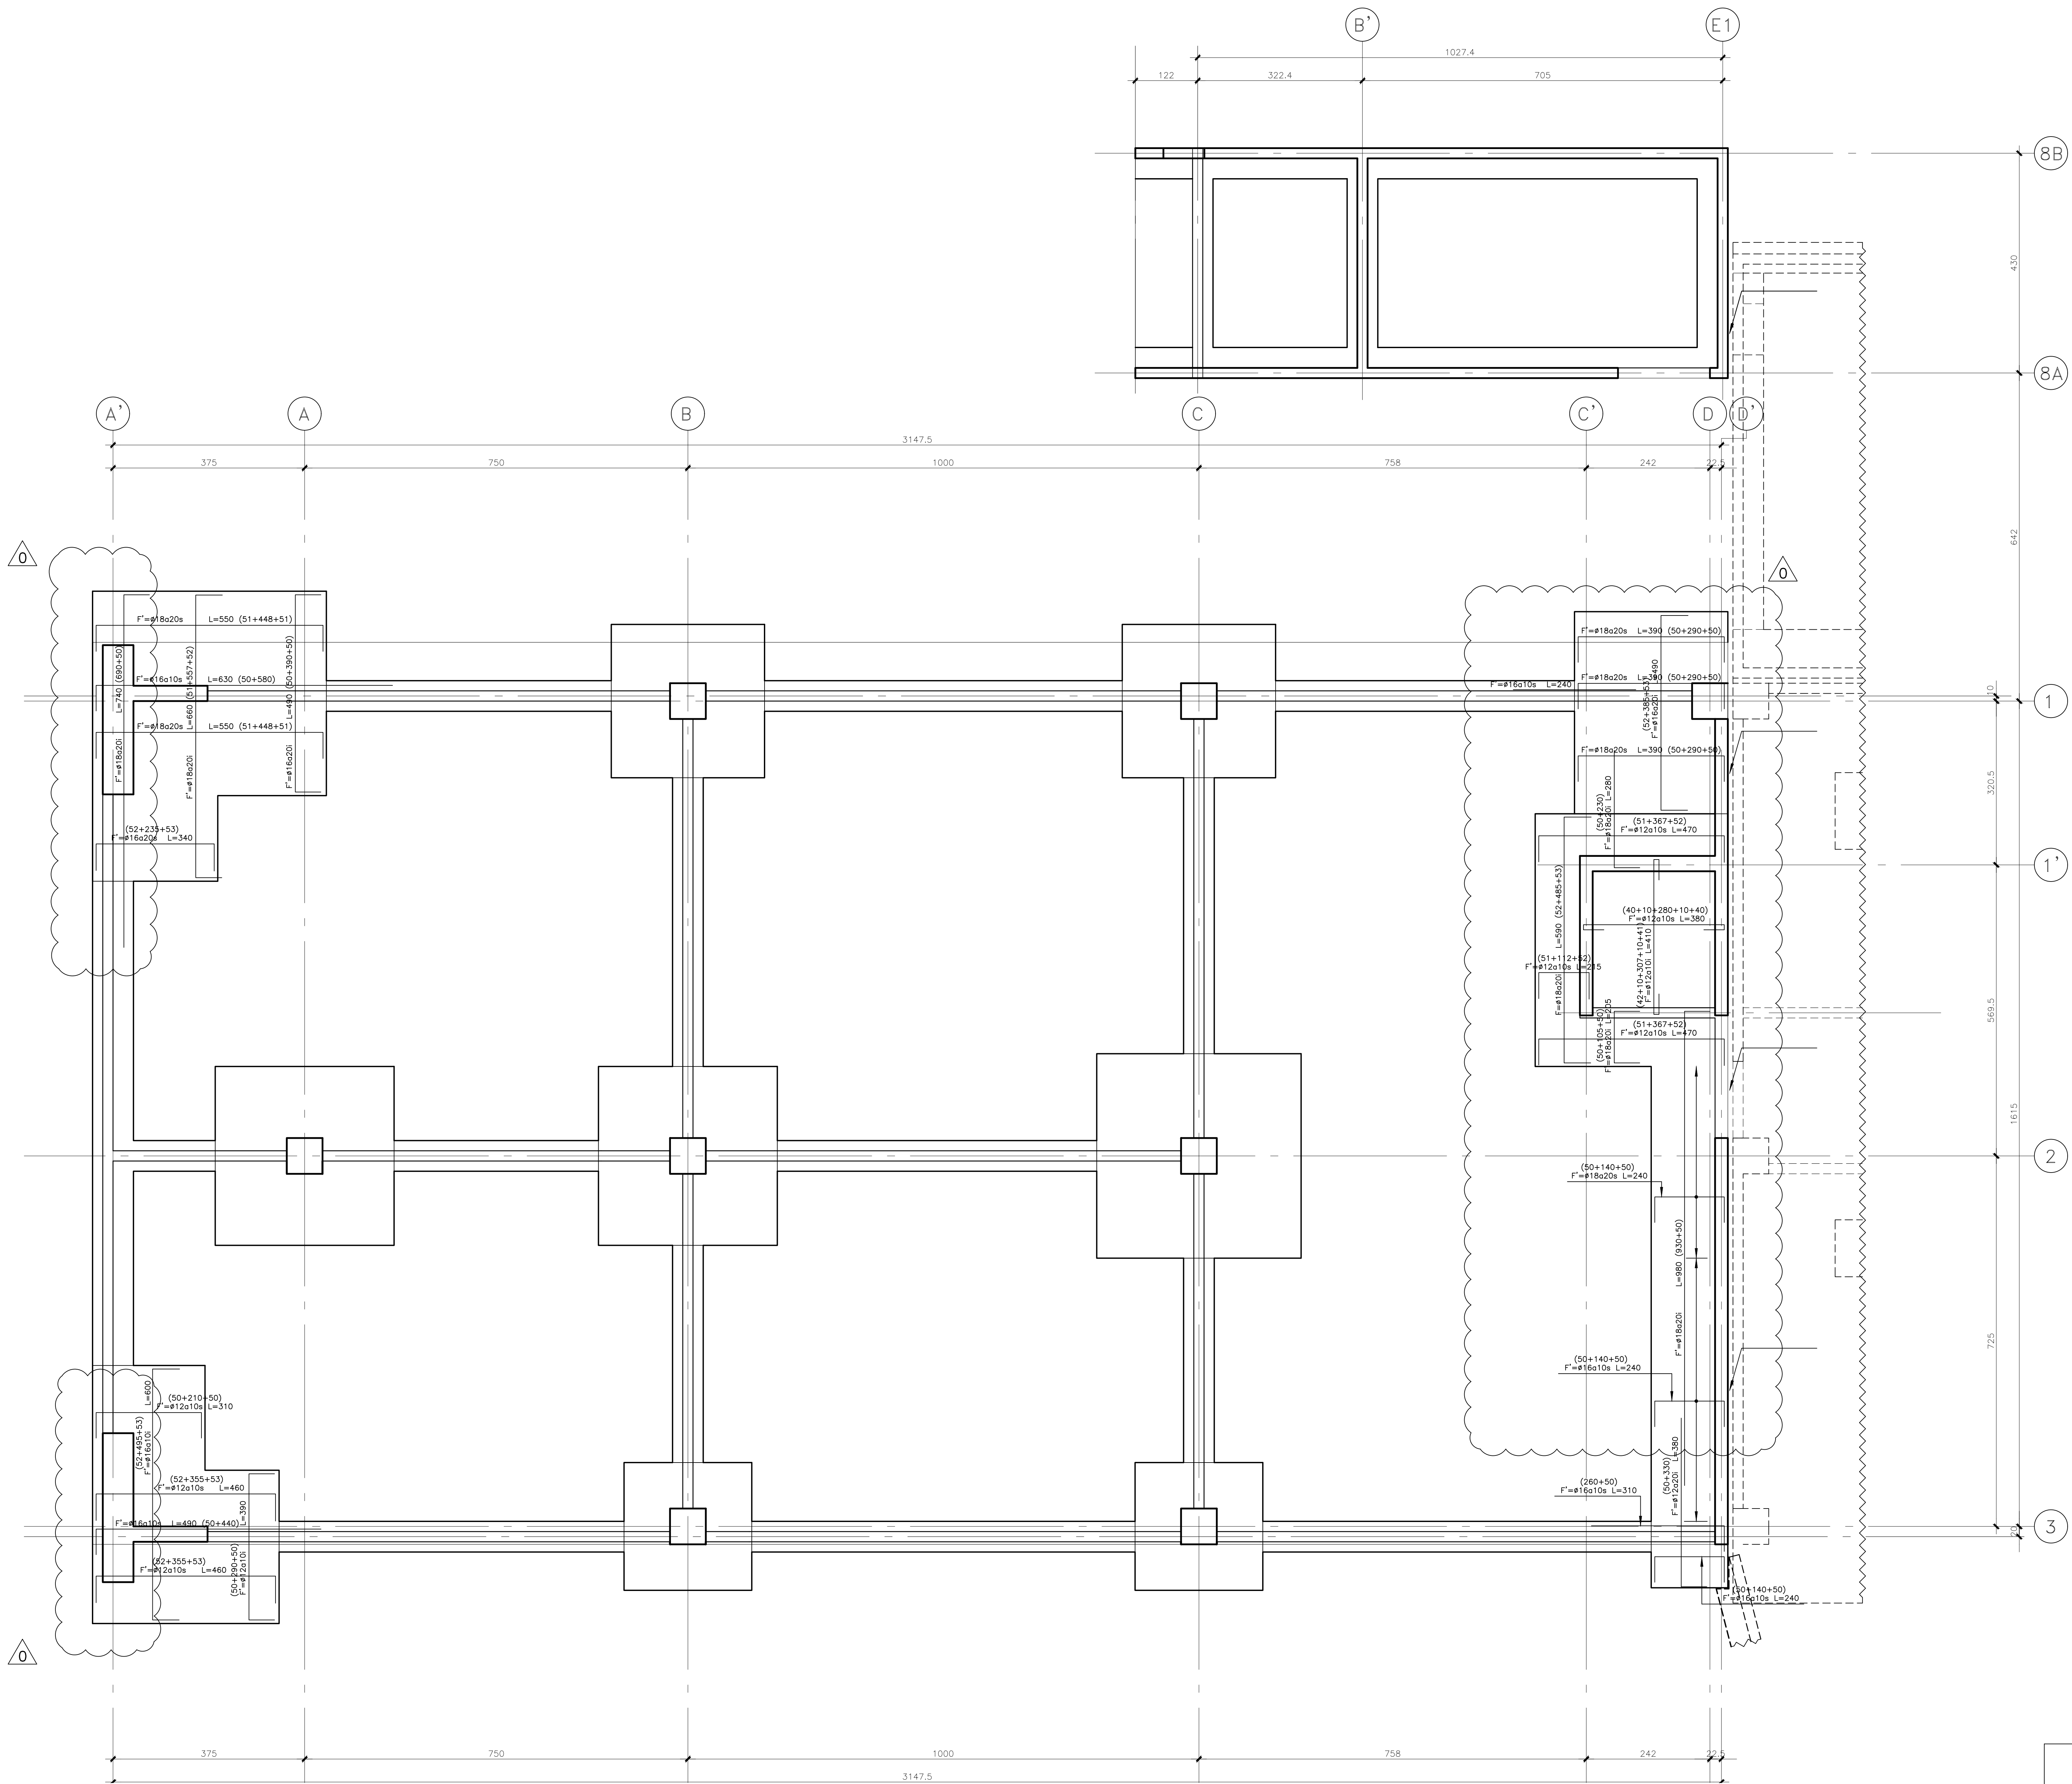

PLANTA ARMADURA SUPERIOR FUNDACIONES (F')

ESCALA 1:50

ESTADO:		APROBADO PARA:	
DESARROLLO	PRELIMINAR	PROPUESTA	CONSTRUCCION
REVISION		ING. / DIB. FECHA	

05/07/2011

FIRMA RE

ISO

FONO: +1
Info@re
www.re