

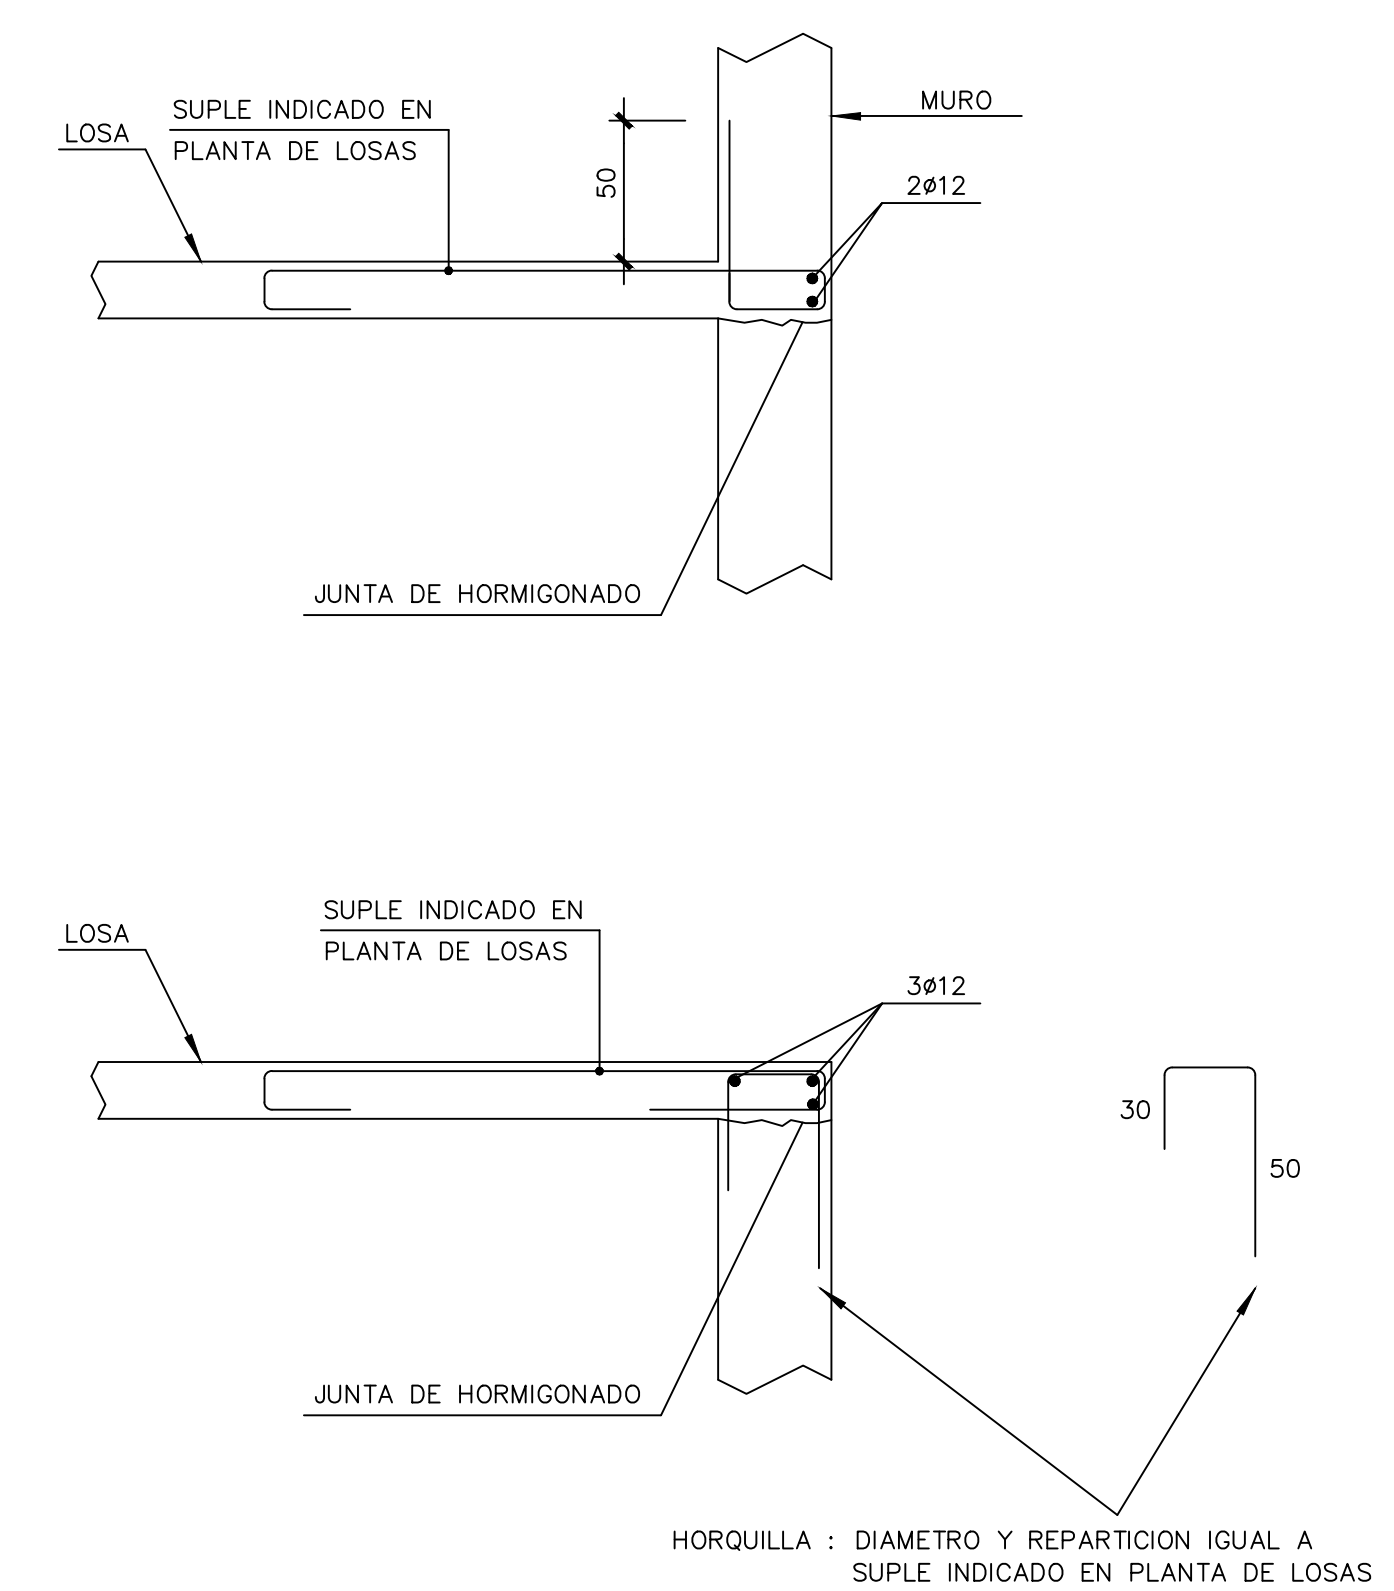


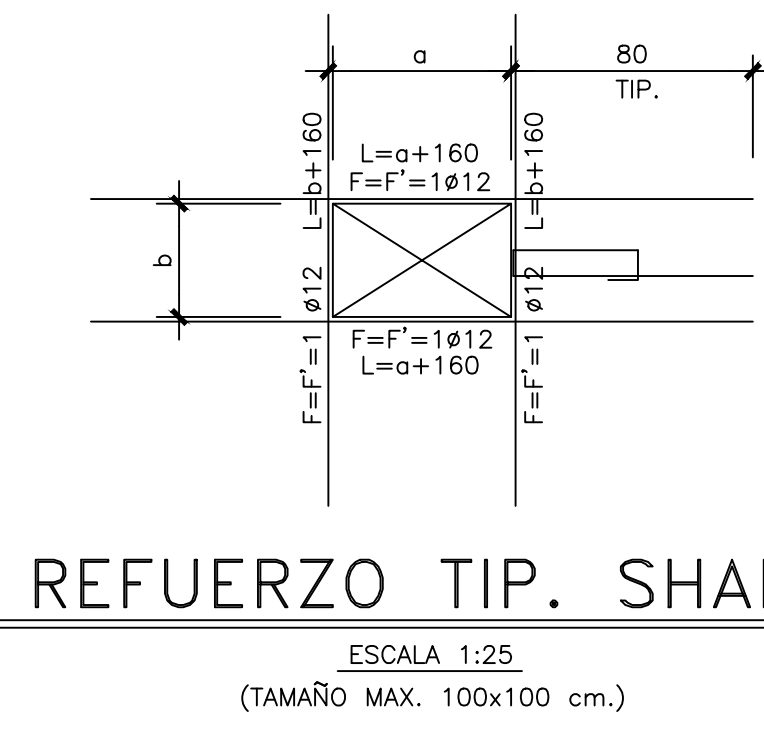

PLANTA ARMADURA SUPERIOR CIELO 1ºSUBTERRANEO a CIELO PISO 3º (F')
ESCALA 1:50

ESTADO:		APROBADO PARA:	
EN DESARROLLO	PRELIMINAR	PROPUESTA	CONSTRUCCION X
REVISION	ING. / DIB.	FECHA	
0	SE EMITE PARA CONSTRUCCION	MRC/ARB	24/10/2024

FIRMA REVISOR INDEPENDIENTE CALCULO		FIRMA INC. RESPONSABLE	

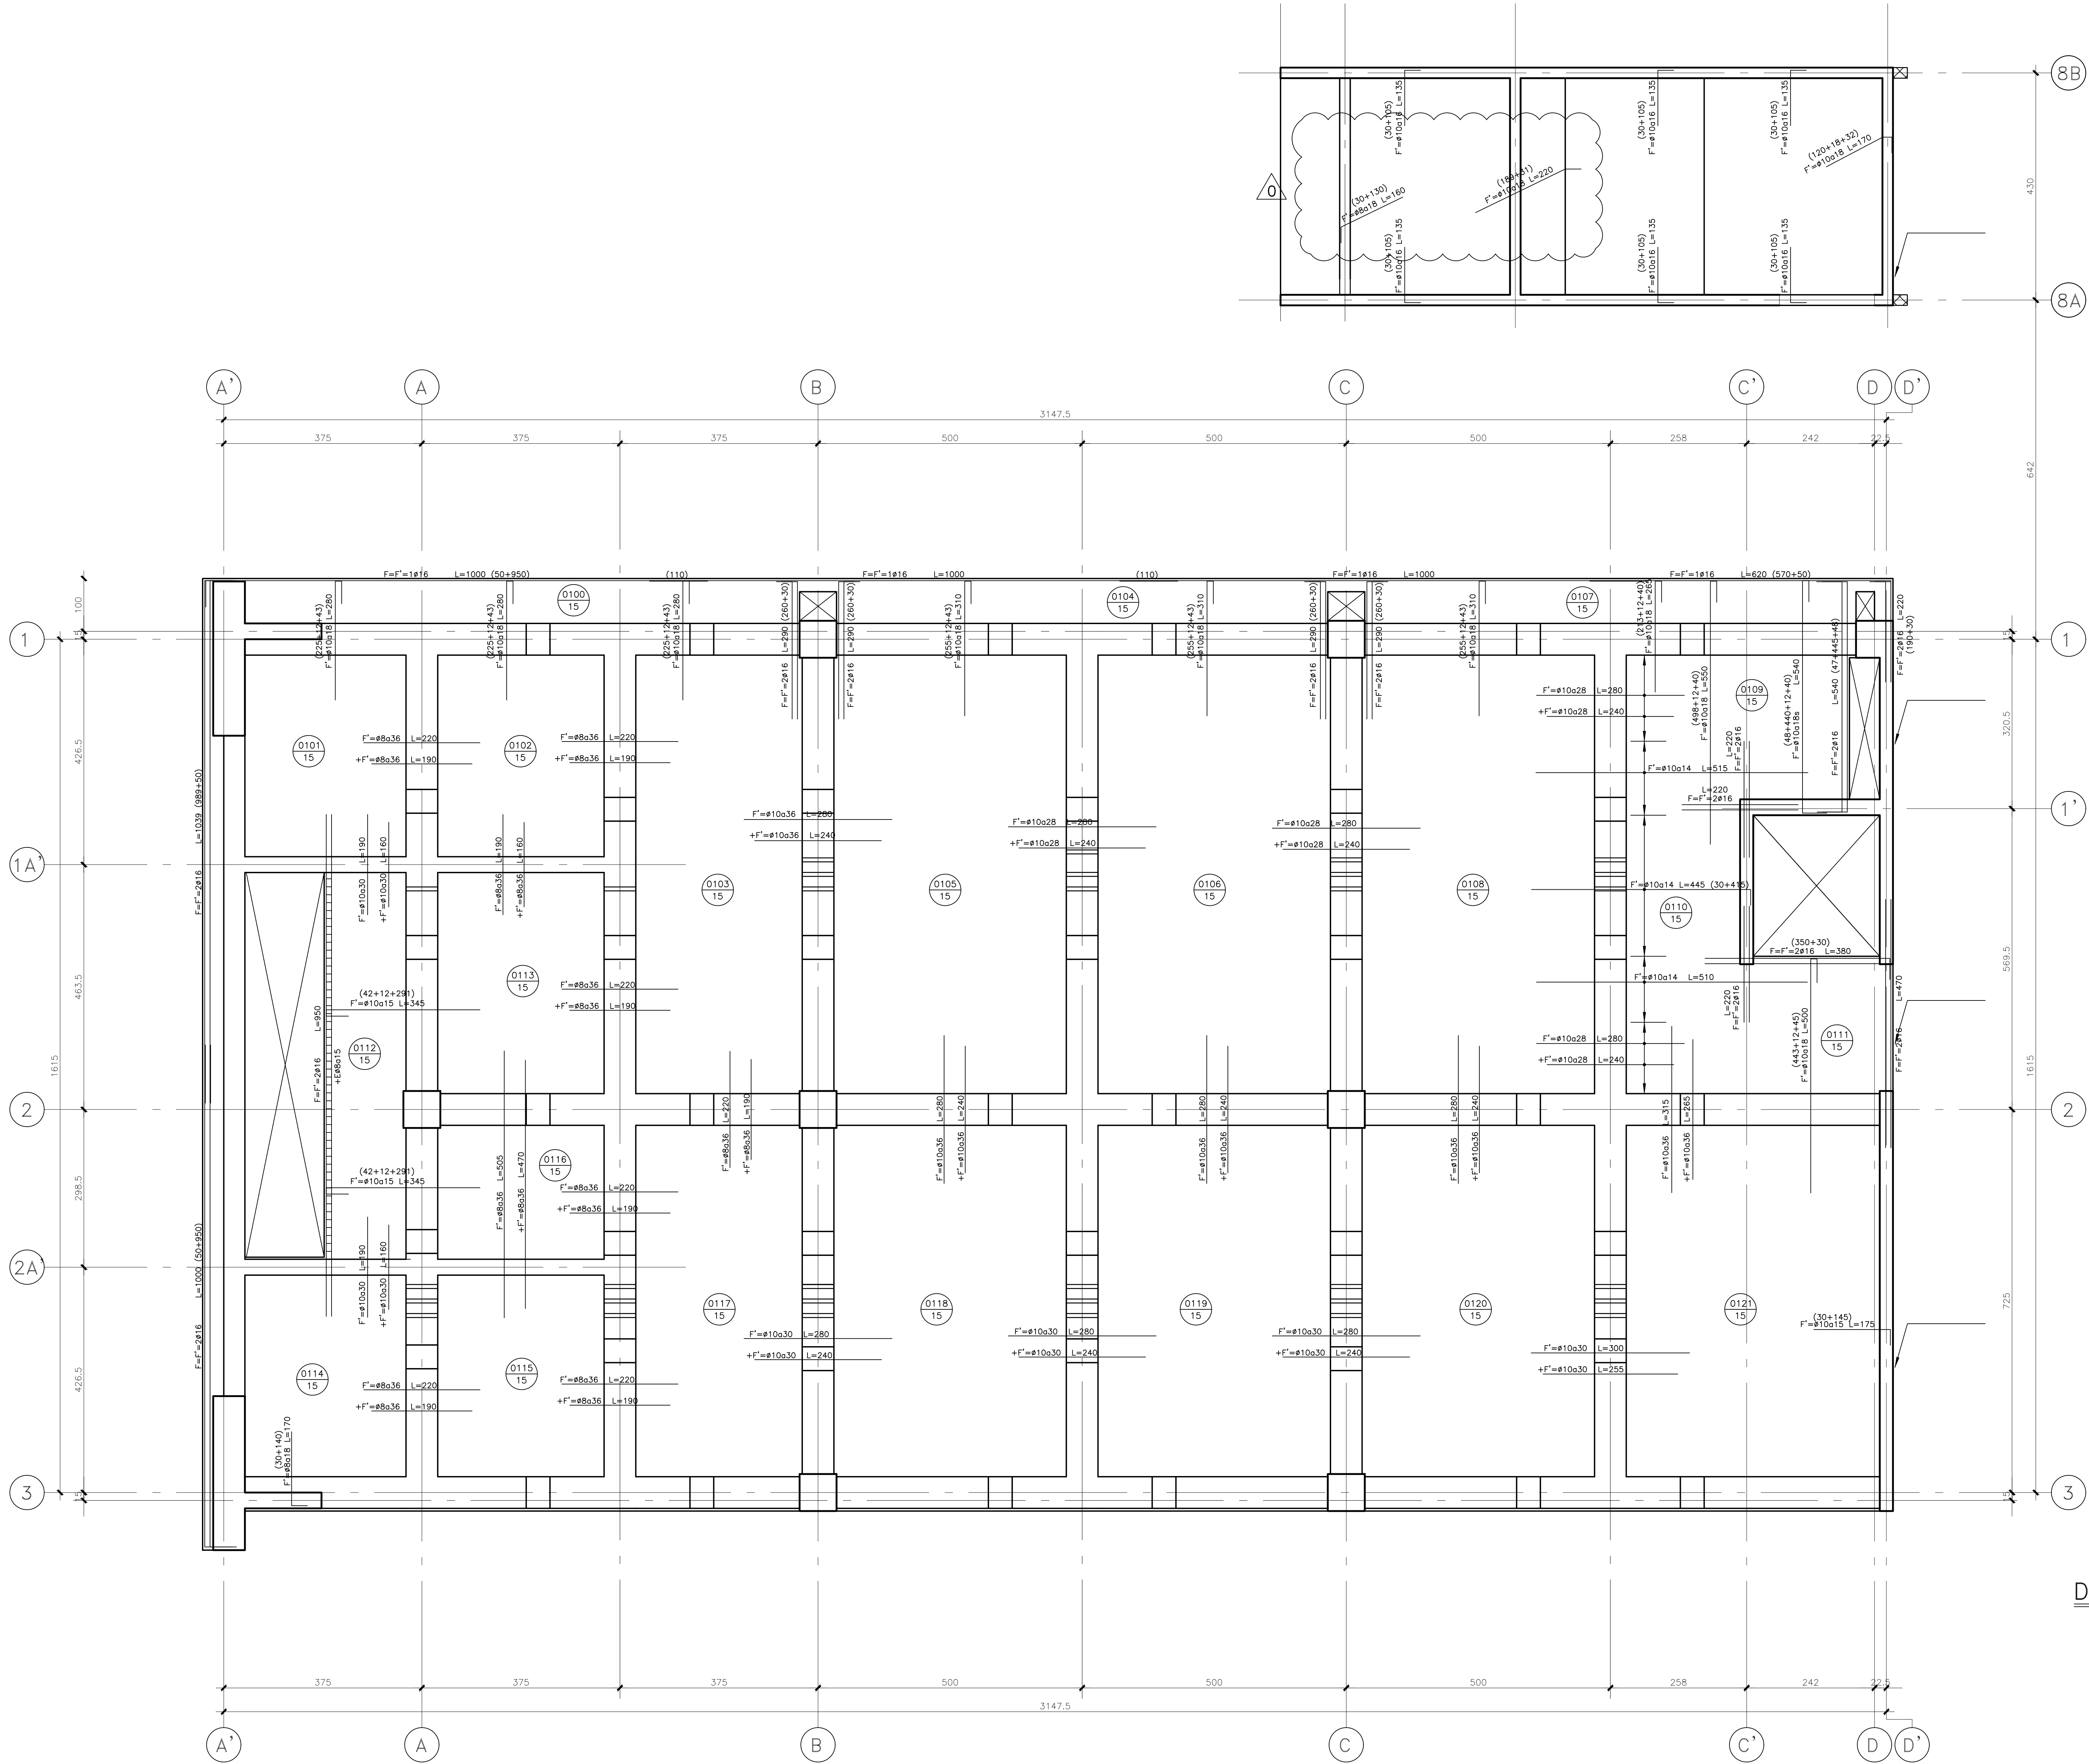

FONO: +56 2 25941300
info@renelagos.com
www.renelagos.com

renelagos
engineers



PROYECTO	U. DE LOS ANDES (FASE 2)
CONTENIDO	PLANTA ARMADURA SUPERIOR CIELO 1ºSUBTERRANEO a CIELO PISO 3º (F')

REVISOR: MARCELO CONTRERAS
DISEÑADOR: MARCELO CONTRERAS
DISEÑADOR: MARCELO CONTRERAS
DISEÑADOR: MARCELO CONTRERAS

24/10/2024