
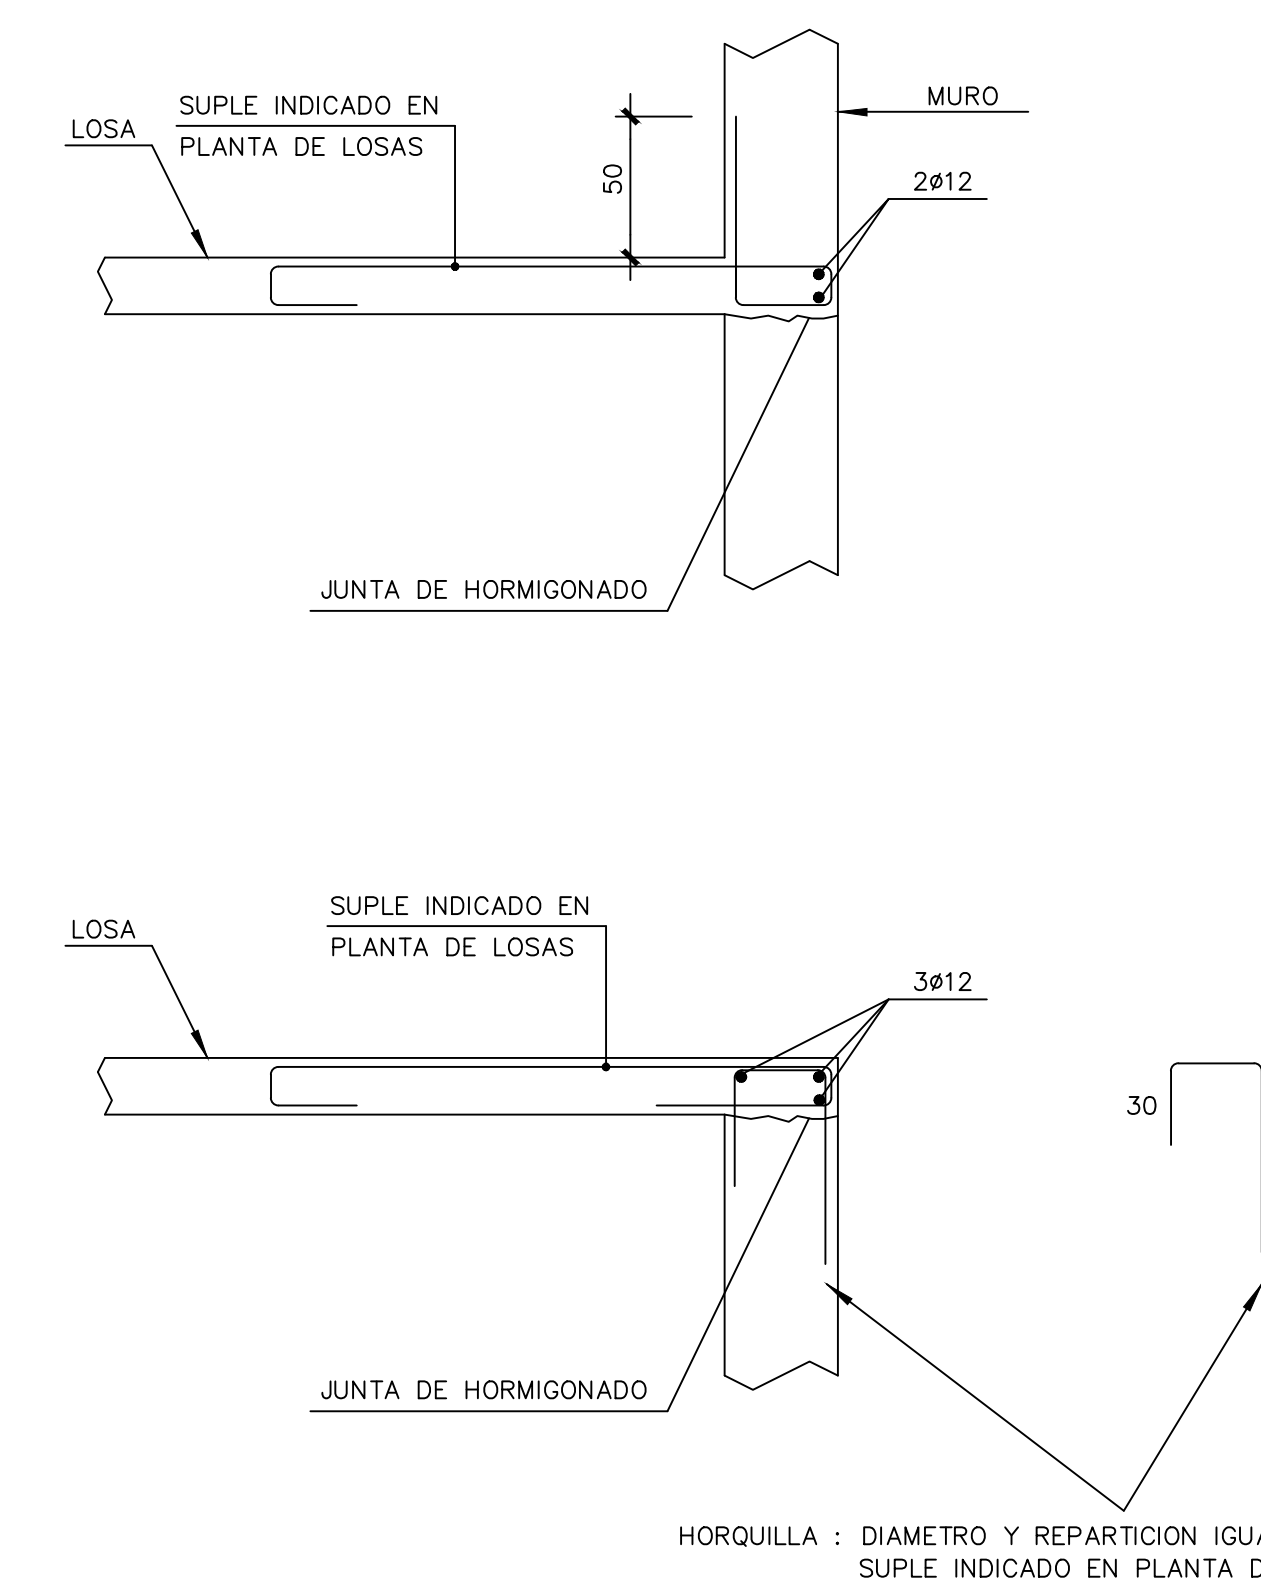
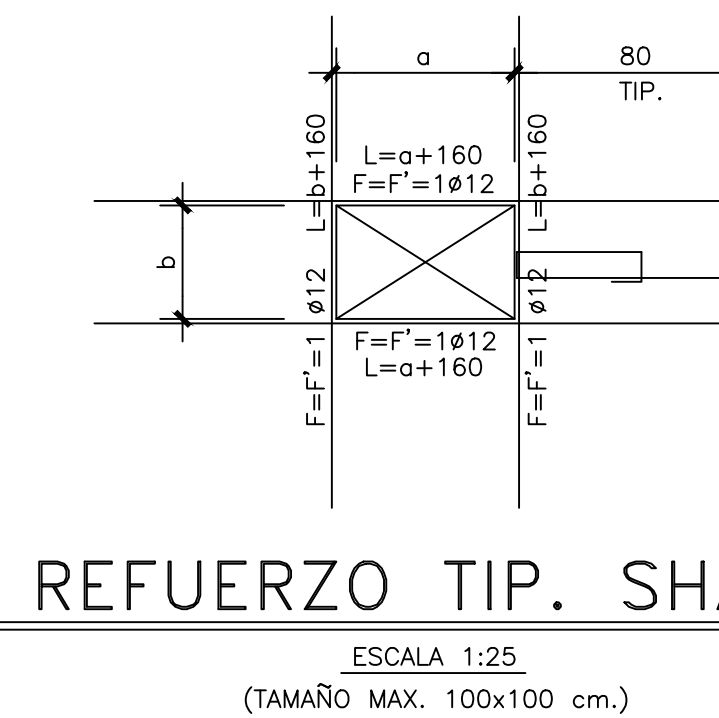


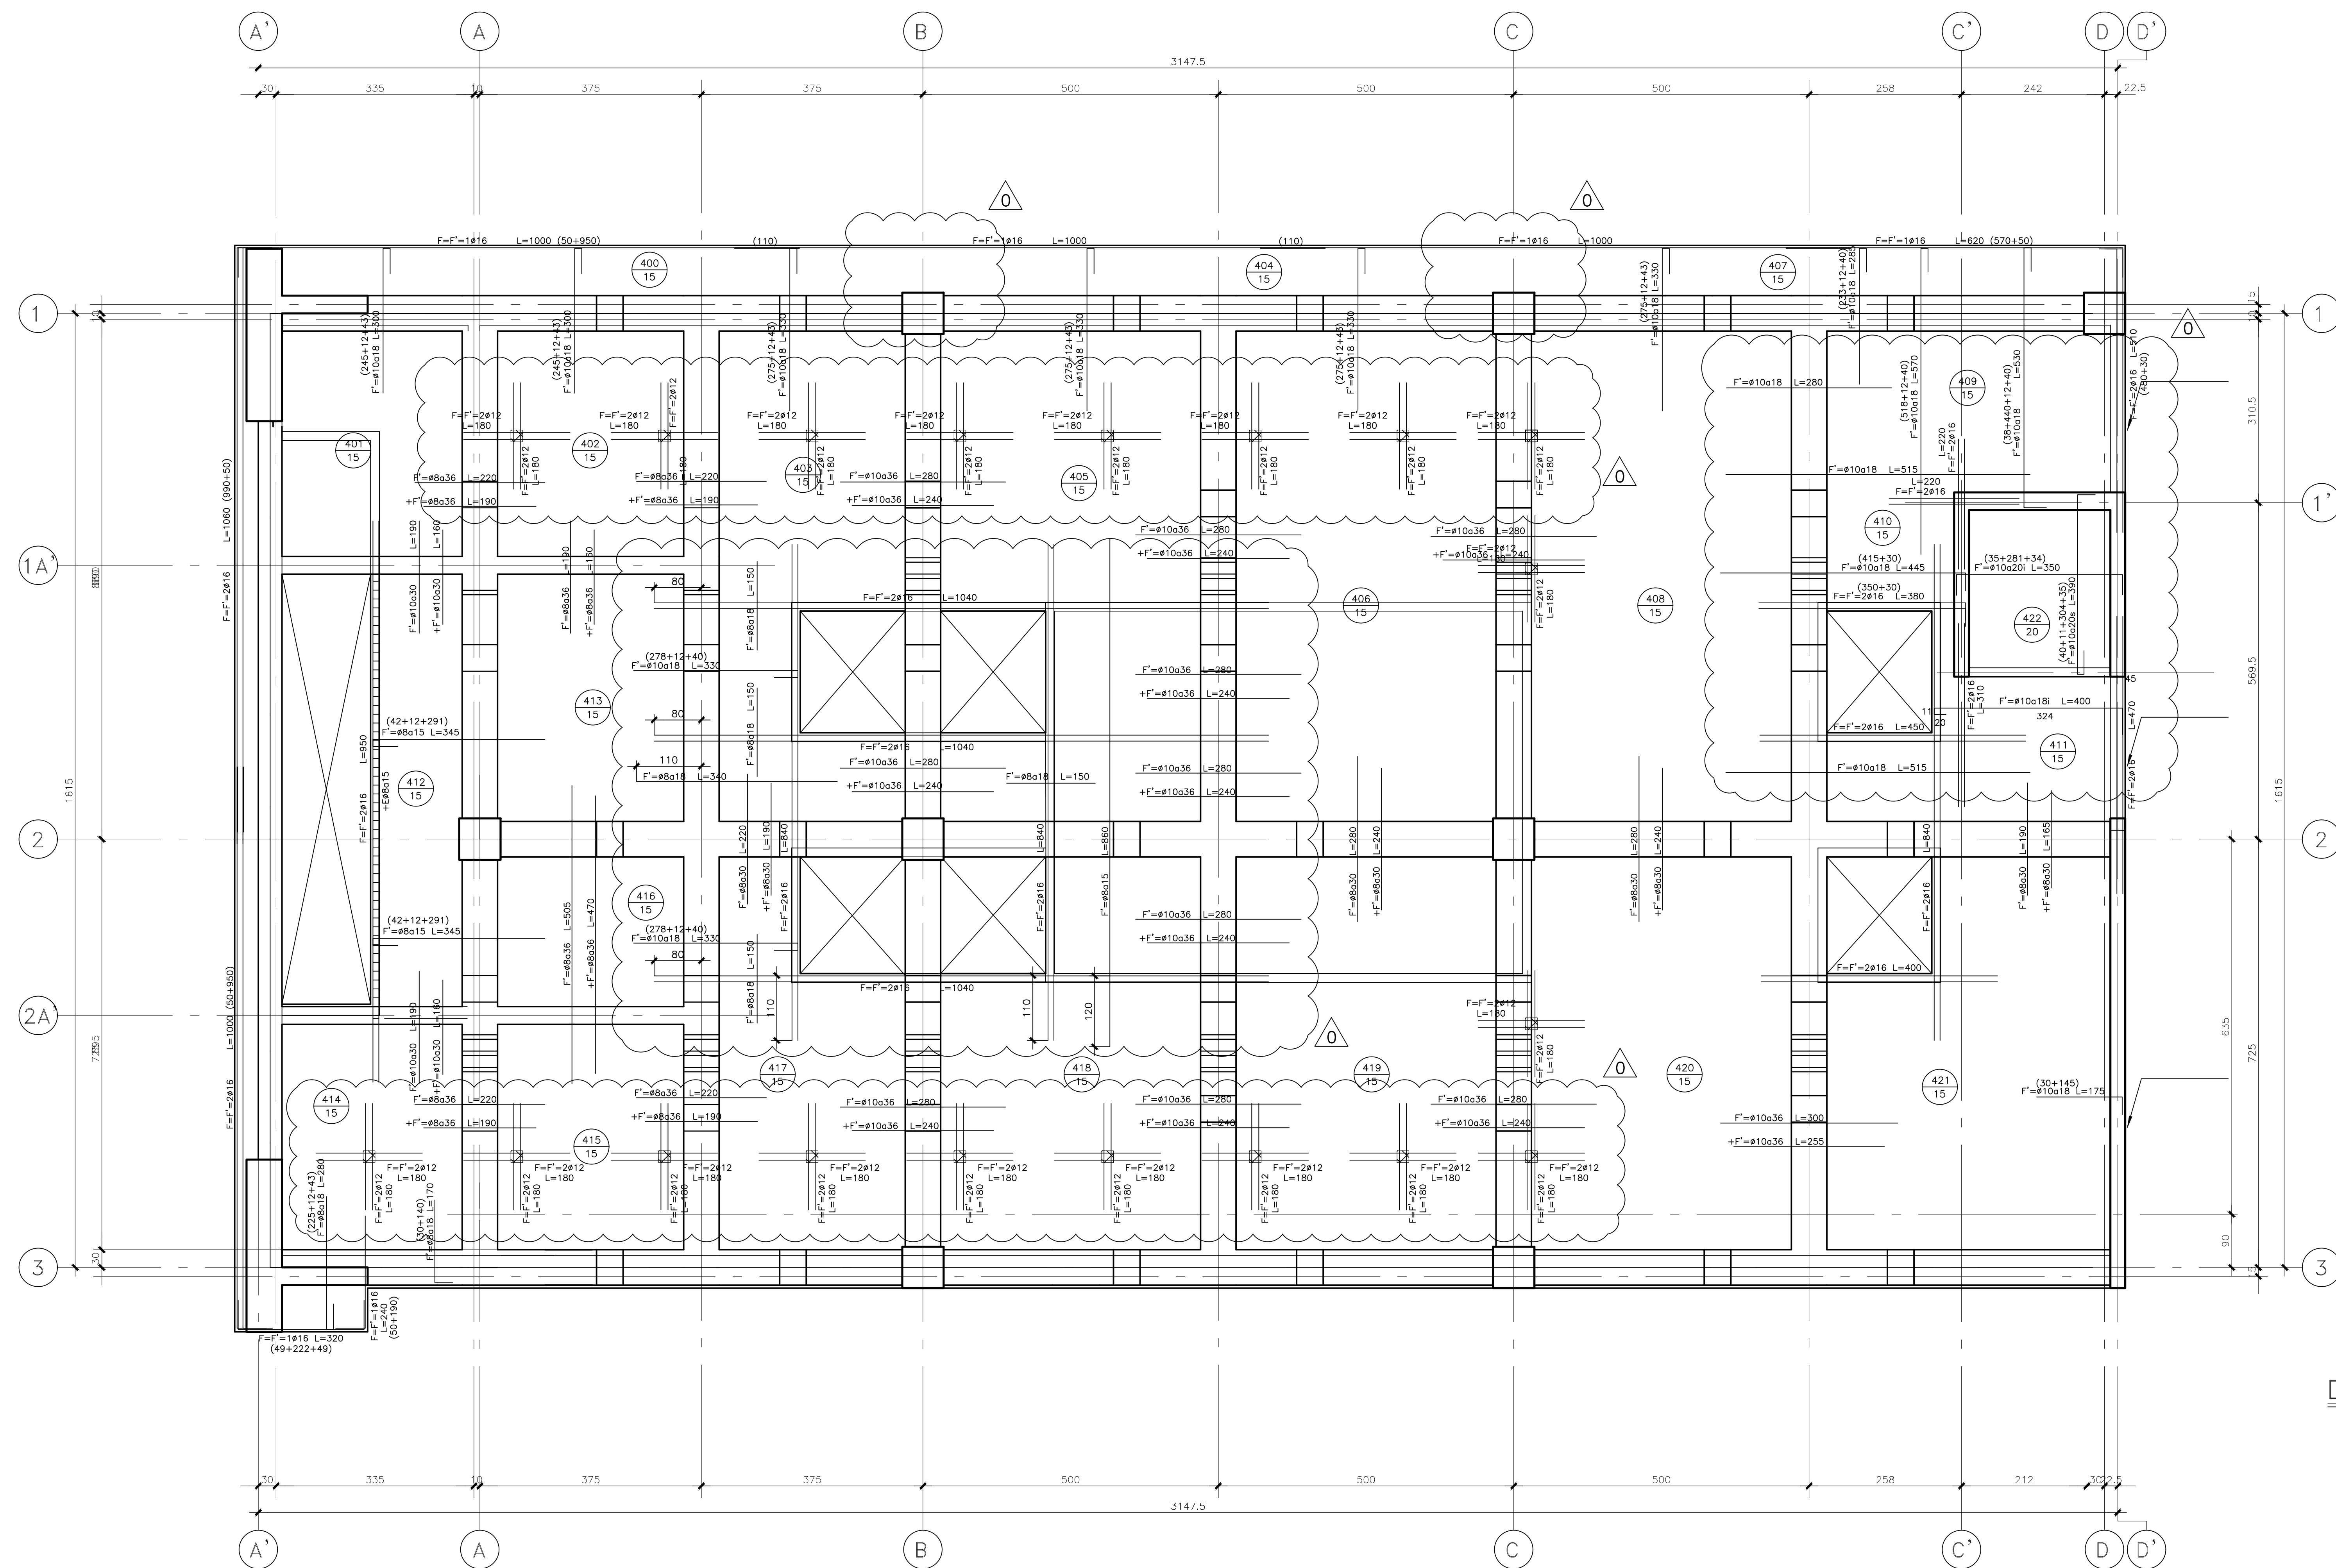

PLANTA ARMADURA SUPERIOR CIELO PISO 4° (F')

ESCALA 1:20