



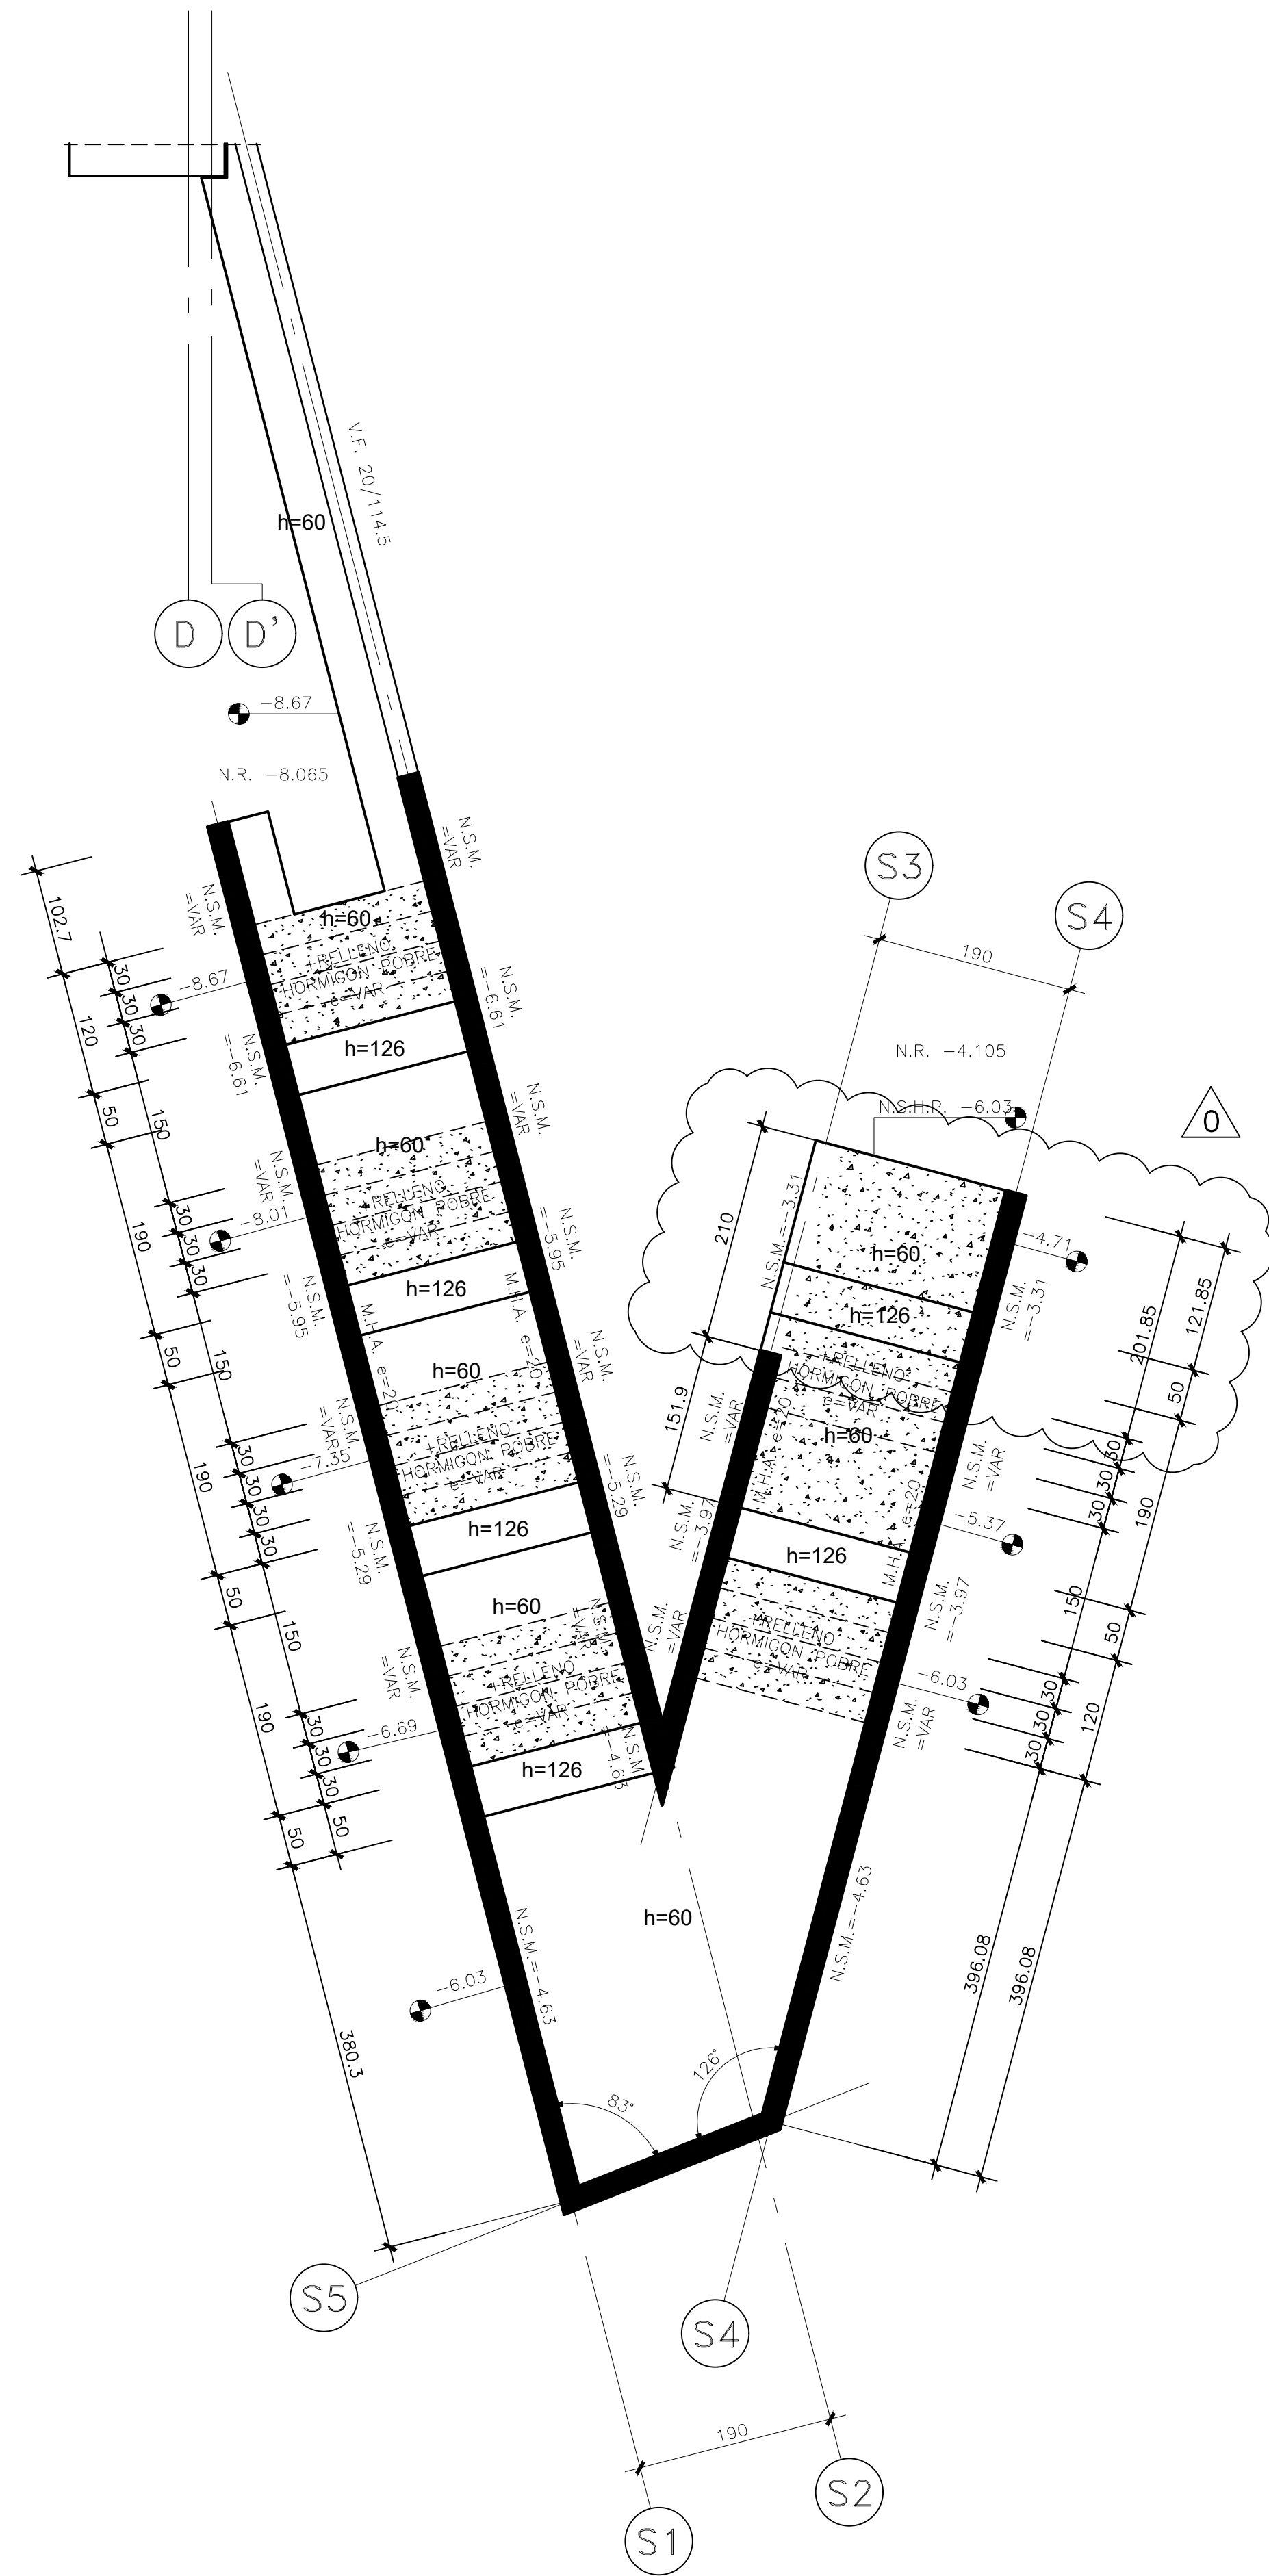


PLANTA ESCALERA 03 EXTERIOR SUR
DESDE NIVEL -8.065 al -4.105

ESCALA 1:50

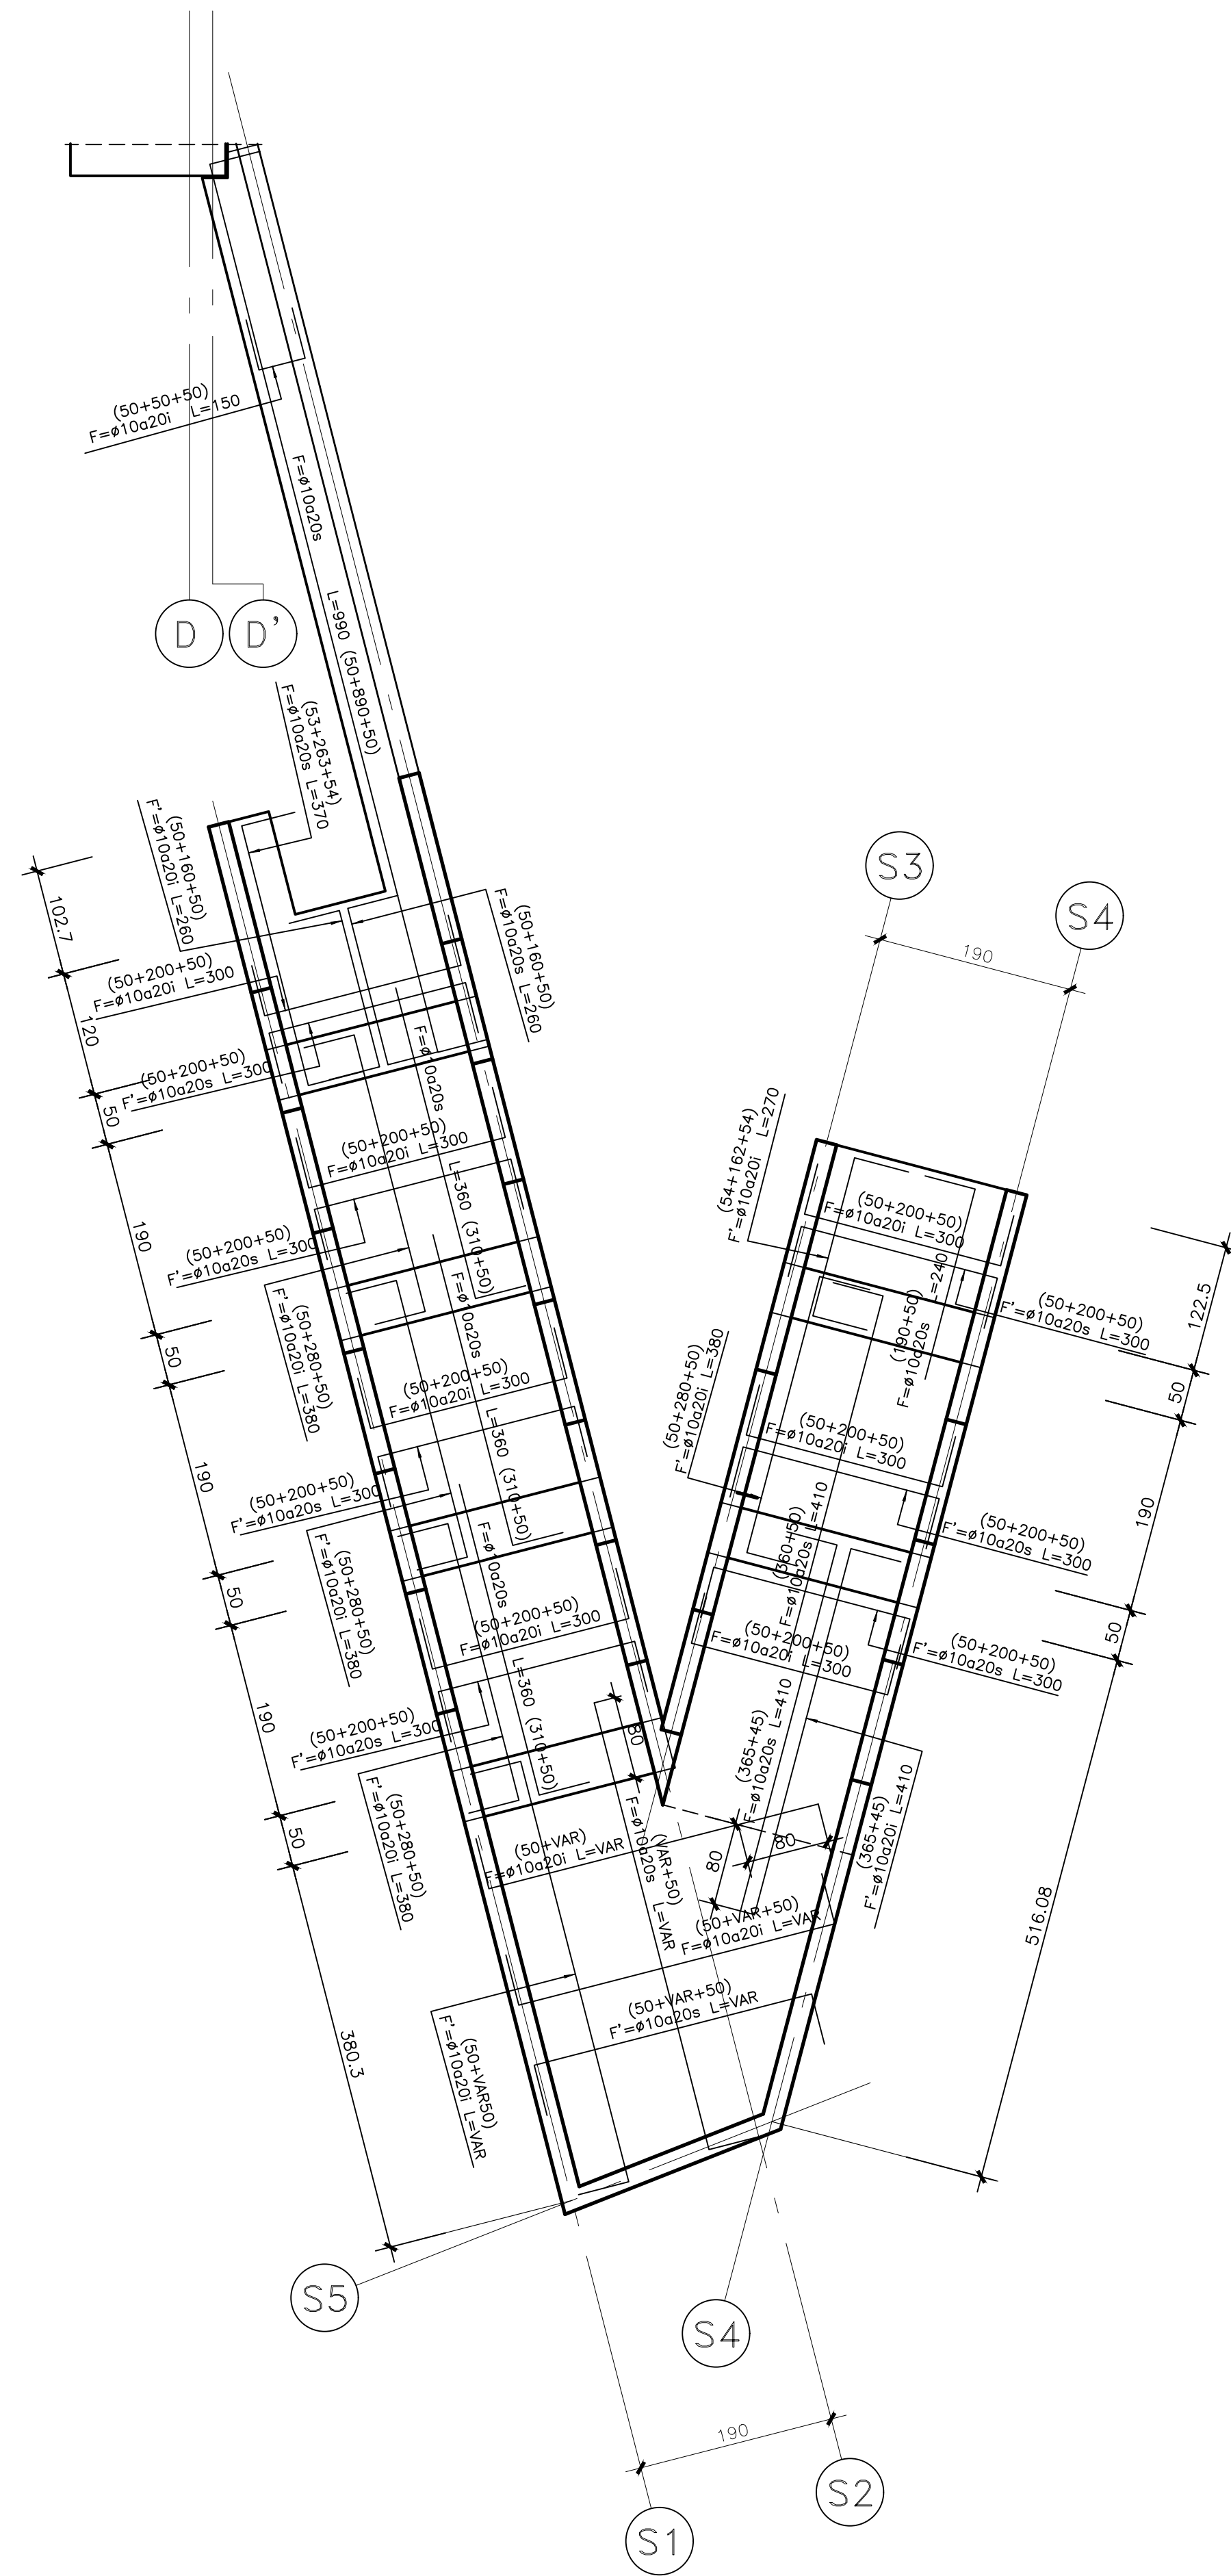


PLANTA ARMADURA DE FUDACION
ESCALERA 03 EXTERIOR SUR

ESCALA 1:50

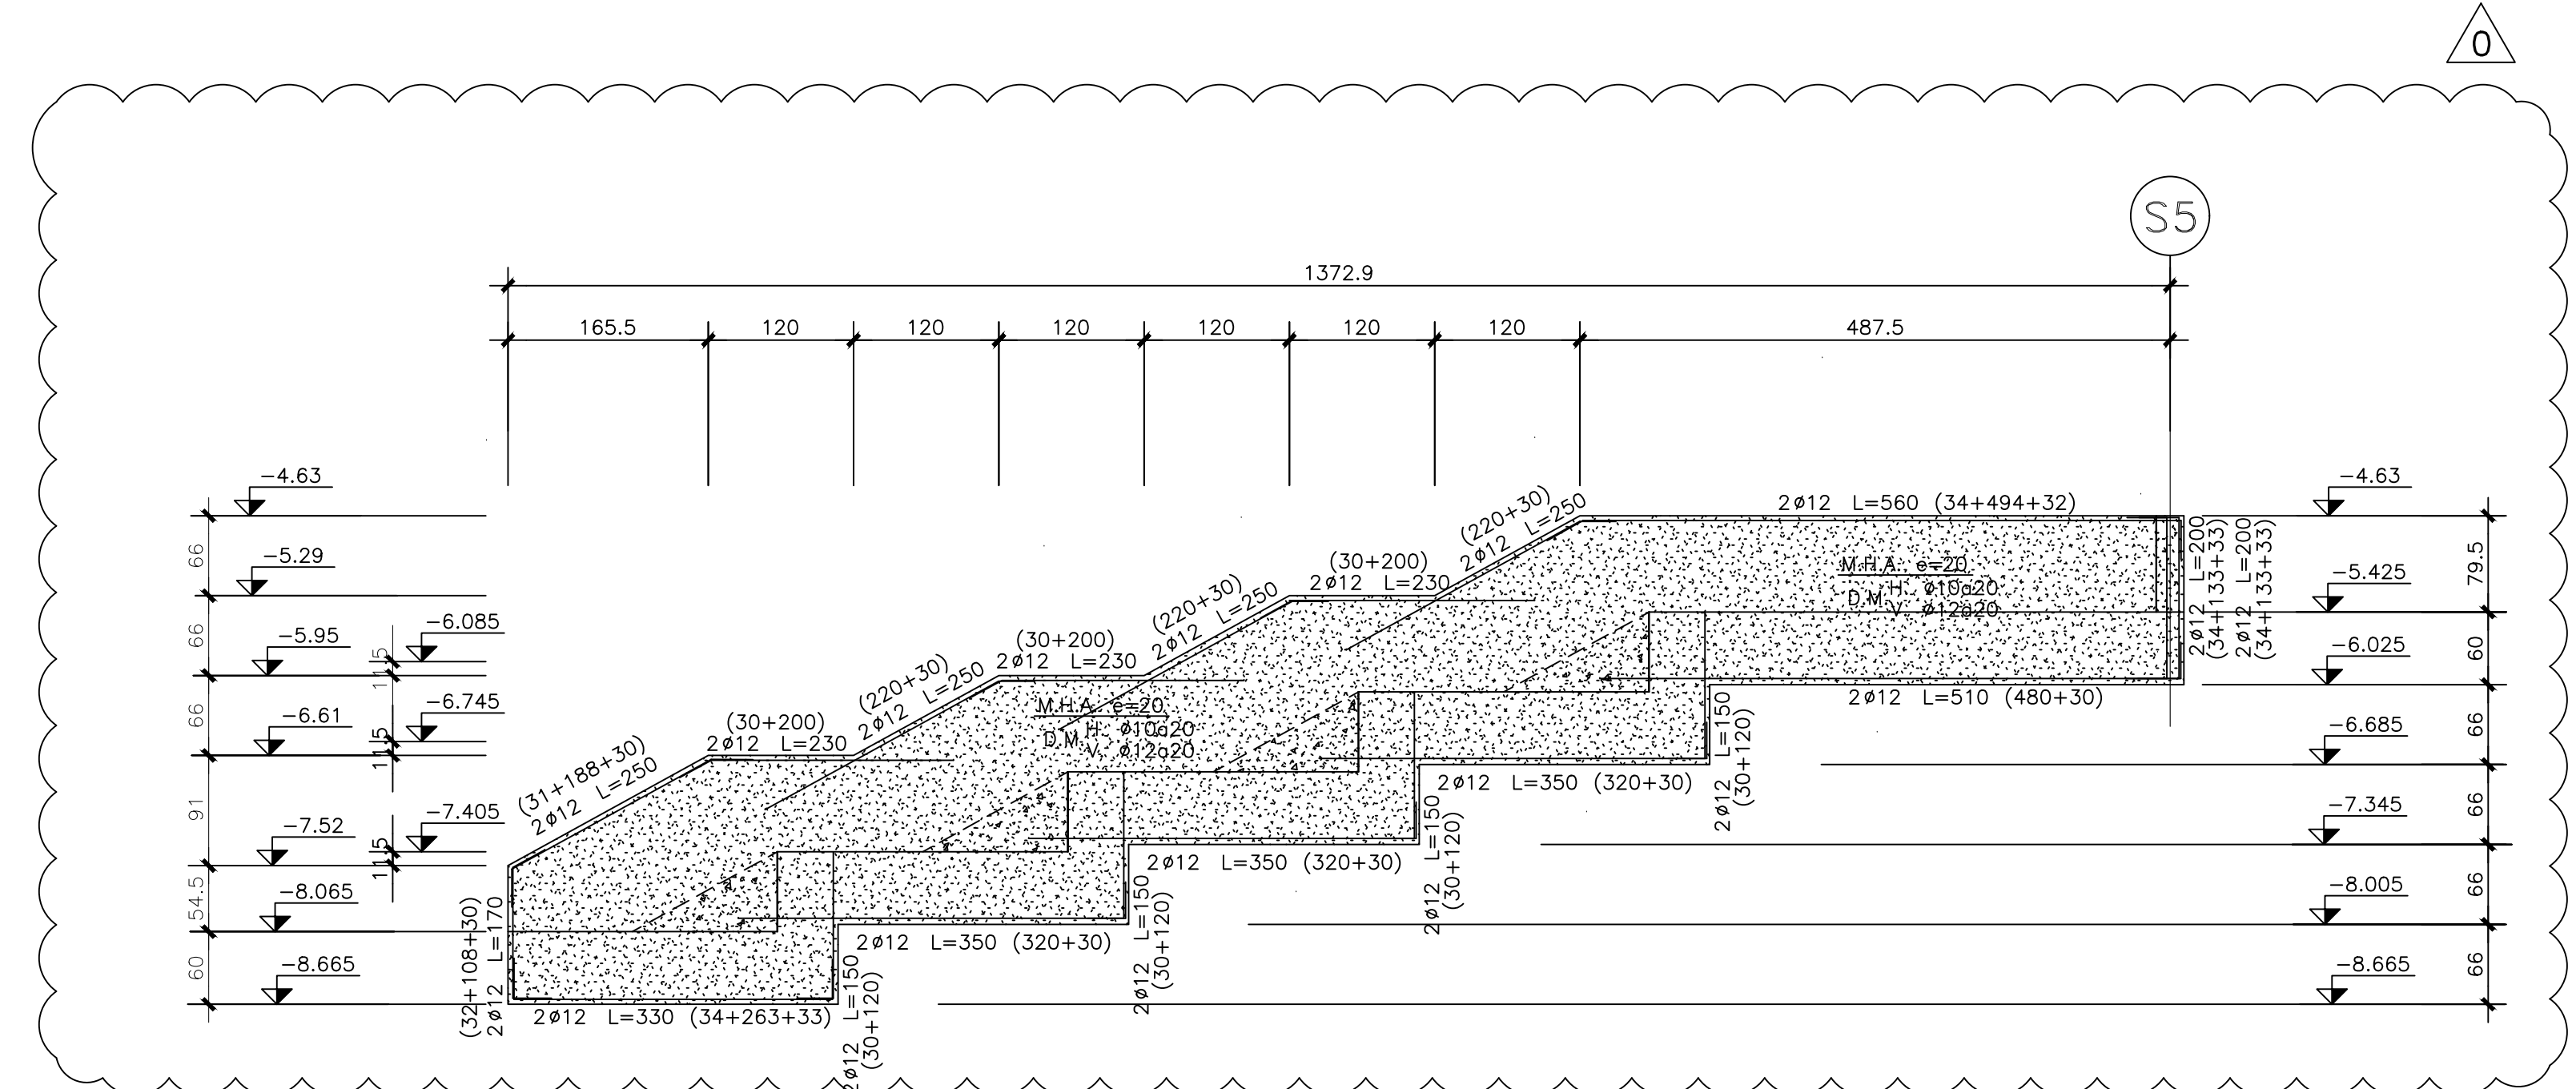


ELEVACION EJE S1

ESCALA 1:50

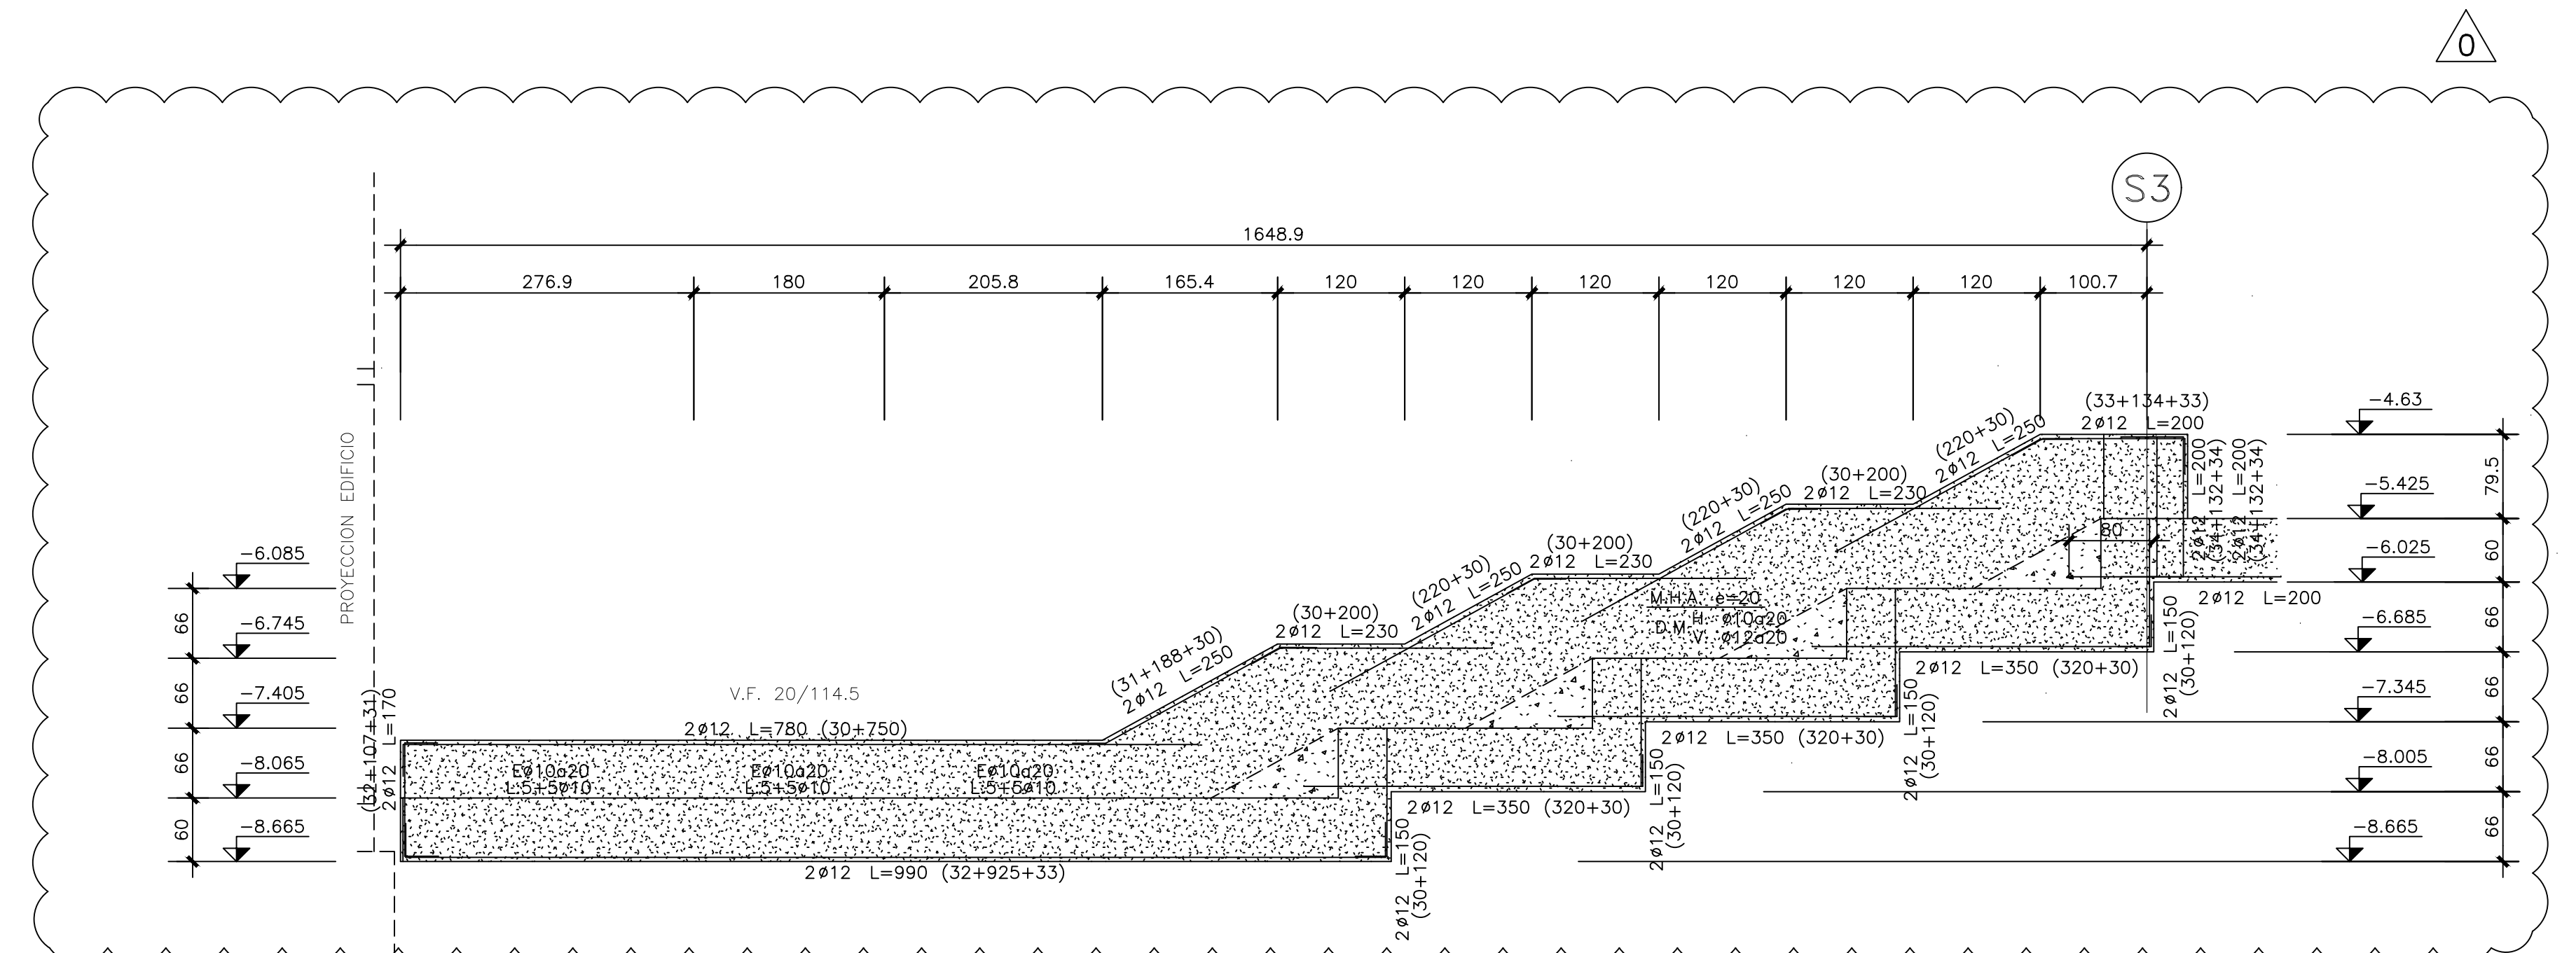


ELEVACION EJE S2

ESCALA 1:50

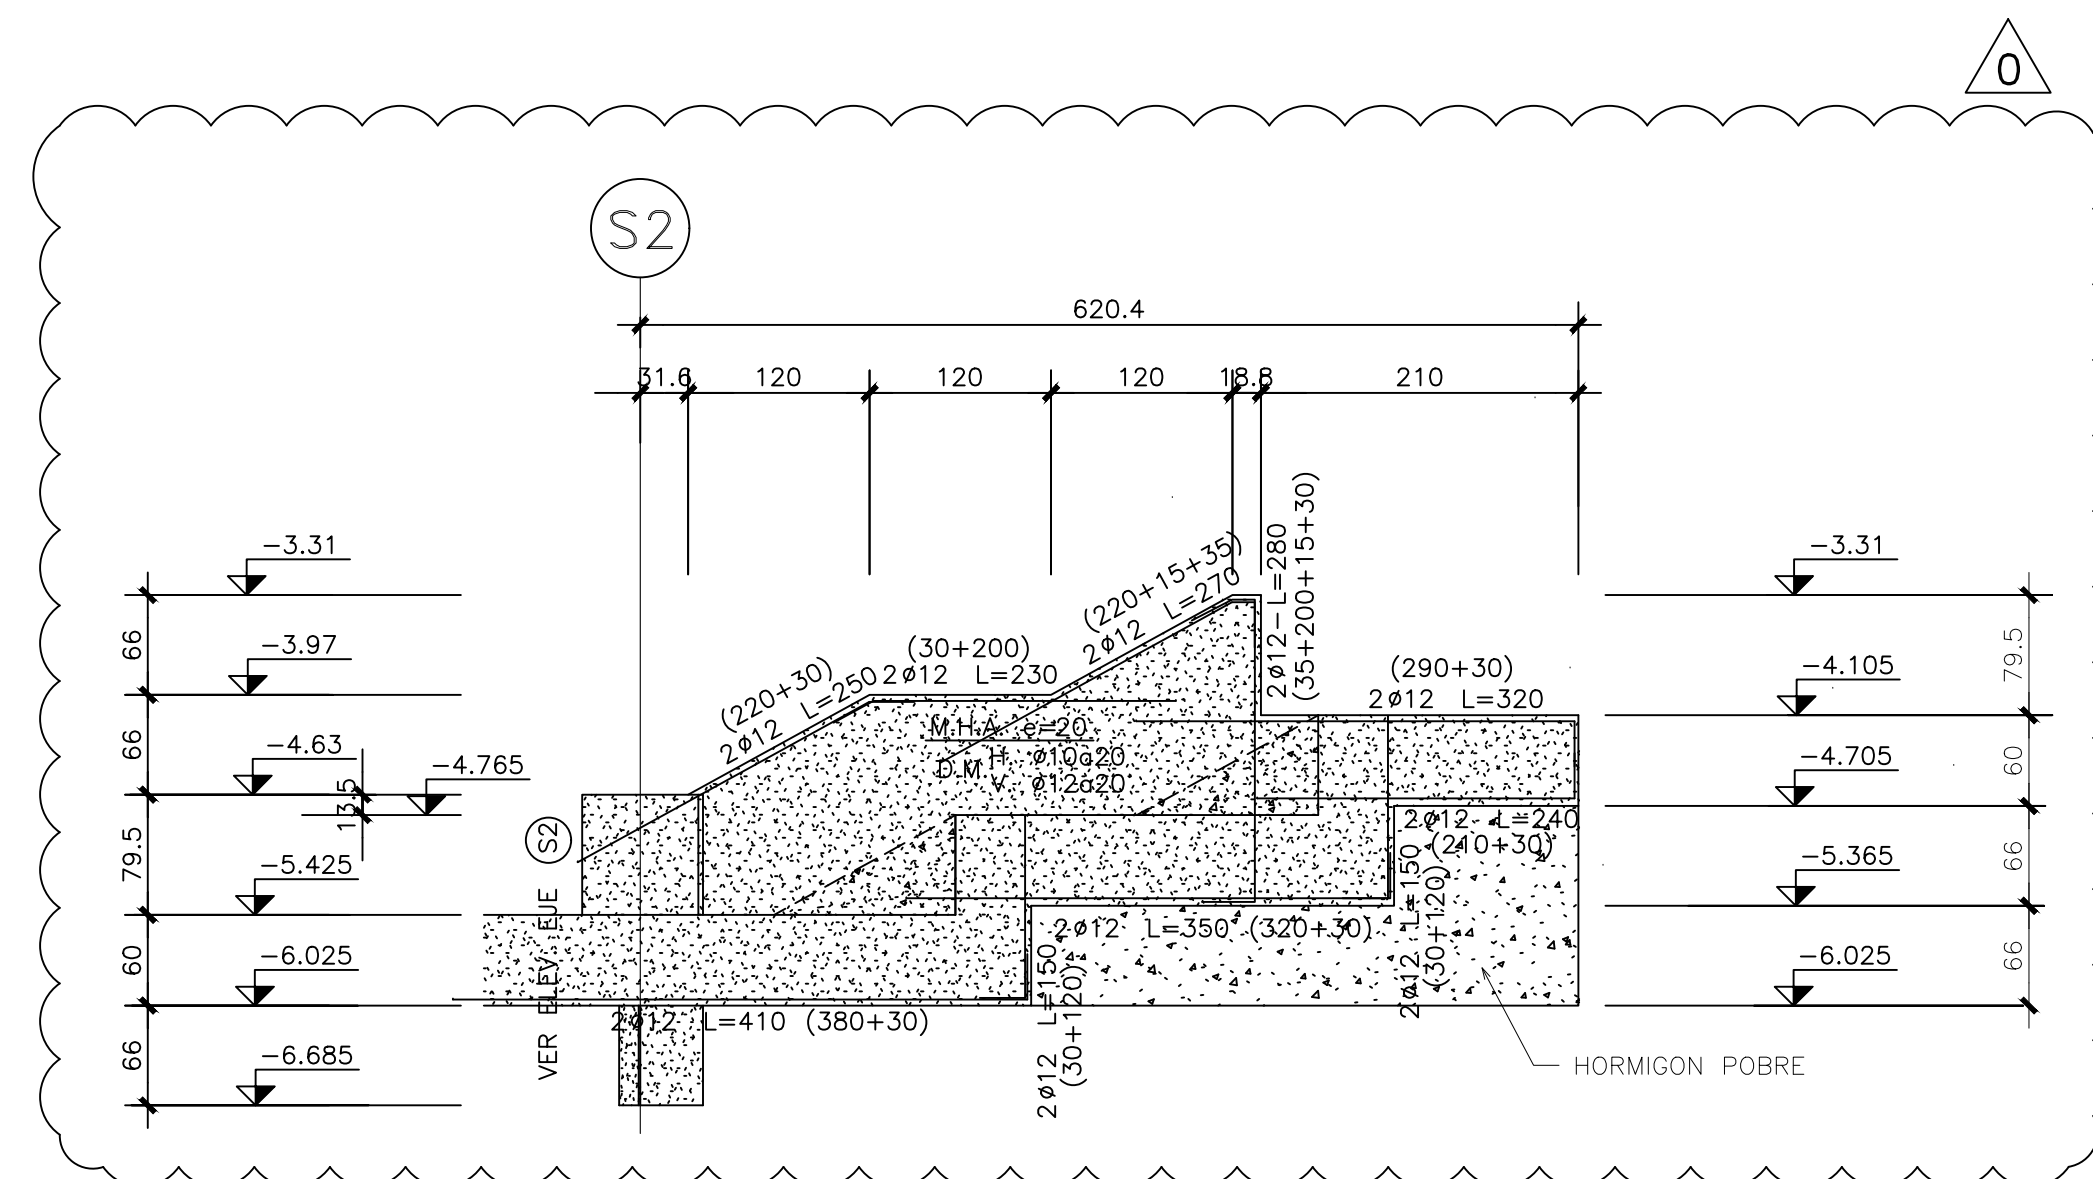


ELEVACION EJE S3

ESCALA 1:50

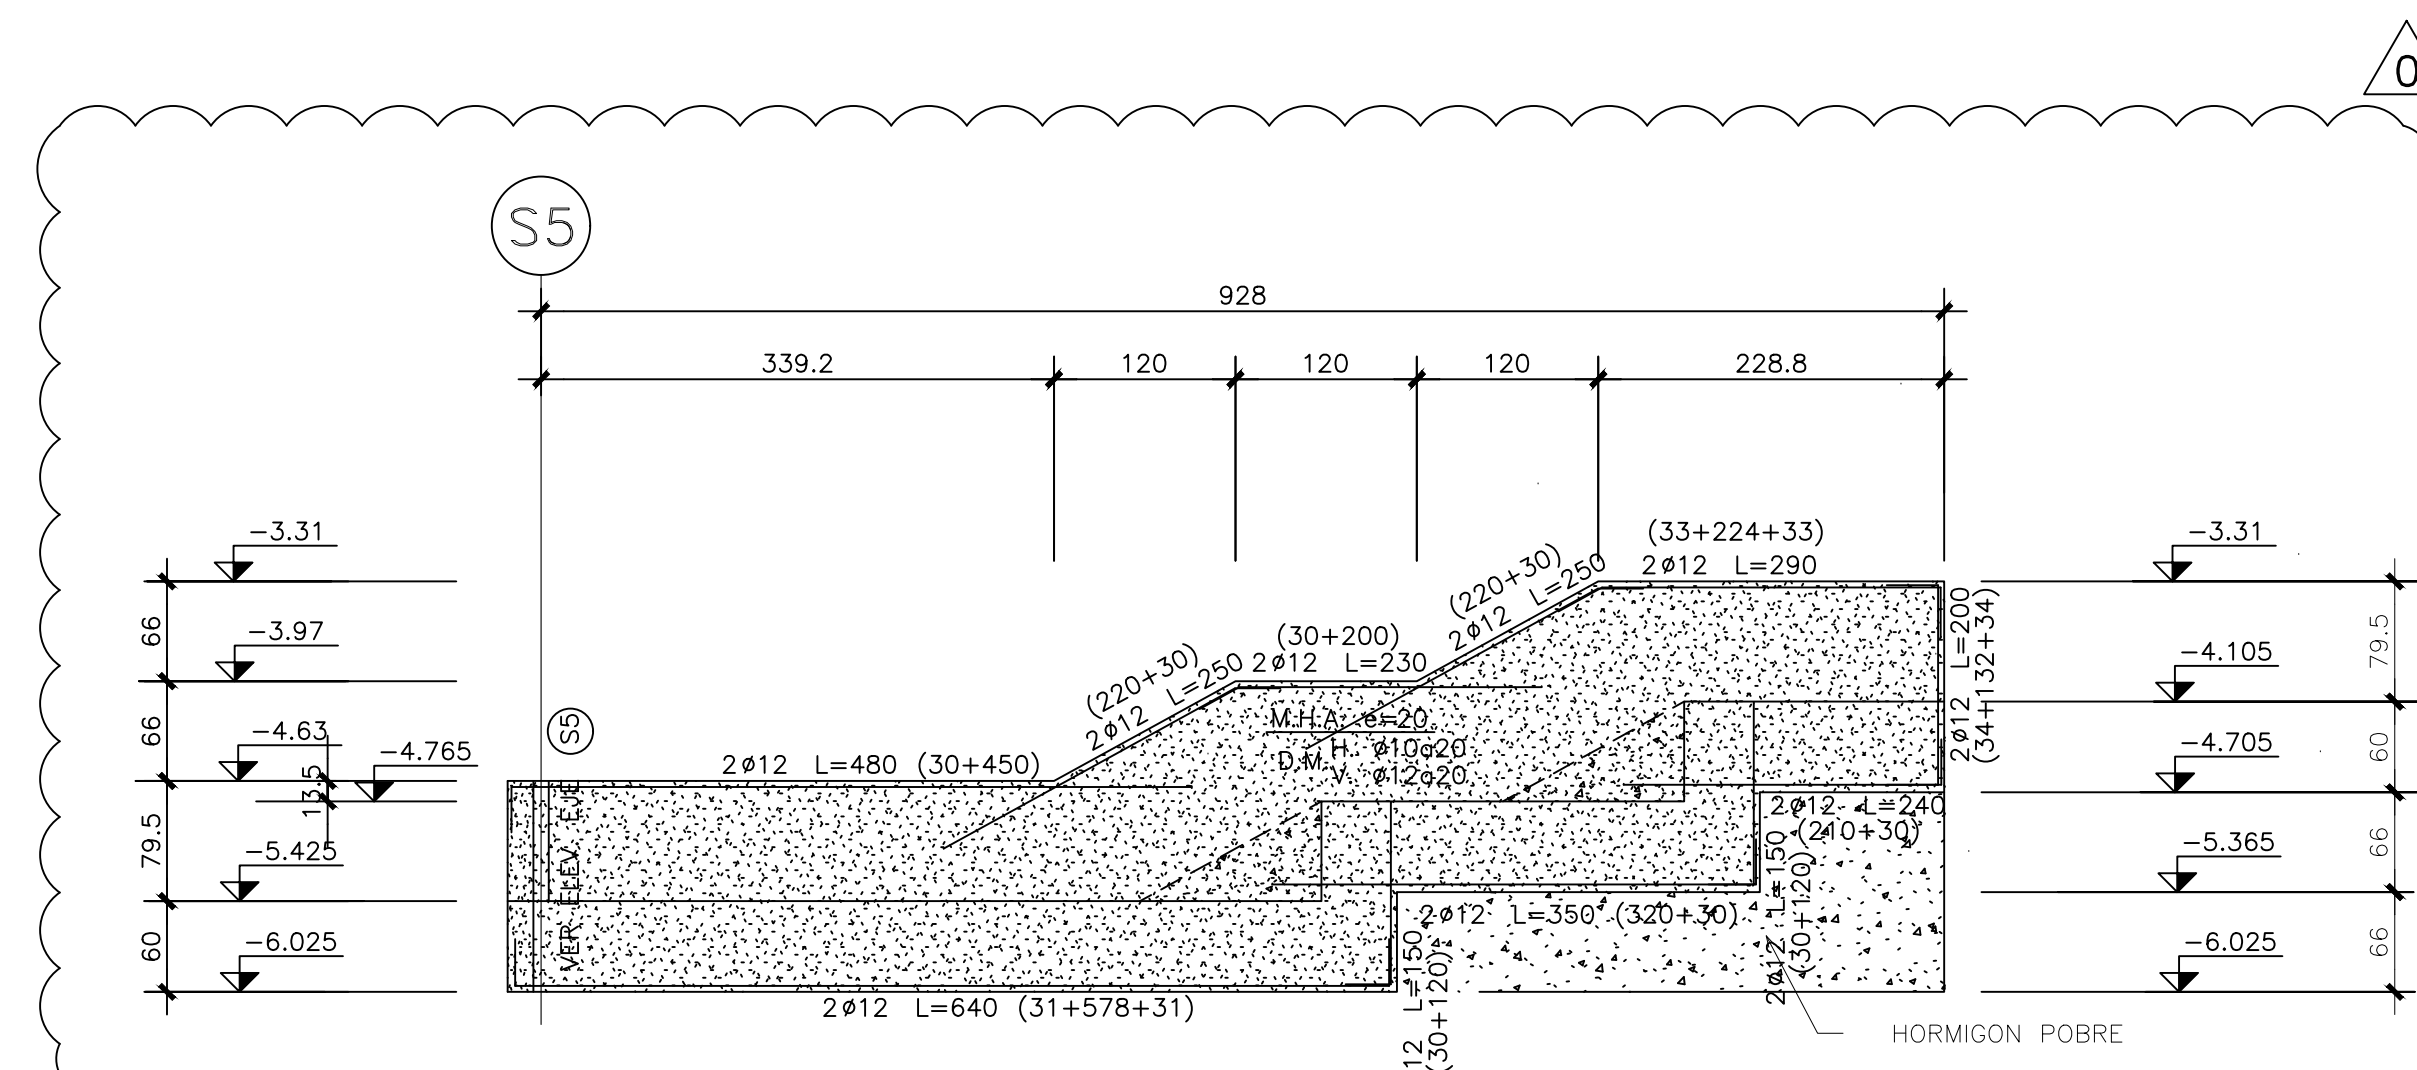

ELEVACION EJE S4

ESCALA 1:50

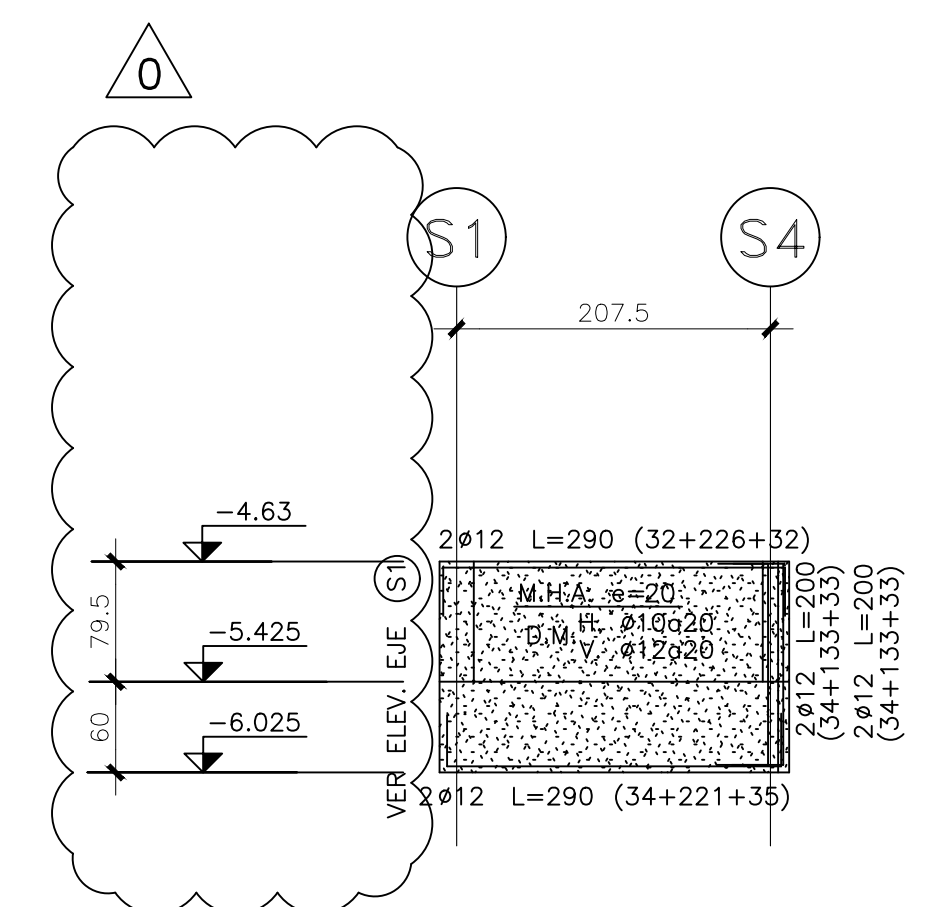

ELEVACION EJE S5

ESCALA 1:50

ESTADO:	APROBADO PARA:
EN DESARROLLO	PRELIMINAR
REVISION	PROPUESTA
CONSTRUCCION	CONSTRUCCION

FIRMA REVISOR INDEPENDIENTE CALCULO	FIRMA ING. RESPONSABLE
ISO	ISO
FOYD: +56 2 2581300 Info@renelagos.com www.renelagos.com	renelagos engineers
PROYECTO	U. DE LOS ANDES (FASE 2)