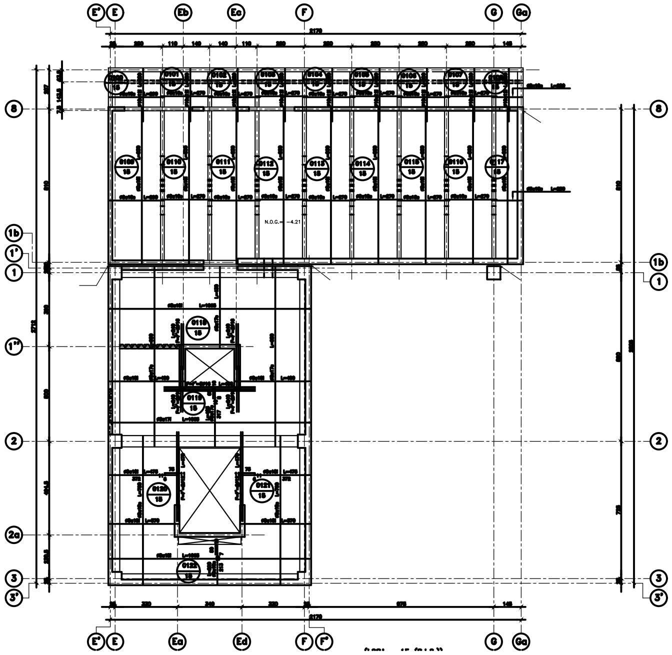

ARMADURA MALLA INFERIOR LOSA CIELO 1° SUBTERRANEO

ESCALA 1/75

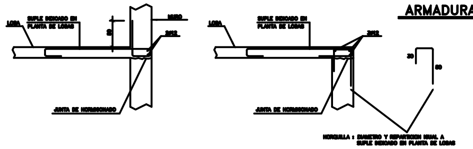

DETALLE ALTERNATIVO SUPLES EN MUROS

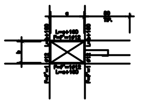

REFUERZO TIP. SHAFT

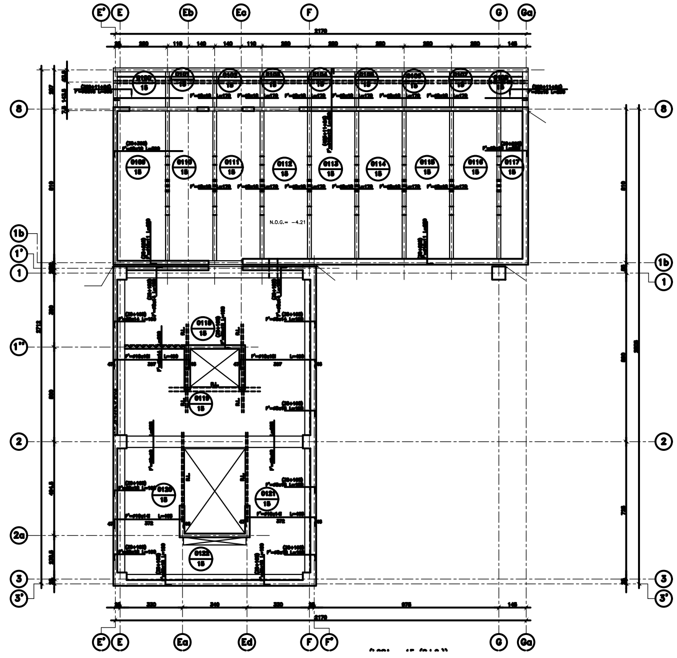

ARMADURA MALLA SUPERIOR LOSA CIELO 1° SUBTERRANEO

2017_67-201.dwg

ESTADO:

APROBADO PARA:

U. DE LOS ANDES

ARMADURA MALLA INFERIOR LOSA CIELO 1° SUBTERRANEO

2017_67-201 A