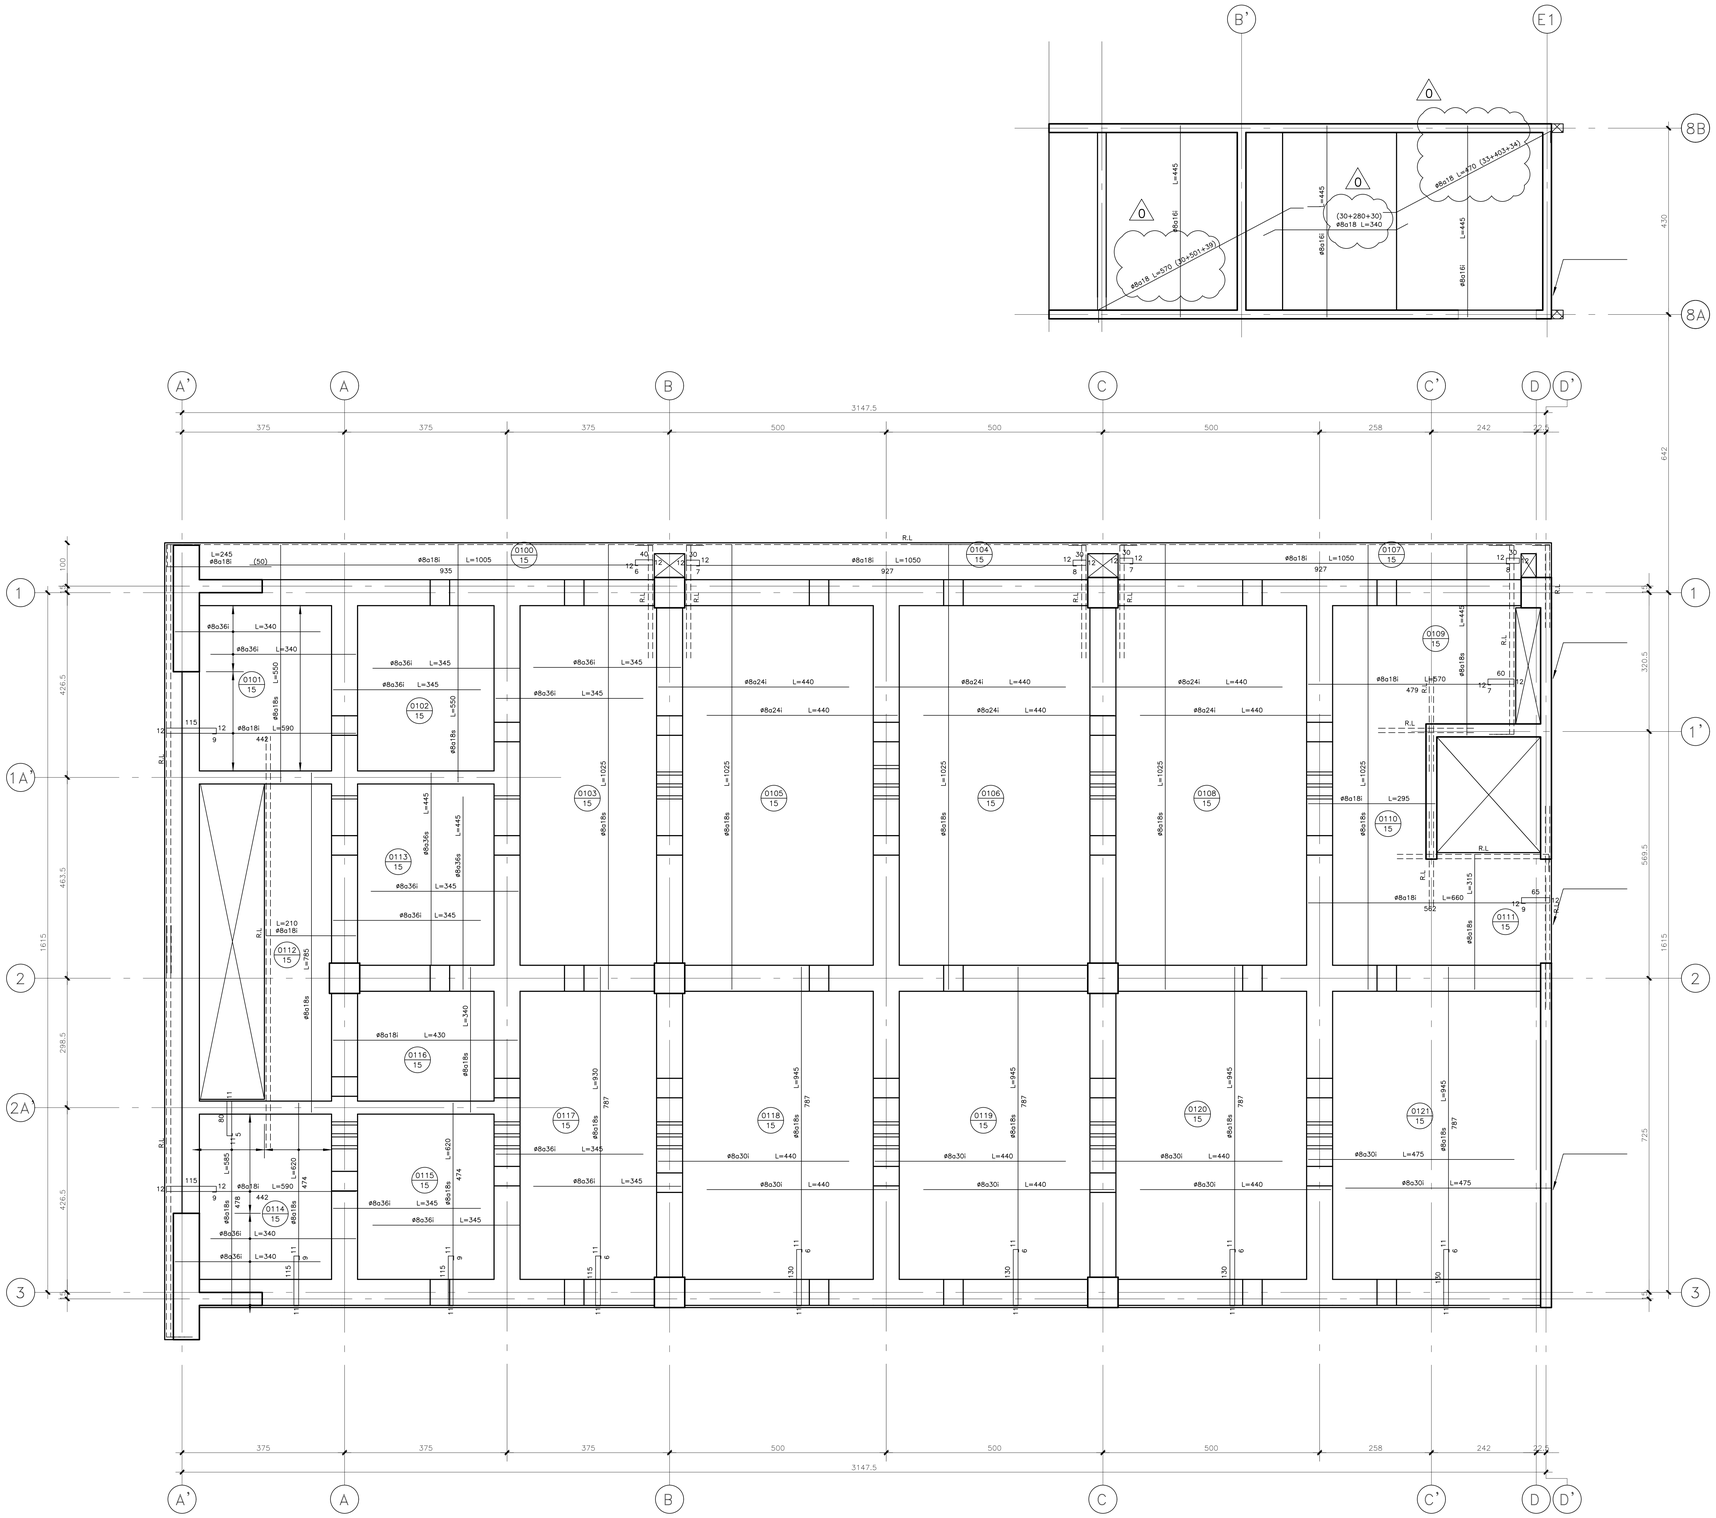


PLANTA ARMADURA INFERIOR CIELO 1°SUBTERRANEO a CIELO PISO 3° (F)

ESCALA 1:50

ESTADO:			APROBADO PARA:		
EN DESARROLLO		PRELIMINAR	PROPUESTA	CONSTRUCCION	X

N°	REVISION	ING. / DIB.	FECHA
0	SE EMITE PARA CONSTRUCCION	MKC/ARB	24/10/2024

RENE LAGOS CONTRERAS
ARQUITECTO

FIRMA RE

FONO: +
Info@re
www.re