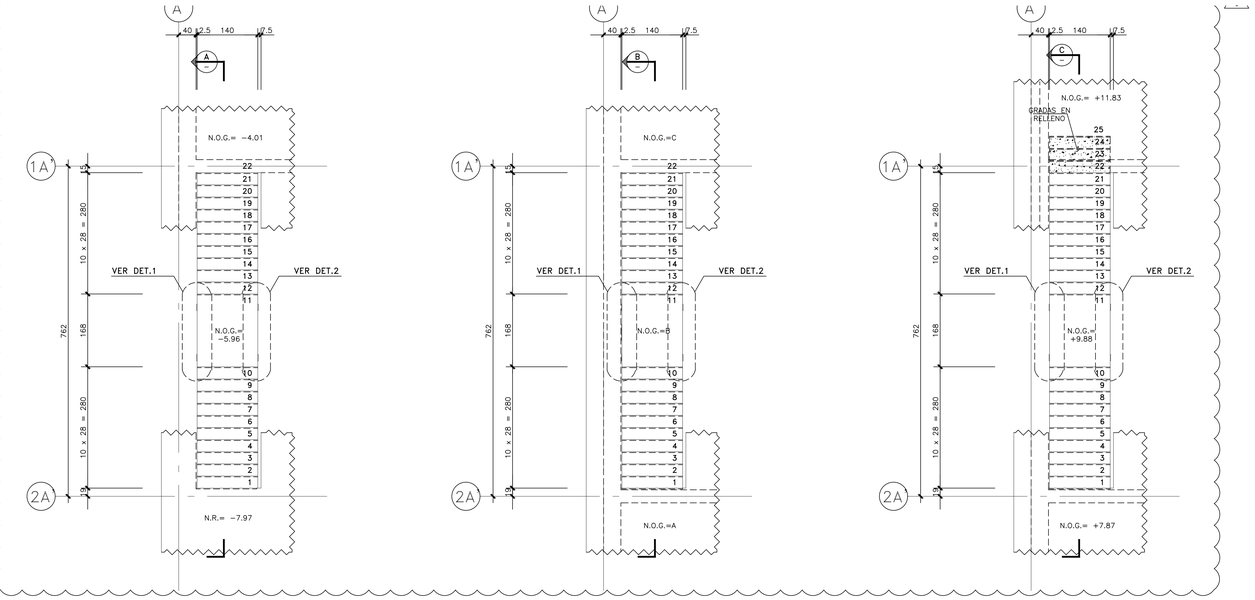


PLANTA ESCALERA 1°SUBT. a 1° PISO

ESCALA 1:50


PLANTA ESCALERA PISOS 1° A 4°

ESCALA 1:50

PLANTA ESCALERA PISO 4° A CUBIERTA

ESCALA 1:50

CUADRO DE NIVELES			
PISO	A	B	C
1° a 2°	−4.01	−2.00	−0.05
2° a 3°	−0.05	+1.96	+3.91
3° a 4°	+3.91	+5.92	+7.87

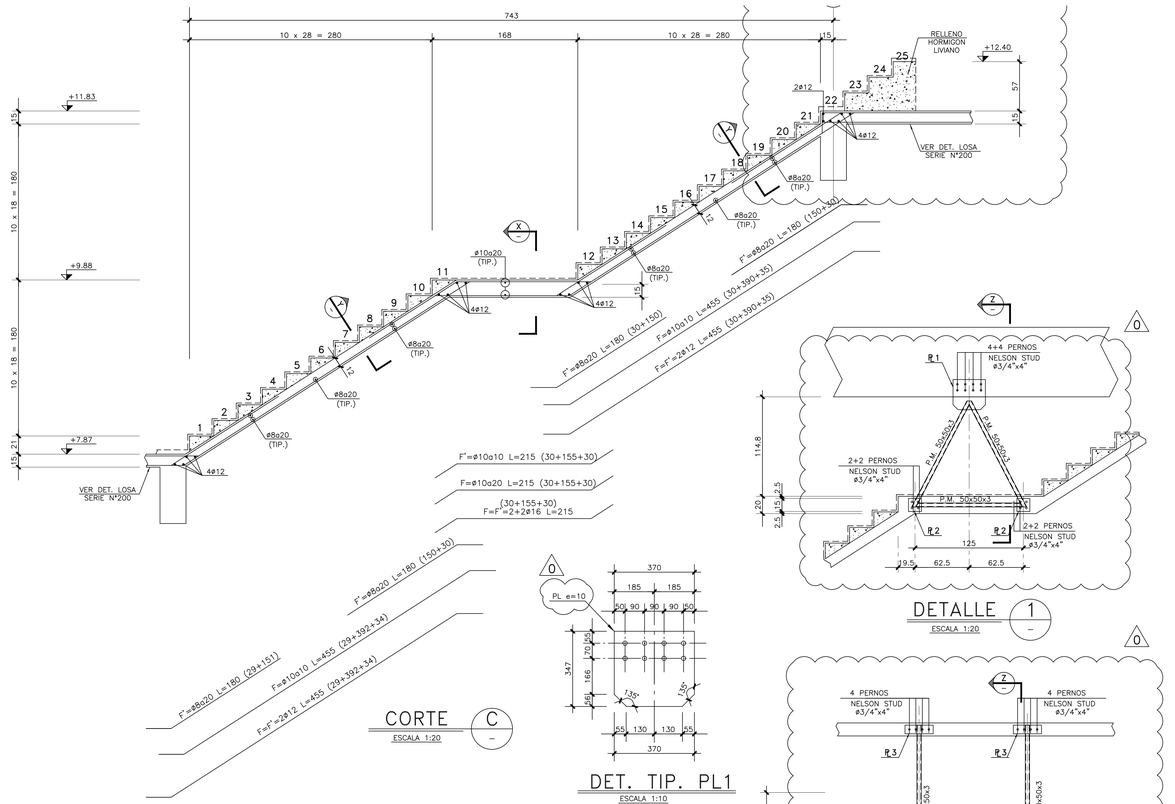

CORTE C

ESCALA 1:20

DET. TIP. PL1


ESCALA 1:10

DETALLE 1

ESCALA 1:20


DET. TIP. PL2

ESCALA 1:10

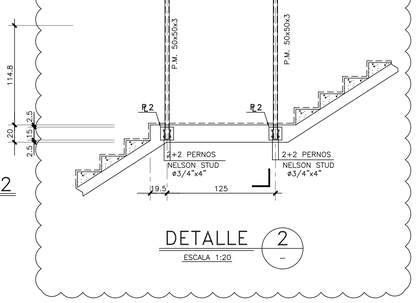


DETALLE 2

ESCALA 1:20

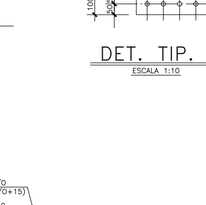


DET. TIP. PL3

ESCALA 1:10

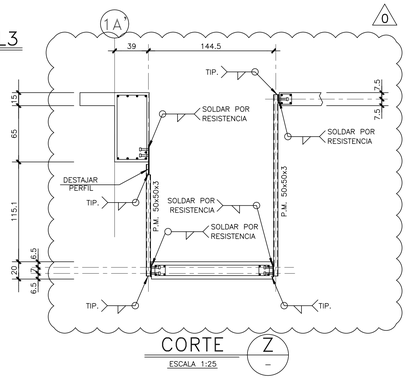

CORTE Z

ESCALA 1:25

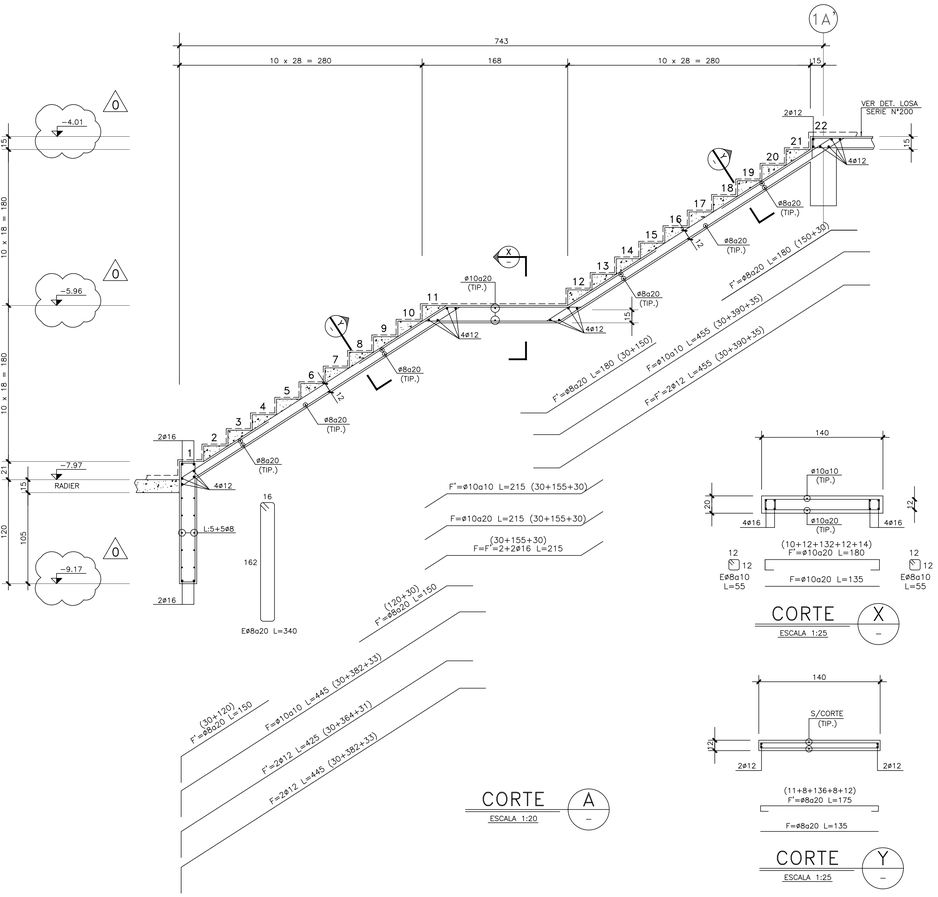

CORTE A


ESCALA 1:20

CORTE X

ESCALA 1:25

CORTE Y

ESCALA 1:25

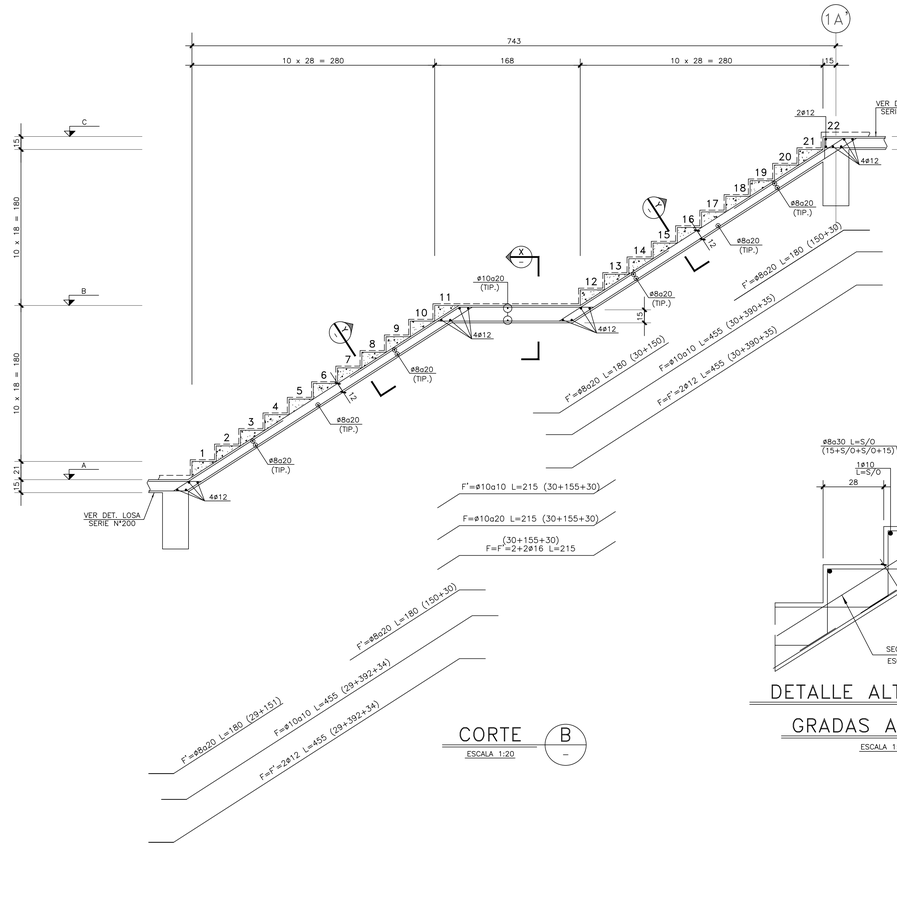

CORTE B

ESCALA 1:20

DETALLE ALTERNATIVO GRADAS ARMADAS

ESCALA 1:10

FIRMA REVISOR INDEPENDIENTE CALCULO

FIRMA ING. RESPONSABLE

ESTADO:		APROBADO PARA:	
EN DESARROLLO	PRELIMINAR	PROPUESTA	CONSTRUCCION X

N°	REVISION	ING. / DIB.	FECHA
0	SE EMITE PARA CONSTRUCCION	MKC/ARB	24/10/2024

FONO: +56 2 25941300
info@renelagos.com
www.renelagos.com
renelagos engineers

RENE LAGOS CONTRERAS
MARIANNE KUPFER CAUTY
GONZALO ARIAS ESPARZA
LUIS DE LA FUENTE MARTINEZ
SIMON SANHUEZA TORREALBA

PROYECTO: U. DE LOS ANDES (FASE 2)

CONTENIDO: DET. DE ESCALERAS 1°S a CUBIERTA

CALCULO: M. KUPFER C.
DISEÑO: A. ROCHA B.
DIBUJO: A. ROCHA B.
REVISO: M. KUPFER C.
ESCALAS: INDICADAS
FECHA: OCTUBRE 2024
NUMERO: 2024_22-500
REV.: 0

2024_22-500.dwg
Wed 23 Oct 2024 - 05:58pm