
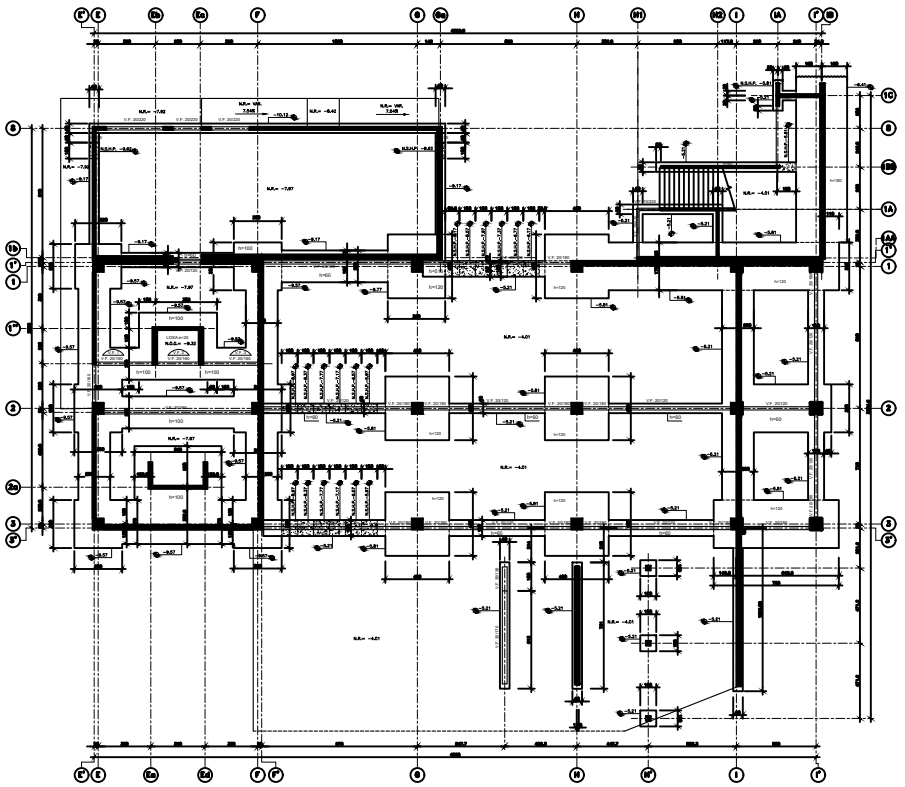


(SOBRE SUPERIOR RADIER E/PLANTA)

PLANTA FUNDACIONES

ESCALA 1:50

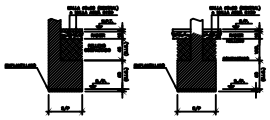

CORTE TIP. FUNDACIONES

ESCALA 1:25

NOTA

LOS ASENTAMIENTOS DE SUELO DEBERAN SER MENOR AL INDICADO EN INFORME DE MECANICA DE SUELOS EMITIDO POR G T Y INGENIEROS CON FECHA JULIO 2017.

NORMAS DE DISEÑO

- Nch 433 Of. 96 MODIF. 2009
- CODIGO ACI318S-08
- DECRETO SUPREMO N° 60 DEL MINISTERIO DE VIVIENDA Y URBANISMO, DE FECHA 15/12/2011
- DECRETO SUPREMO N° 61 DEL MINISTERIO DE VIVIENDA Y URBANISMO, DE FECHA 15/12/2011

MATERIALES

HORMIGÓN G25_10: (Desde fundaciones A Cielo plac 3°)

- RESISTENCIA A COMPRESIÓN PROBETA CILÍNDRICA f'c' = 25 MPA, EQUIVALENTE A RESISTENCIA A COMPRESIÓN PROBETA CÚBICA R30 = 30 MPA Y 9005 HC

HORMIGÓN G30_10 : (Radier armado Ø8 c 20 € cama C-357)

- RESISTENCIA A COMPRESIÓN PROBETA CILÍNDRICA f'c' = 20 MPA, EQUIVALENTE A RESISTENCIA A COMPRESIÓN PROBETA CÚBICA R25 = 25 MPA Y 9005 HC

-TAMAÑO MÁXIMO DE ÁRIDO Y ASENTAMIENTO DE CONO DEBERÁN SER DEFINIDOS POR LA CONSTRUCTORA DE MODO DE GARANTIZAR EL CORRECTO HORMIGONADO DE LOS ELEMENTOS.

-LA COMPOSICION DEL HORMIGON DEBERA CONSIDERAR LOS PARAMETROS DE DURABILIDAD ESTABLECIDOS EN NCh170:2016. LOS GRADOS DE EXPOSICION DEBERAN SER DEFINIDOS POR UN ESPECIALISTA EN MATERIA DE HORMIGONES, DE ACUERDO A:

- EMPLAZAMIENTO Y ENTORNO
- TIPO DE EXPOSICIÓN
- USO DE MEDIDAS ESPECIALES DE PROTECCIÓN
- EXISTENCIA DE ESTUDIOS ESPECIALES

A FALTA DE ESPECIALISTA SE DEBE CONSIDERAR LAS CONDICIONES MAS SEVERAS ESTABLECIDAS EN NCh170:2016.

EN CASO QUE SE REQUIERA, POR CONDICIONES DE DURABILIDAD, UN HORMIGON DE GRADO SUPERIOR AL ESPECIFICADO, ESTO DEBE SER INFORMADO A MLC.

ACERO REFUERZO: A630-420H

ACERO ESTRUCTURAS METALICAS: A36

SOLDADURAS ELECTRODOS: E70-XX

ANTECEDENTES SISMICOS

ZONA SISMICA 3
TIPO DE SUELO D

PRESIONES ADMISIBLES DEL SUELO

CARGA NORMAL = 4.0 Kg/cm²
CARGA SISMICA= 5.0 Kg/cm²