


V.S.I. 20/150
EDOLA 562

CUADRO DE CONTRAFLECHAS	
LONG.	CONTRAFLECHA (mm.)
0000	-
0001	-
0100	-
0101	-
0200	-
0201	-
0300	-
0301	-
0400	-
0401	-
0500	1,0
0501	1,0
0600	1,0
0601	1,0
0700	1,0
0701	1,0
0800	0,0
0801	0,0
0900	-
0901	-
1000	-

CUADRO DE CONTRAFLECHA	
LÍNEA	CONTRAFLECHA (mm.)
100	0,0
101	--
102	--
103	--
104	1
105	1
106	1
107	1
108	1
109	1
110	0,0
111	1
112	--
113	--
114	0,0
115	0,0
116	0,0
117	0,0

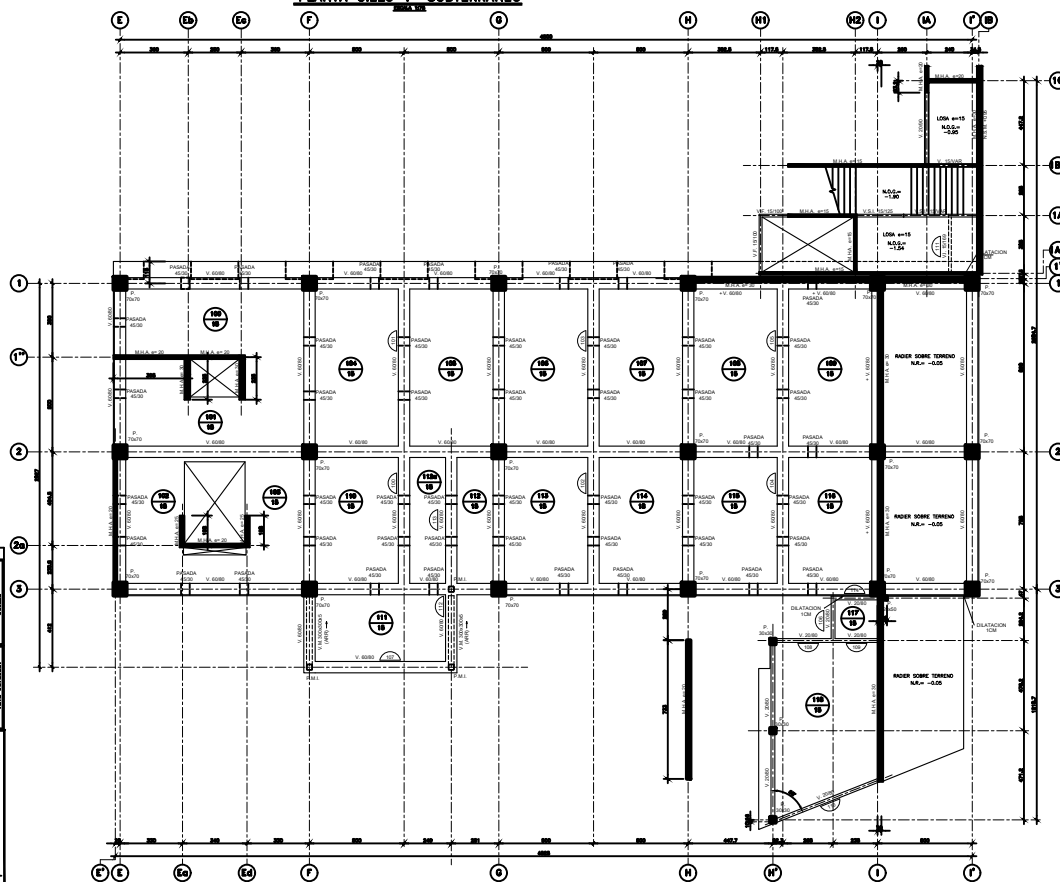

(LOSA c=15 (S.I.C.))
(NIVEL SUPERIOR LOSA -0.05)
PLANTA CIELO PISO 1°
Escala 1:50