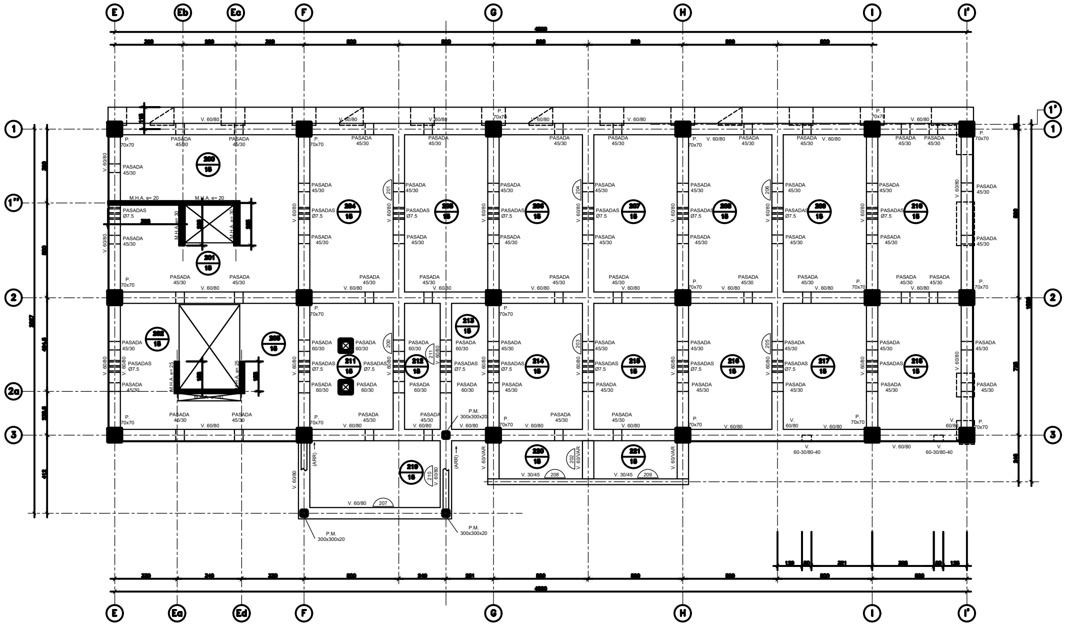

(LOSA e=15 (S.I.C.))
(NIVEL SUPERIOR LOSA +3.91)

PLANTA CIELO PISO 2°

ESCALA 1:75

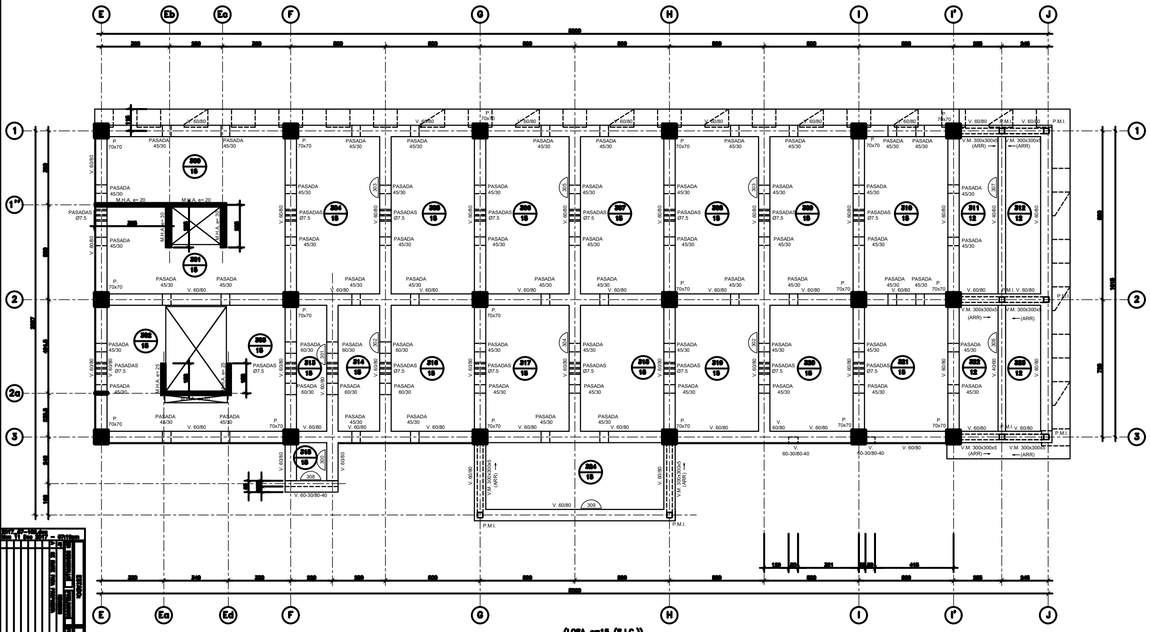

(LOSA e=15 (S.I.C.))
(NIVEL SUPERIOR LOSA +7.87)

PLANTA CIELO PISO 3°

ESCALA 1:75

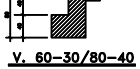

V. 60-30/80-40

ESCALA 1:25

CUADRO DE CONTRAFLECHAS	
LOSA	CONTRAFLECHA (cm.)
200	0.5
201	–
202	–
203	–
204	1
205	1
206	1
207	1
208	1
209	1
210	1
211	0.5
212	–
213	–
214	0.5
215	0.5
216	0.5
217	0.5
218	1
219	1
220	–
221	–

CUADRO DE CONTRAFLECHAS	
LOSA	CONTRAFLECHA (cm.)
300	–
301	–
302	–
303	–
304	1
305	1
306	1
307	1
308	1
309	1
310	1
311	–
312	–
313	–
314	–
315	–
316	0.5
317	0.5
318	0.5
319	0.5
320	0.5
321	0.5
322	–
323	–
324	2

2017_67-102.dwg
Mon 11 Dec 2017 - 07:19am

ESTADO:

APROBADO PARA:

U. DE LOS ANDES

PLANTA CIELO PISO 1°
PLANTA CIELO PISO 2°

2017_67-102

A