



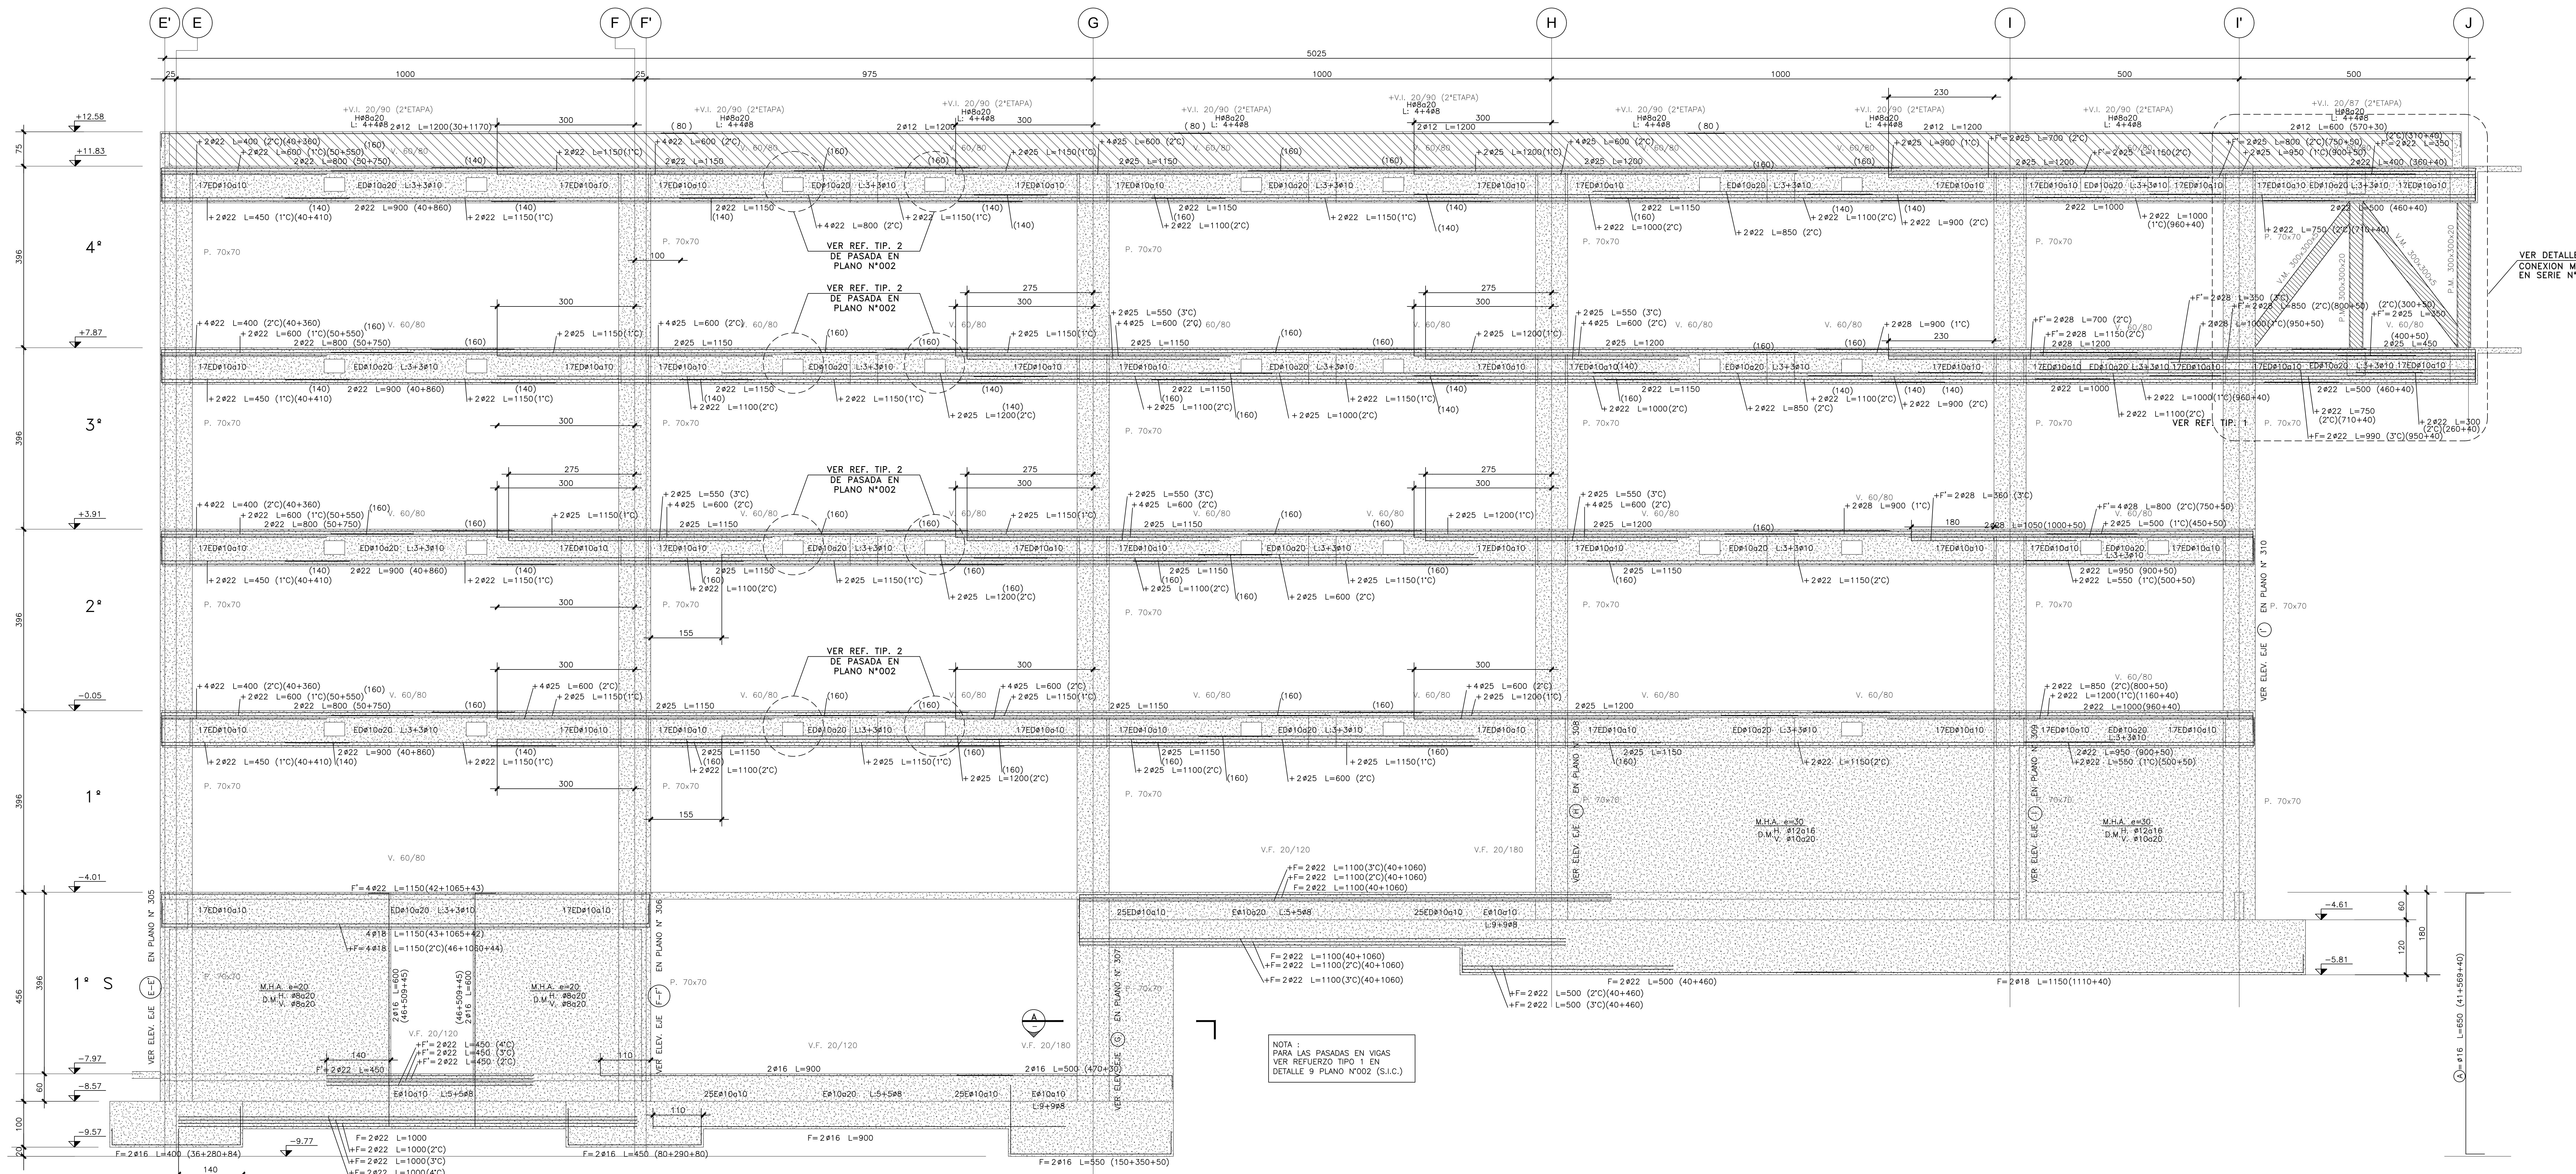

ELEVACION EJE 1-1'

ESCALA 1:50

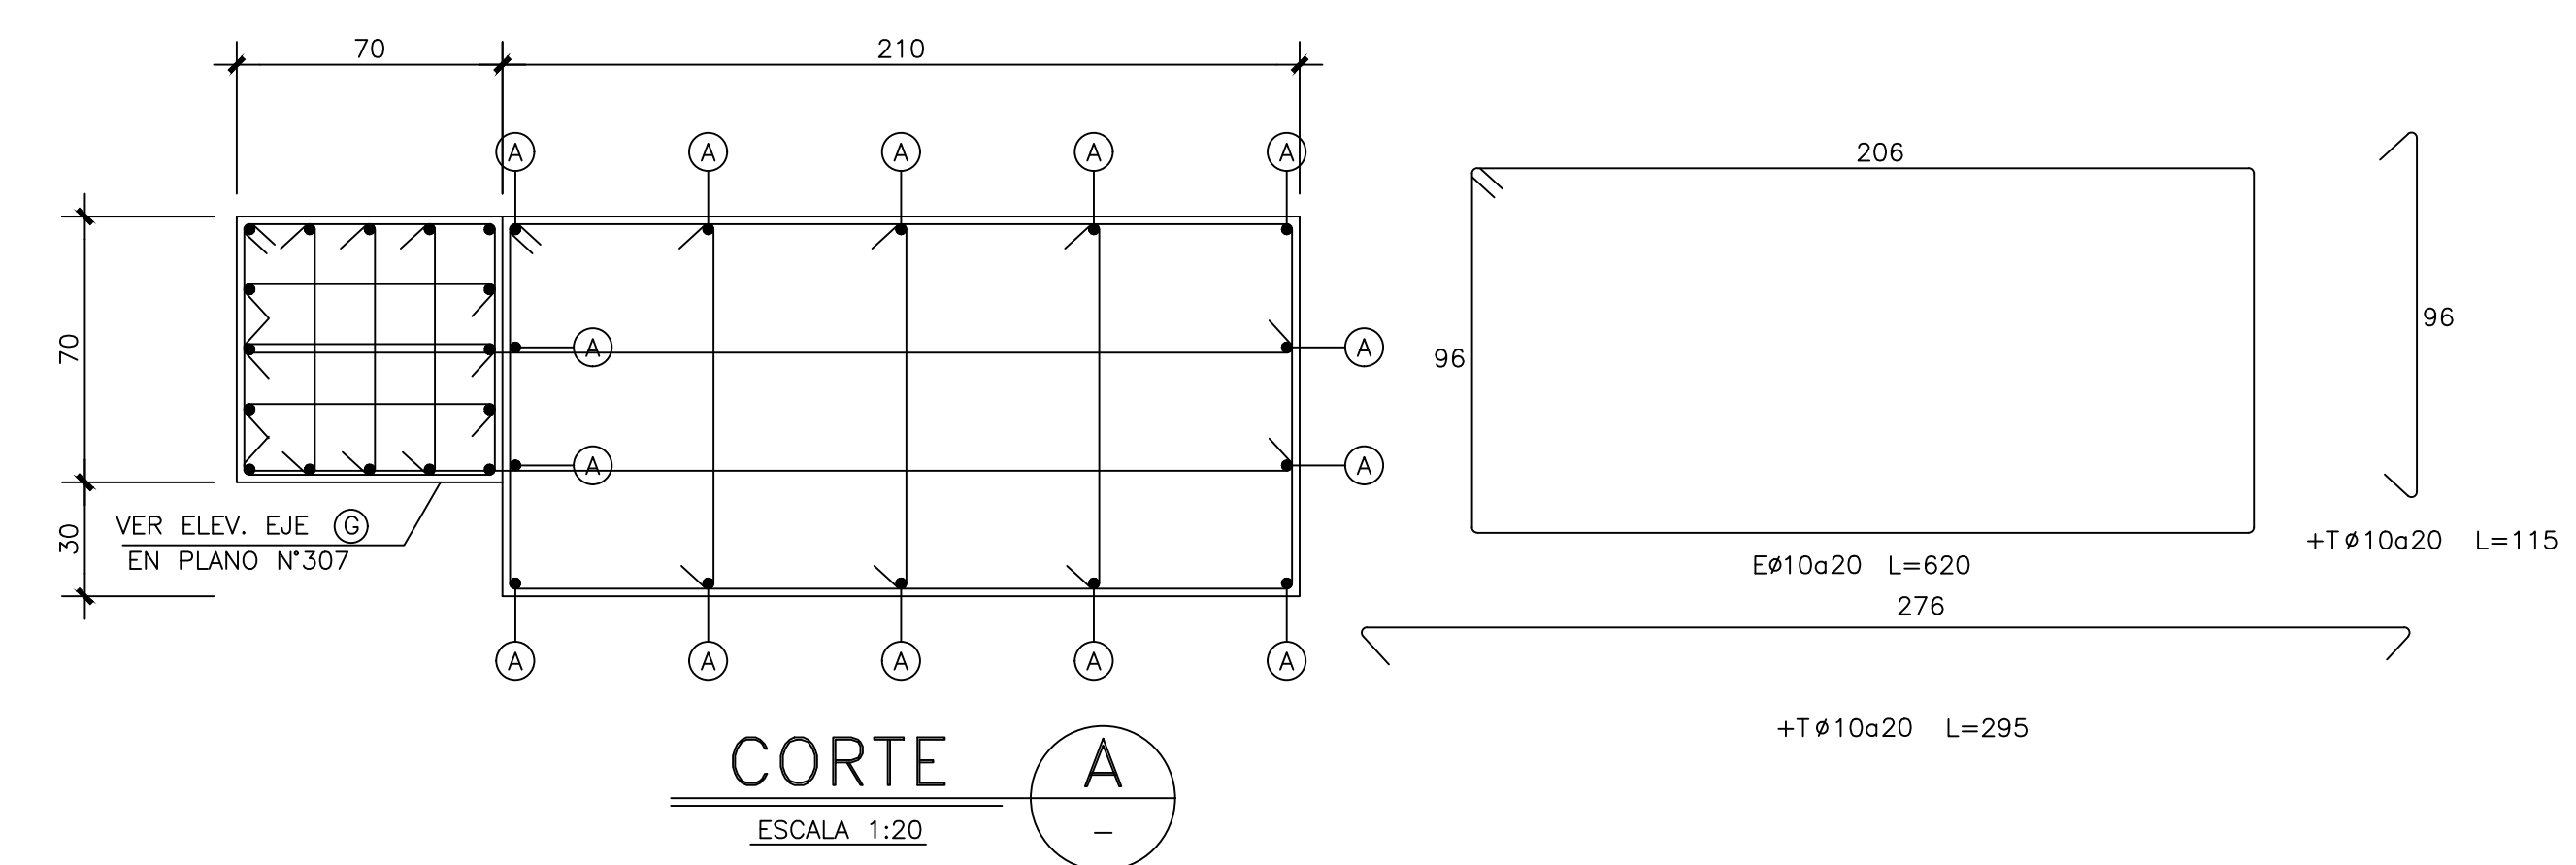

CORTE A

ESCALA 1:20

04-17-2017 04-13-2017 04-13-2017	ESTADO:			APROBADO PARA:		MAGDALENA 140 Piso 24 OF.2402 LAS CONDES SANTIAGO, CHILE FONOS: +56 2 25841300 info@renelagos.com www.renelagos.com		renelagos engineers	
	EN DESARROLLO	PRELIMINAR		PROPUESTA	X CONSTRUCCION				
	N°	REVISION	ING./DIB.	FECHA					
	1	SE EMITE PARA PROPUESTA	JMC/EMF	22/02/2018					
						PROYECTO			
					CONTENIDO		ELEVACION EJE 1-1'		
					RENE LAGOS CONTRERAS MOLINA C. E. MORALES F. DISEÑO REVISOR FECHA NUMERO		REVISOR FECHA NUMERO		
					CALCULO		E. MORALES F.		
					DISEÑO		E. MORALES F.		
					REVISOR		E. MORALES F.		
					FECHA		DICIEMBRE 2017		
					NUMERO		2017_67-300		