



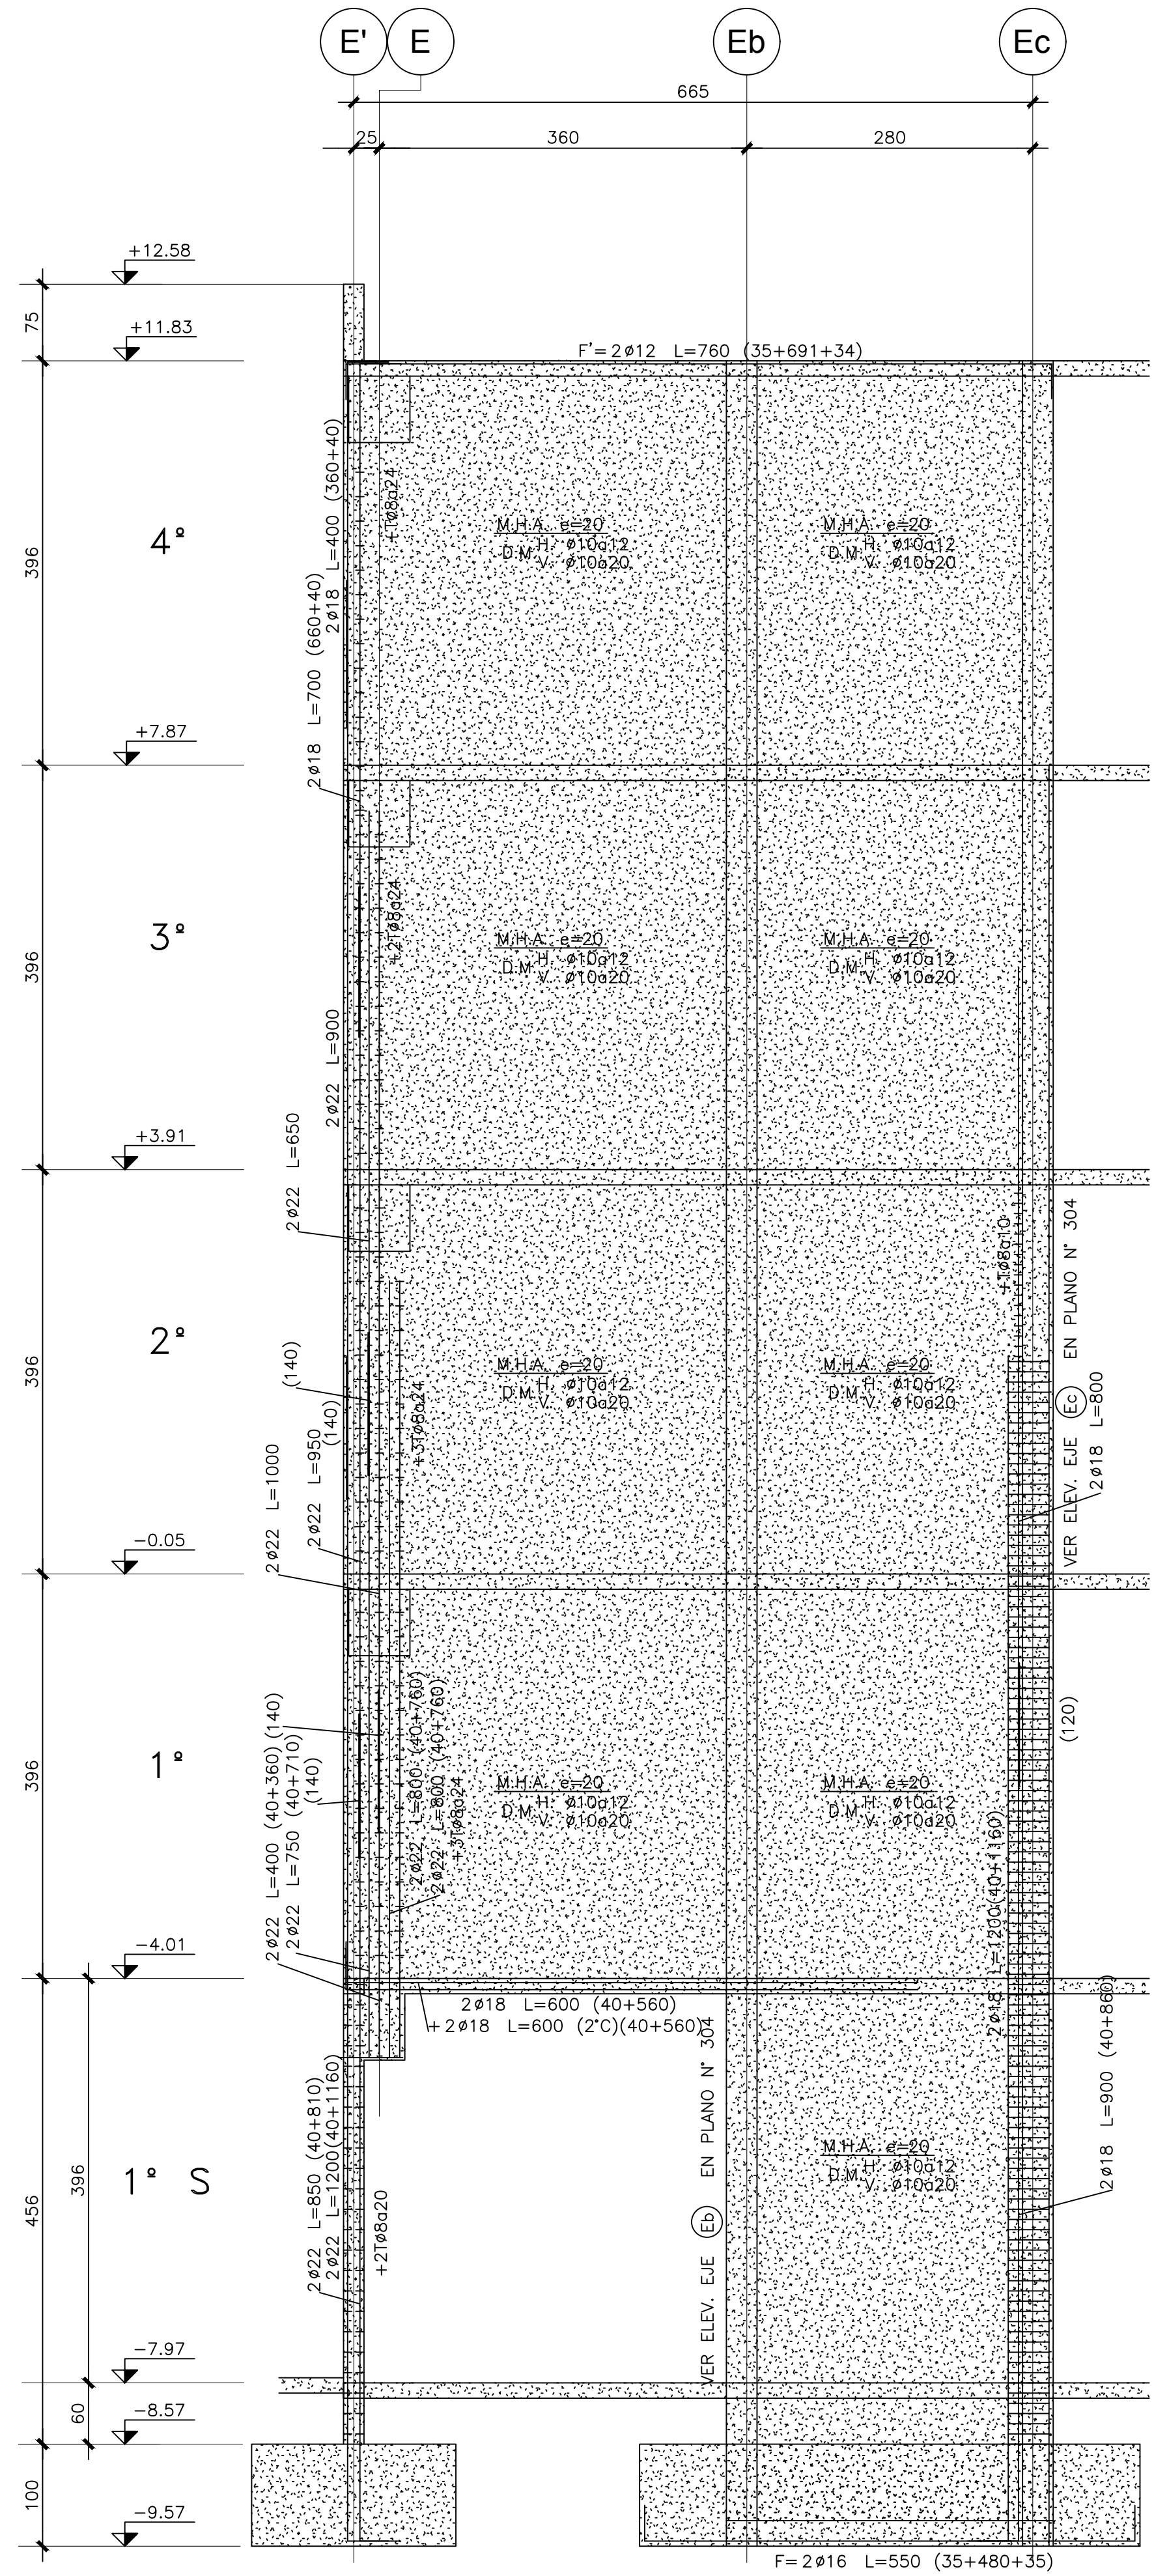


ELEVACION EJE 1''

ESCALA 1:50

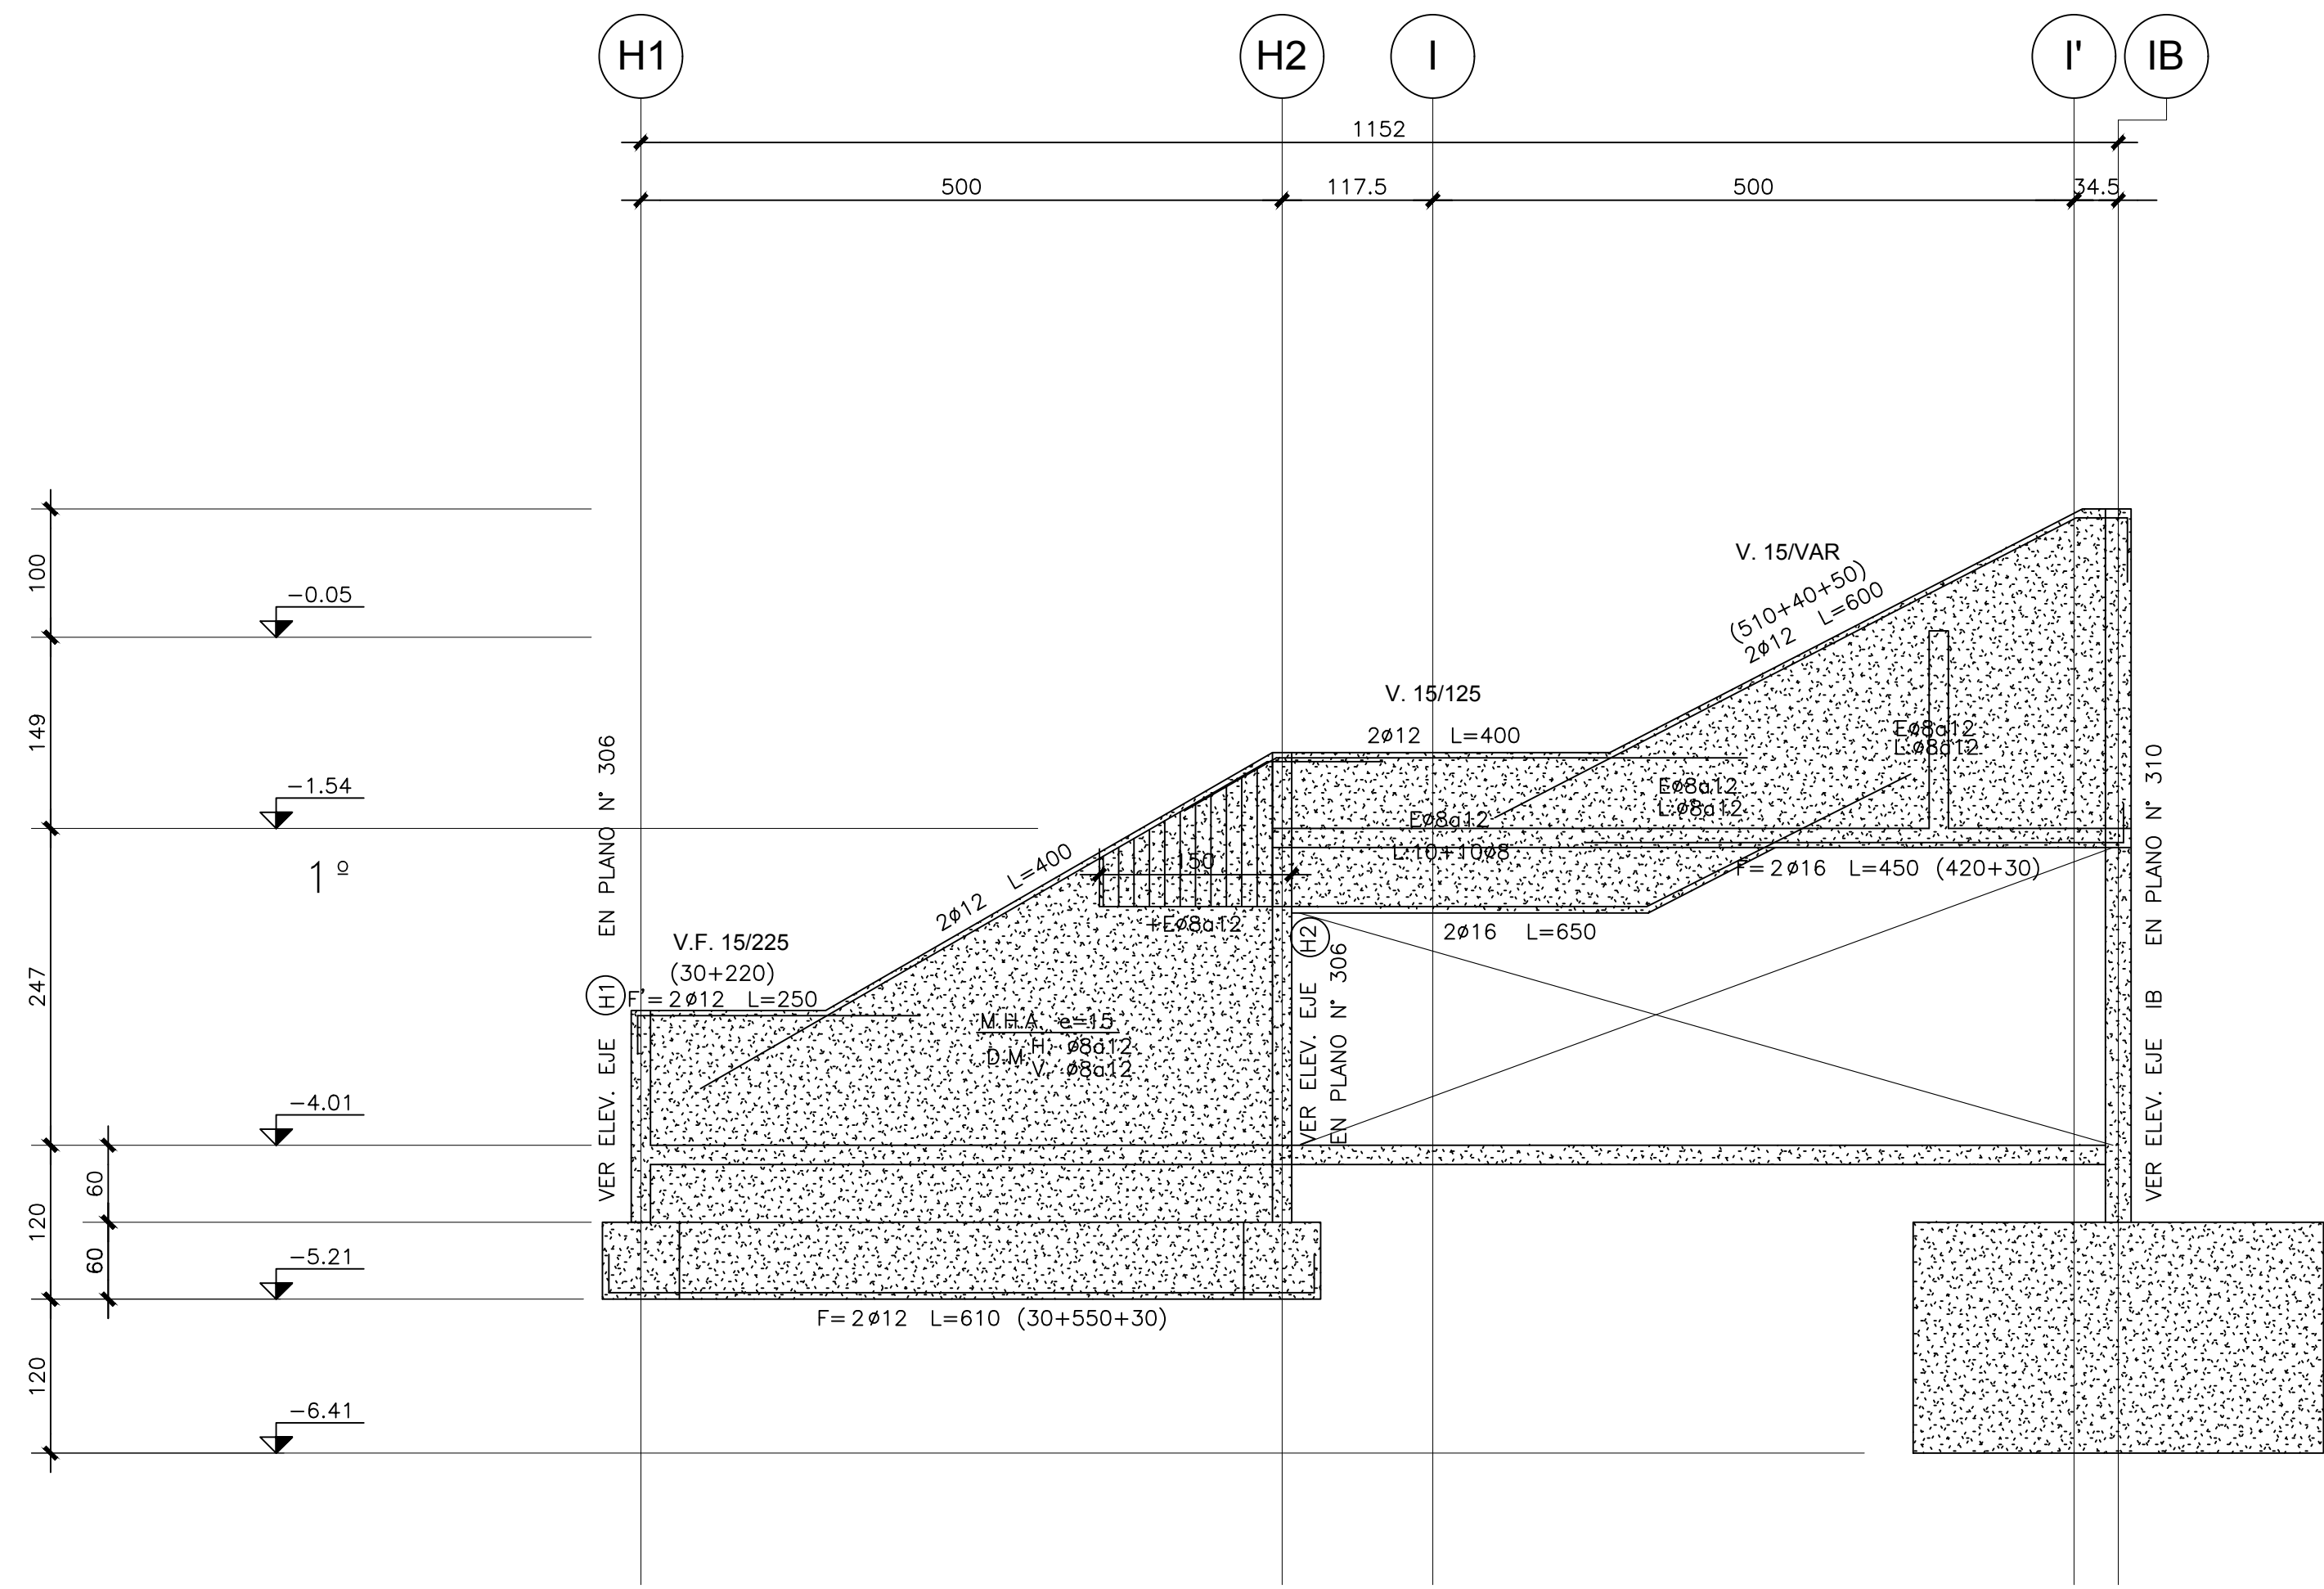


ELEVACION EJE 1A

ESCALA 1:50

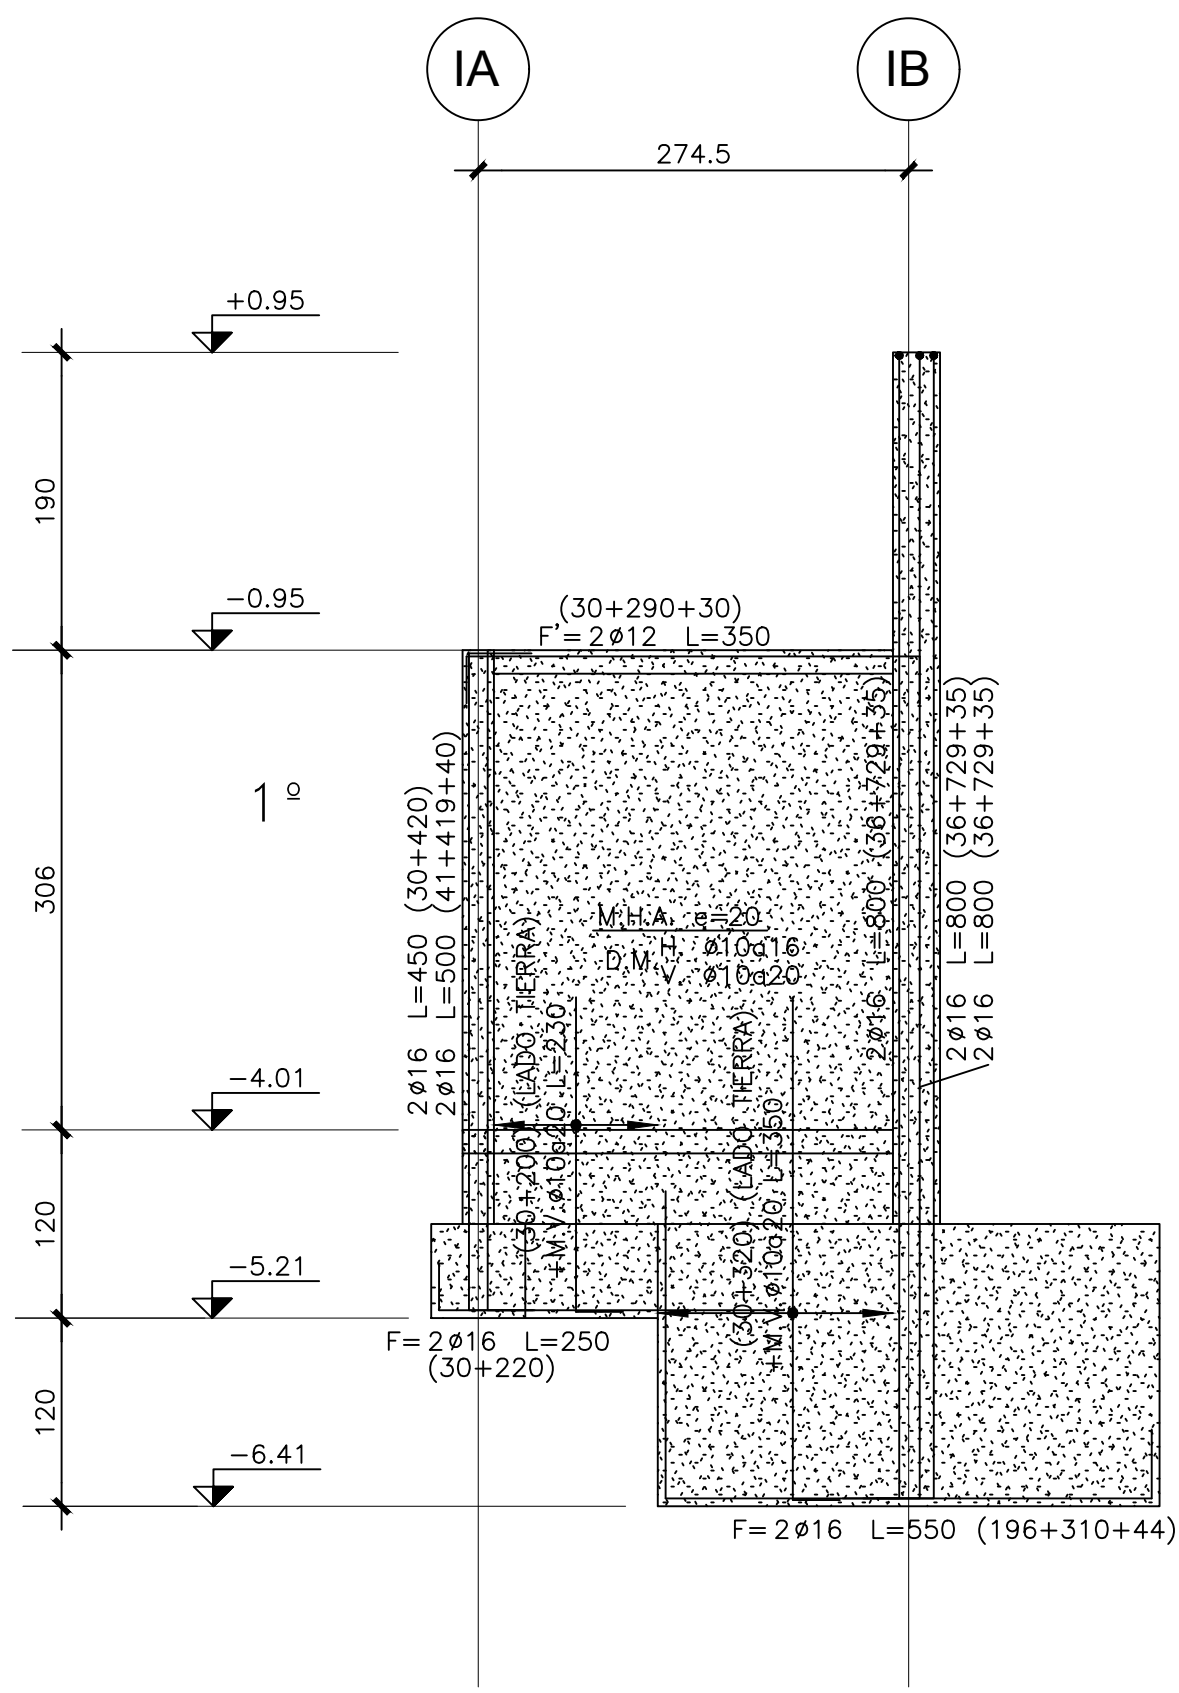


ELEVACION EJE 1C

ESCALA 1:50

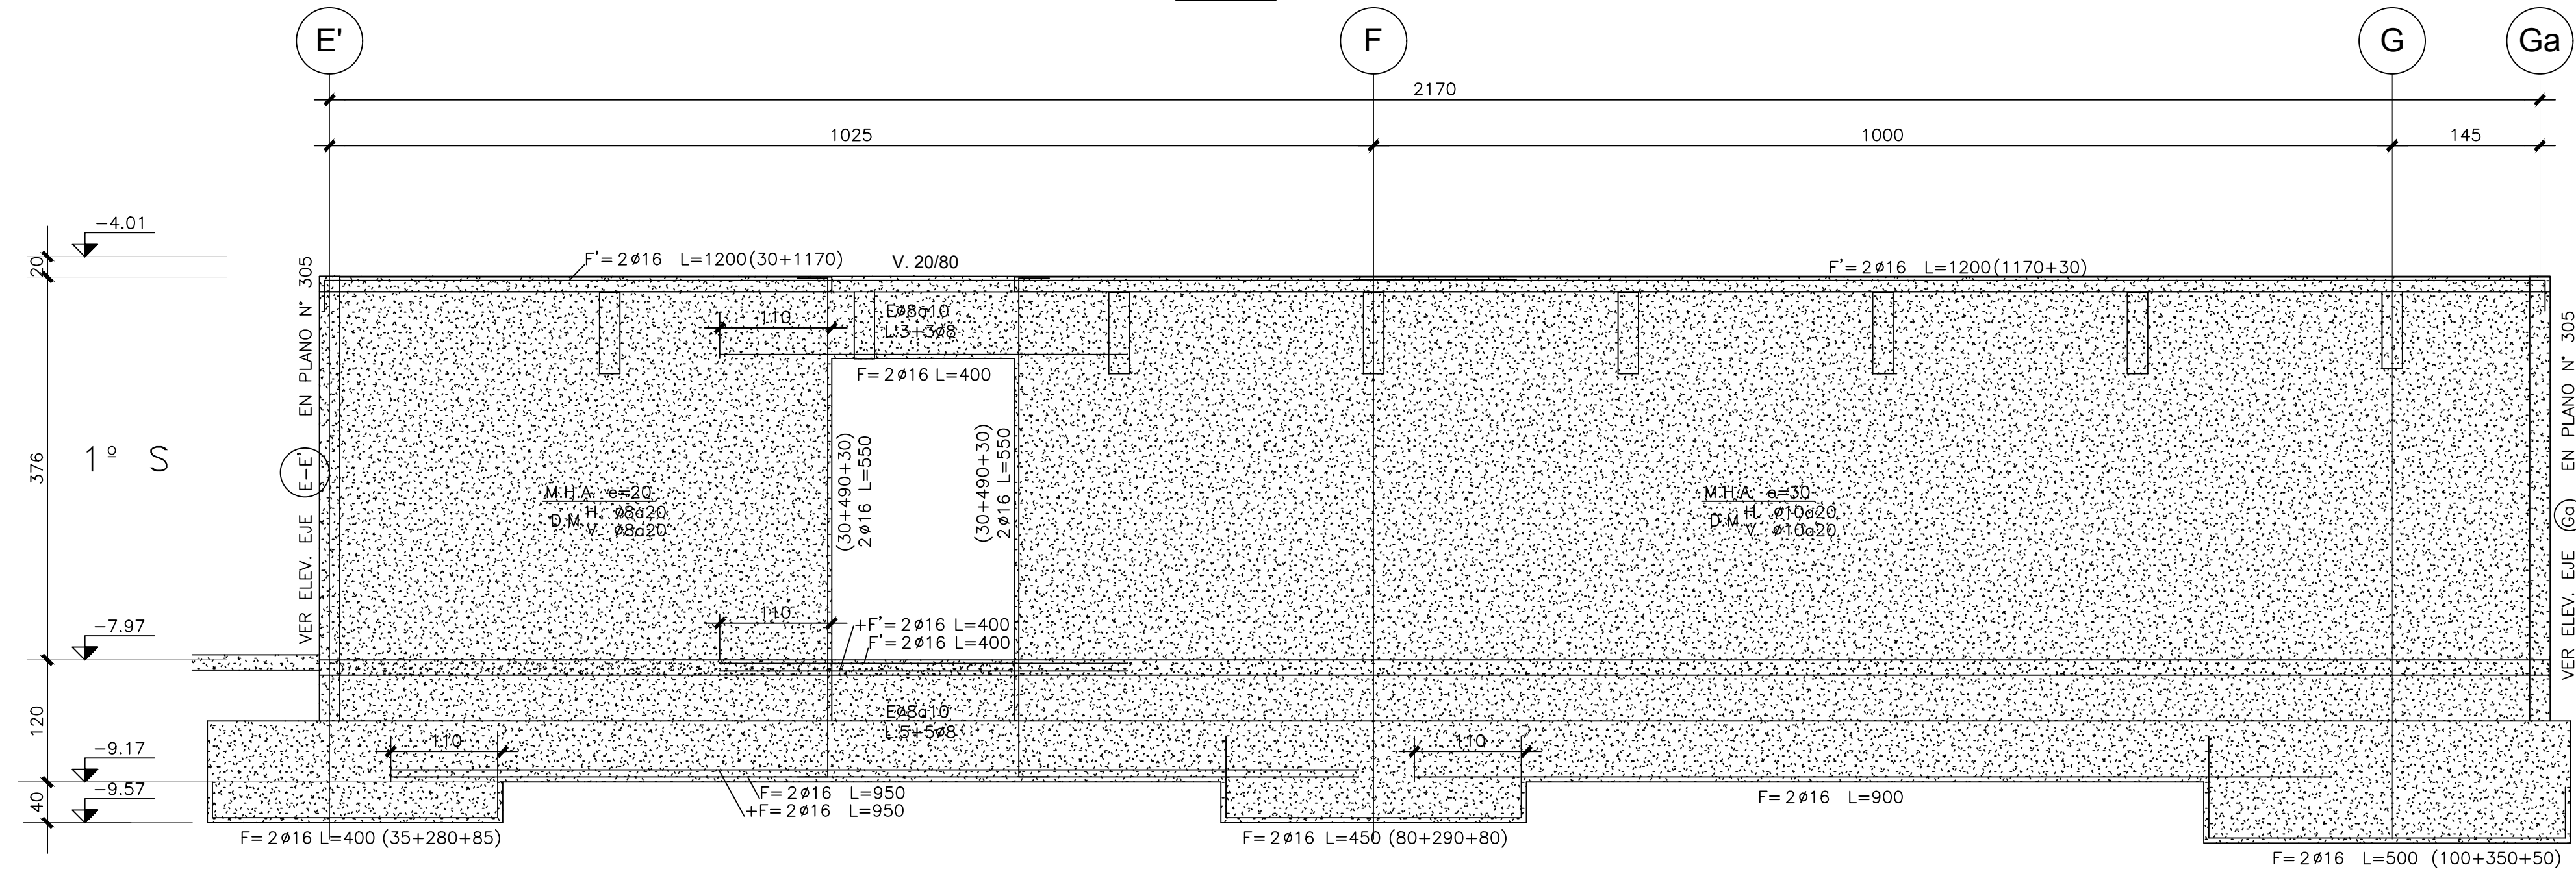


ELEVACION EJE 1b

ESCALA 1:50

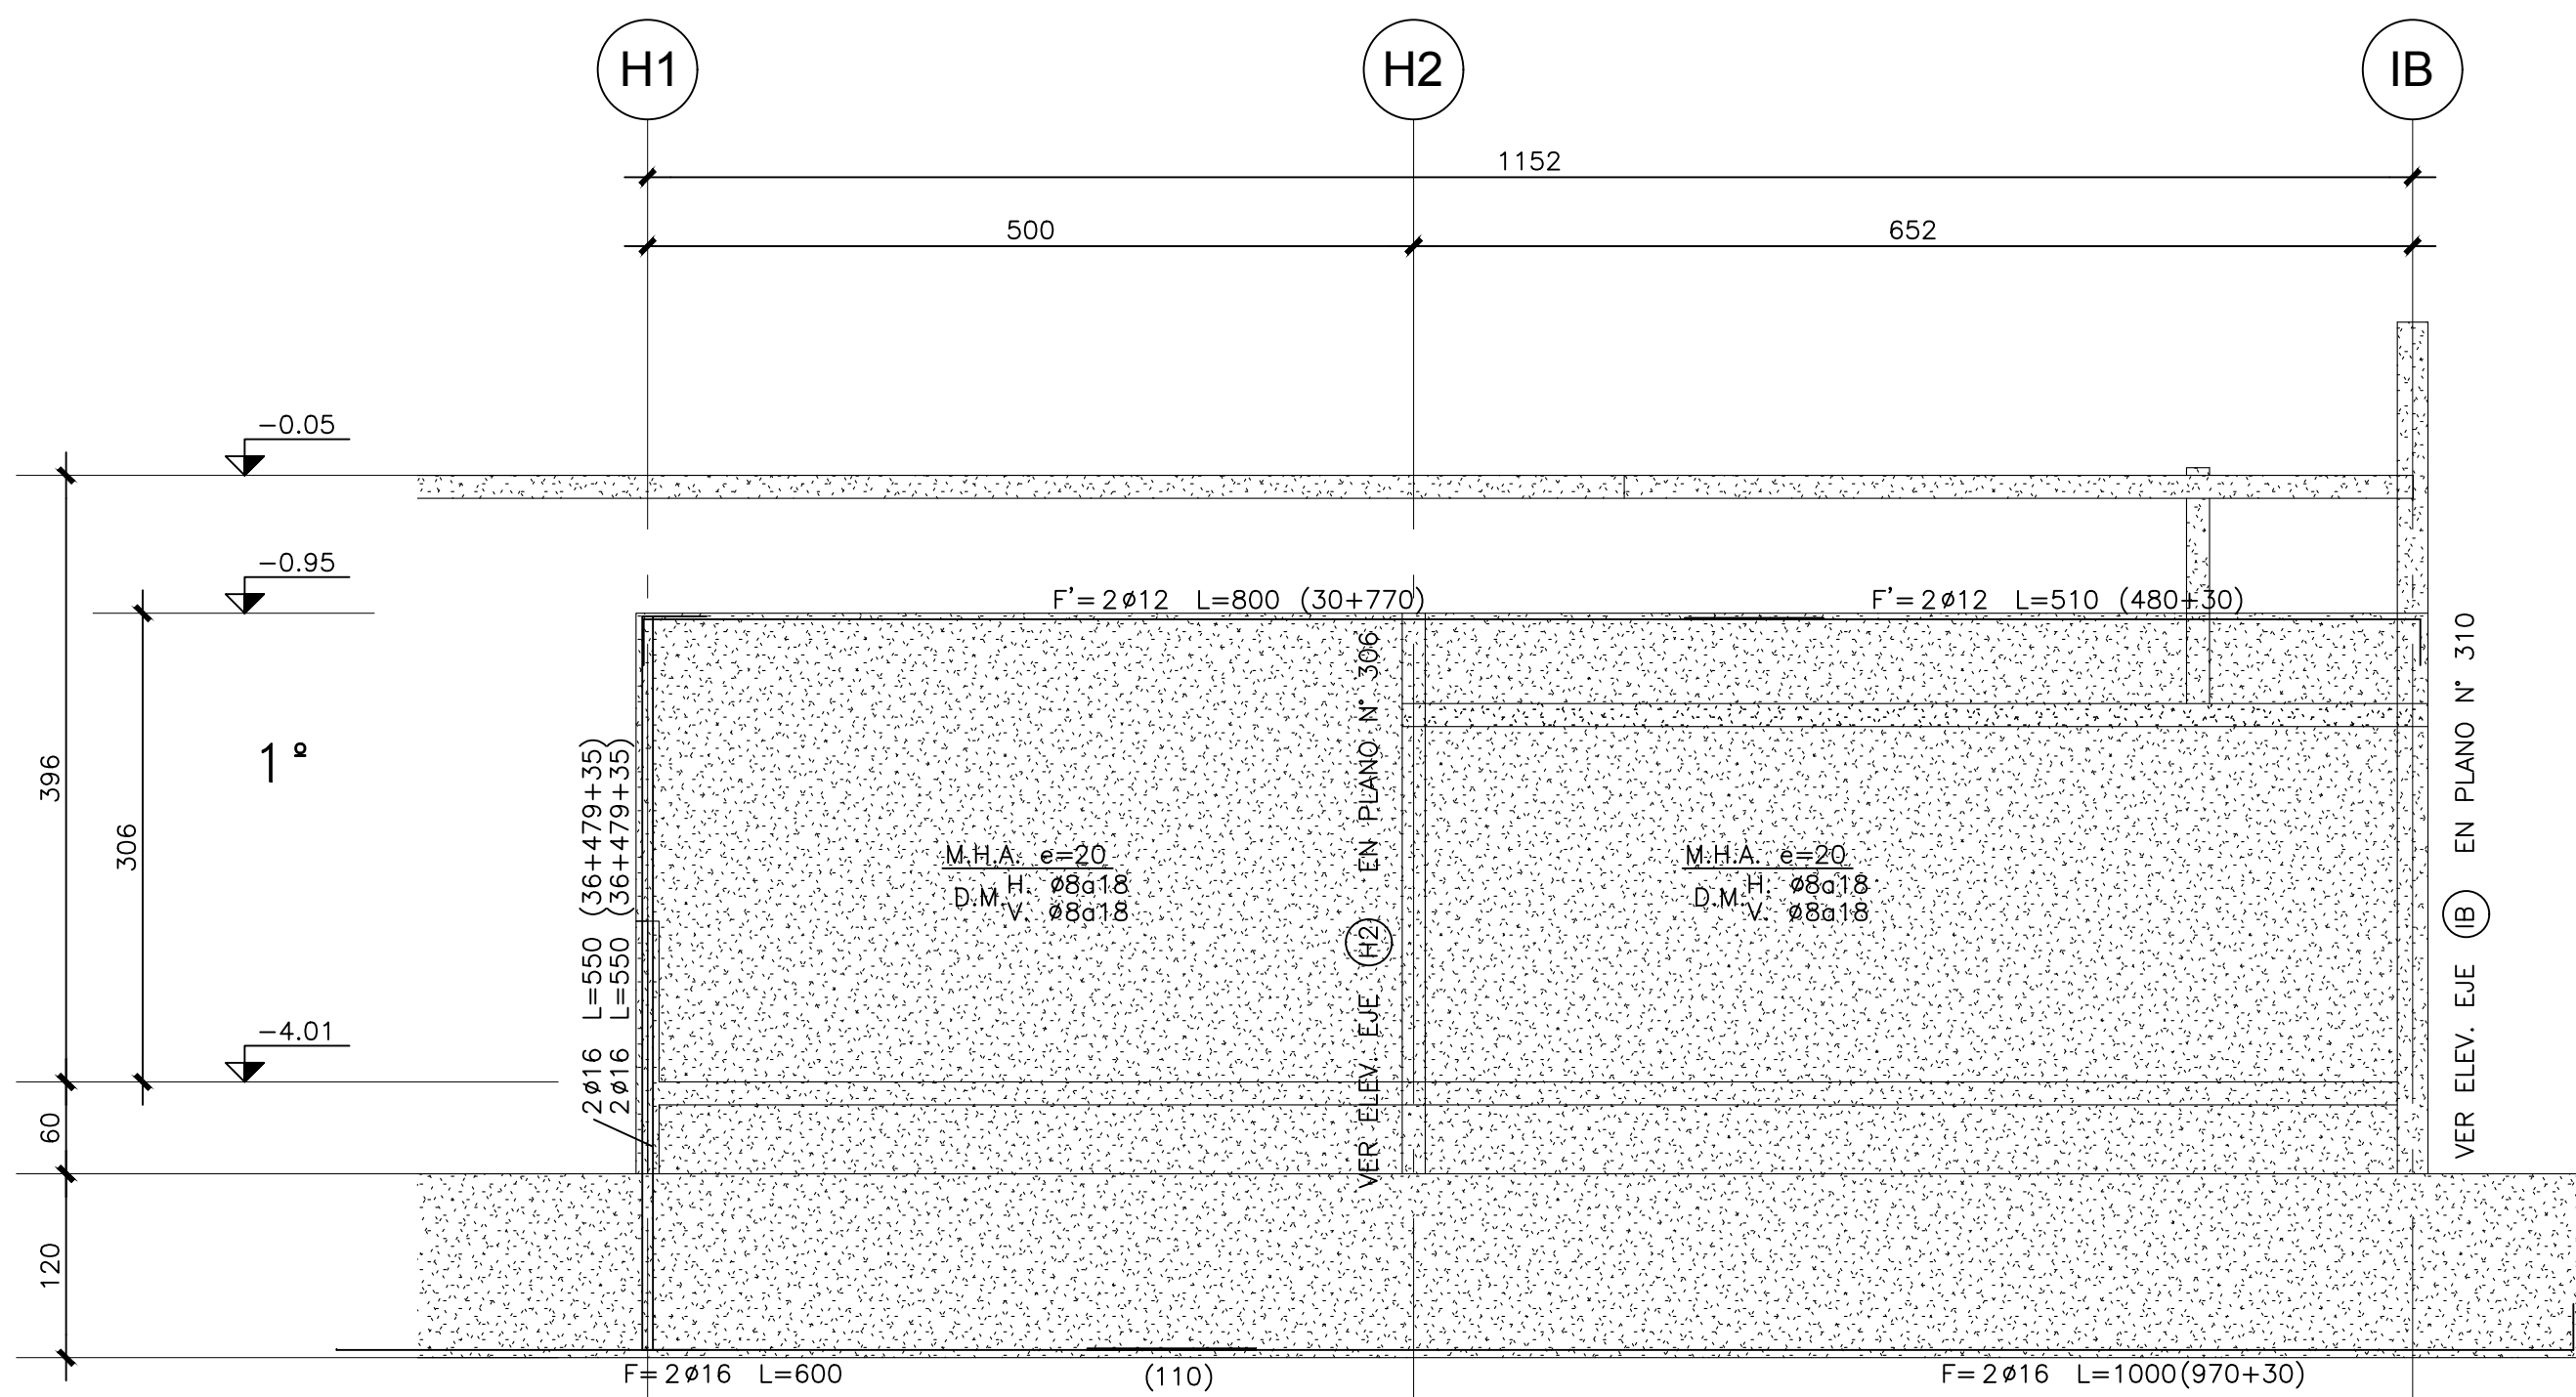


ELEVACION EJE 1AA

ESCALA 1:50

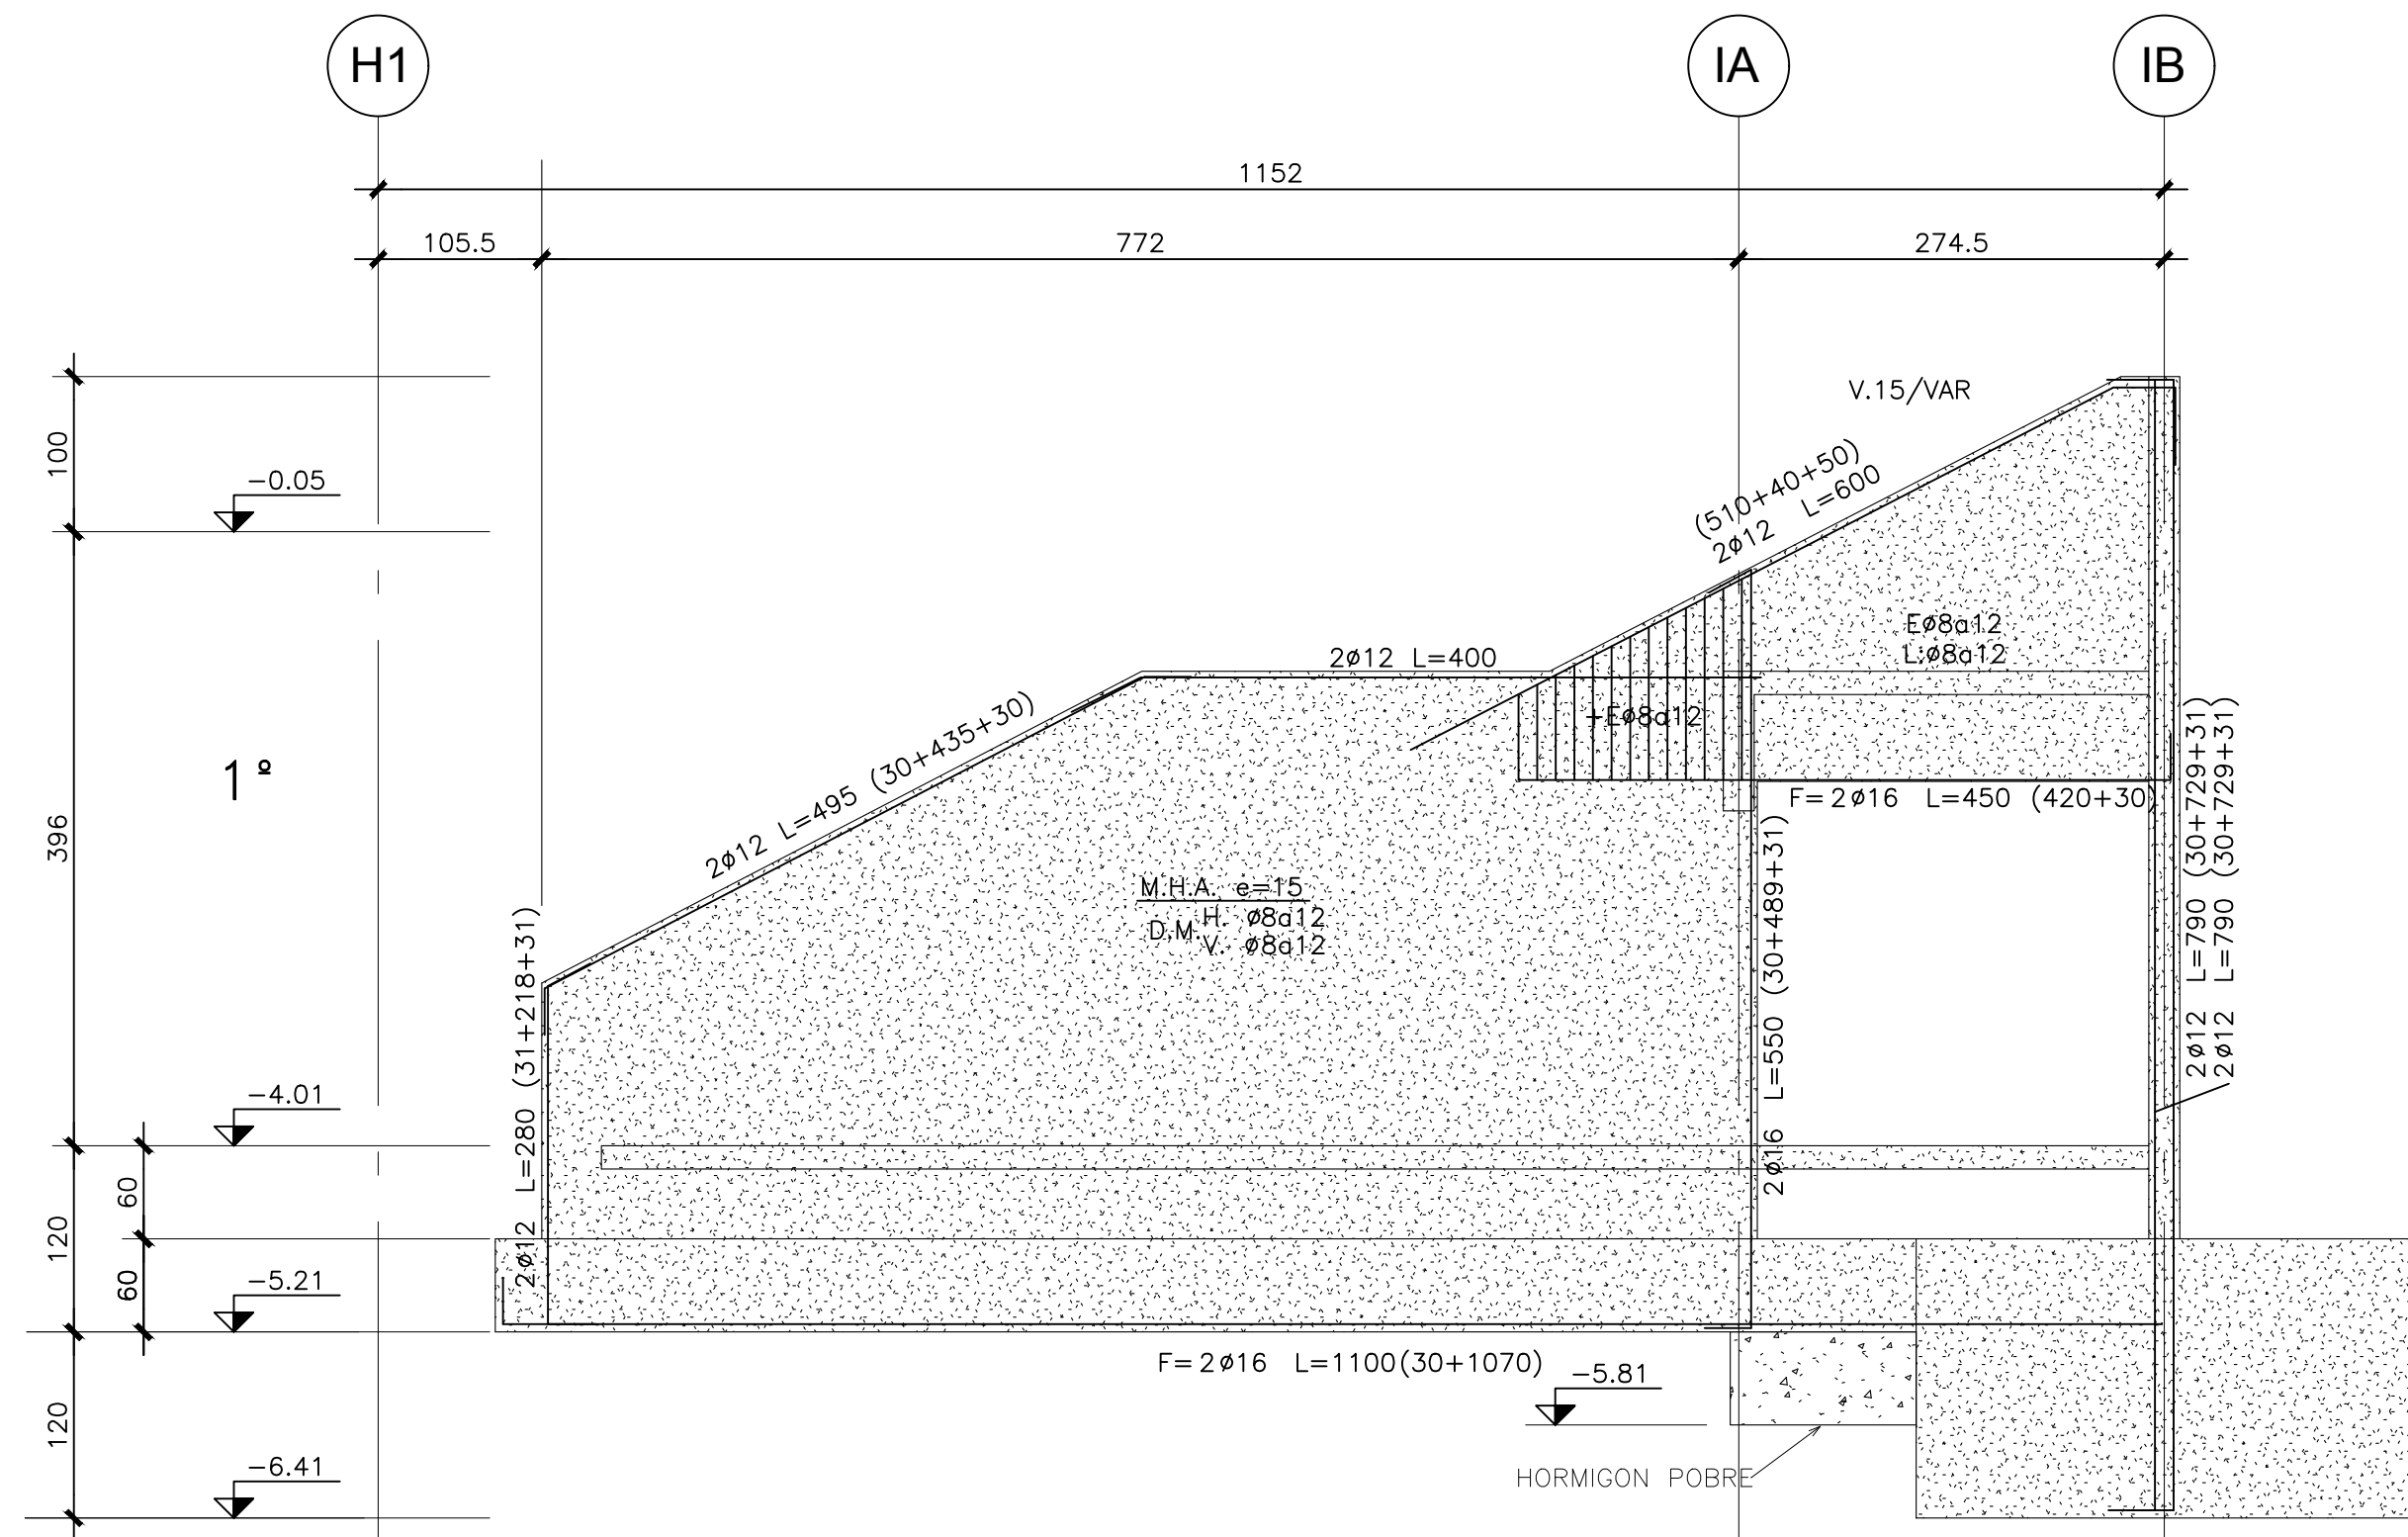

ELEVACION EJE 1BB

ESCALA 1:50

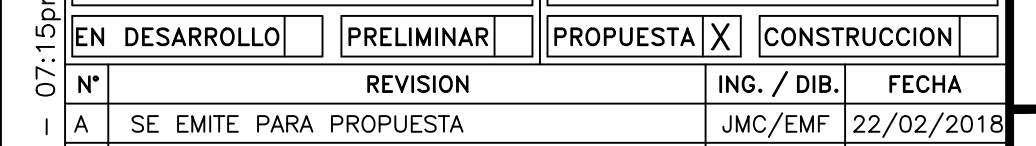ESTADO:		APROBADO PARA:		MAGDALENA 140 Piso 24 OF.2402 LAS CONDES SANTIAGO, CHILE FONO: +56 2 25941300 Info@renelagos.com www.renelagos.com			
EN DESARROLLO	PRELIMINAR	PROPUESTA	CONSTRUCCION				
N°	REVISION	ING. / DIB.		FECHA		PROYECTO	
A	SE EMITE PARA PROPUESTA	JMC/EMF		22/02/2018			
 RENE LAGOS CONTRERAS MARIAINE KUPFER CAJAL GONZALO RIASI SPAINZA LUIS FERRER MACQUEO SIMON SANHUELA TORREALBA						U. DE LOS ANDES CONTENIDO ELEVACION EJE 1", 1A, 1b, C, 1AA, 1BB	
CALCULO	J. MOLINA C.	DIBUJO	E. MORALES F.	ESCALAS	INDICADAS	NUMERO 2017_67-301	
DISEÑO	E. MORALES F.	REVISOR	M. KUPFER C.	FECHA DICIEMBRE 2017			