
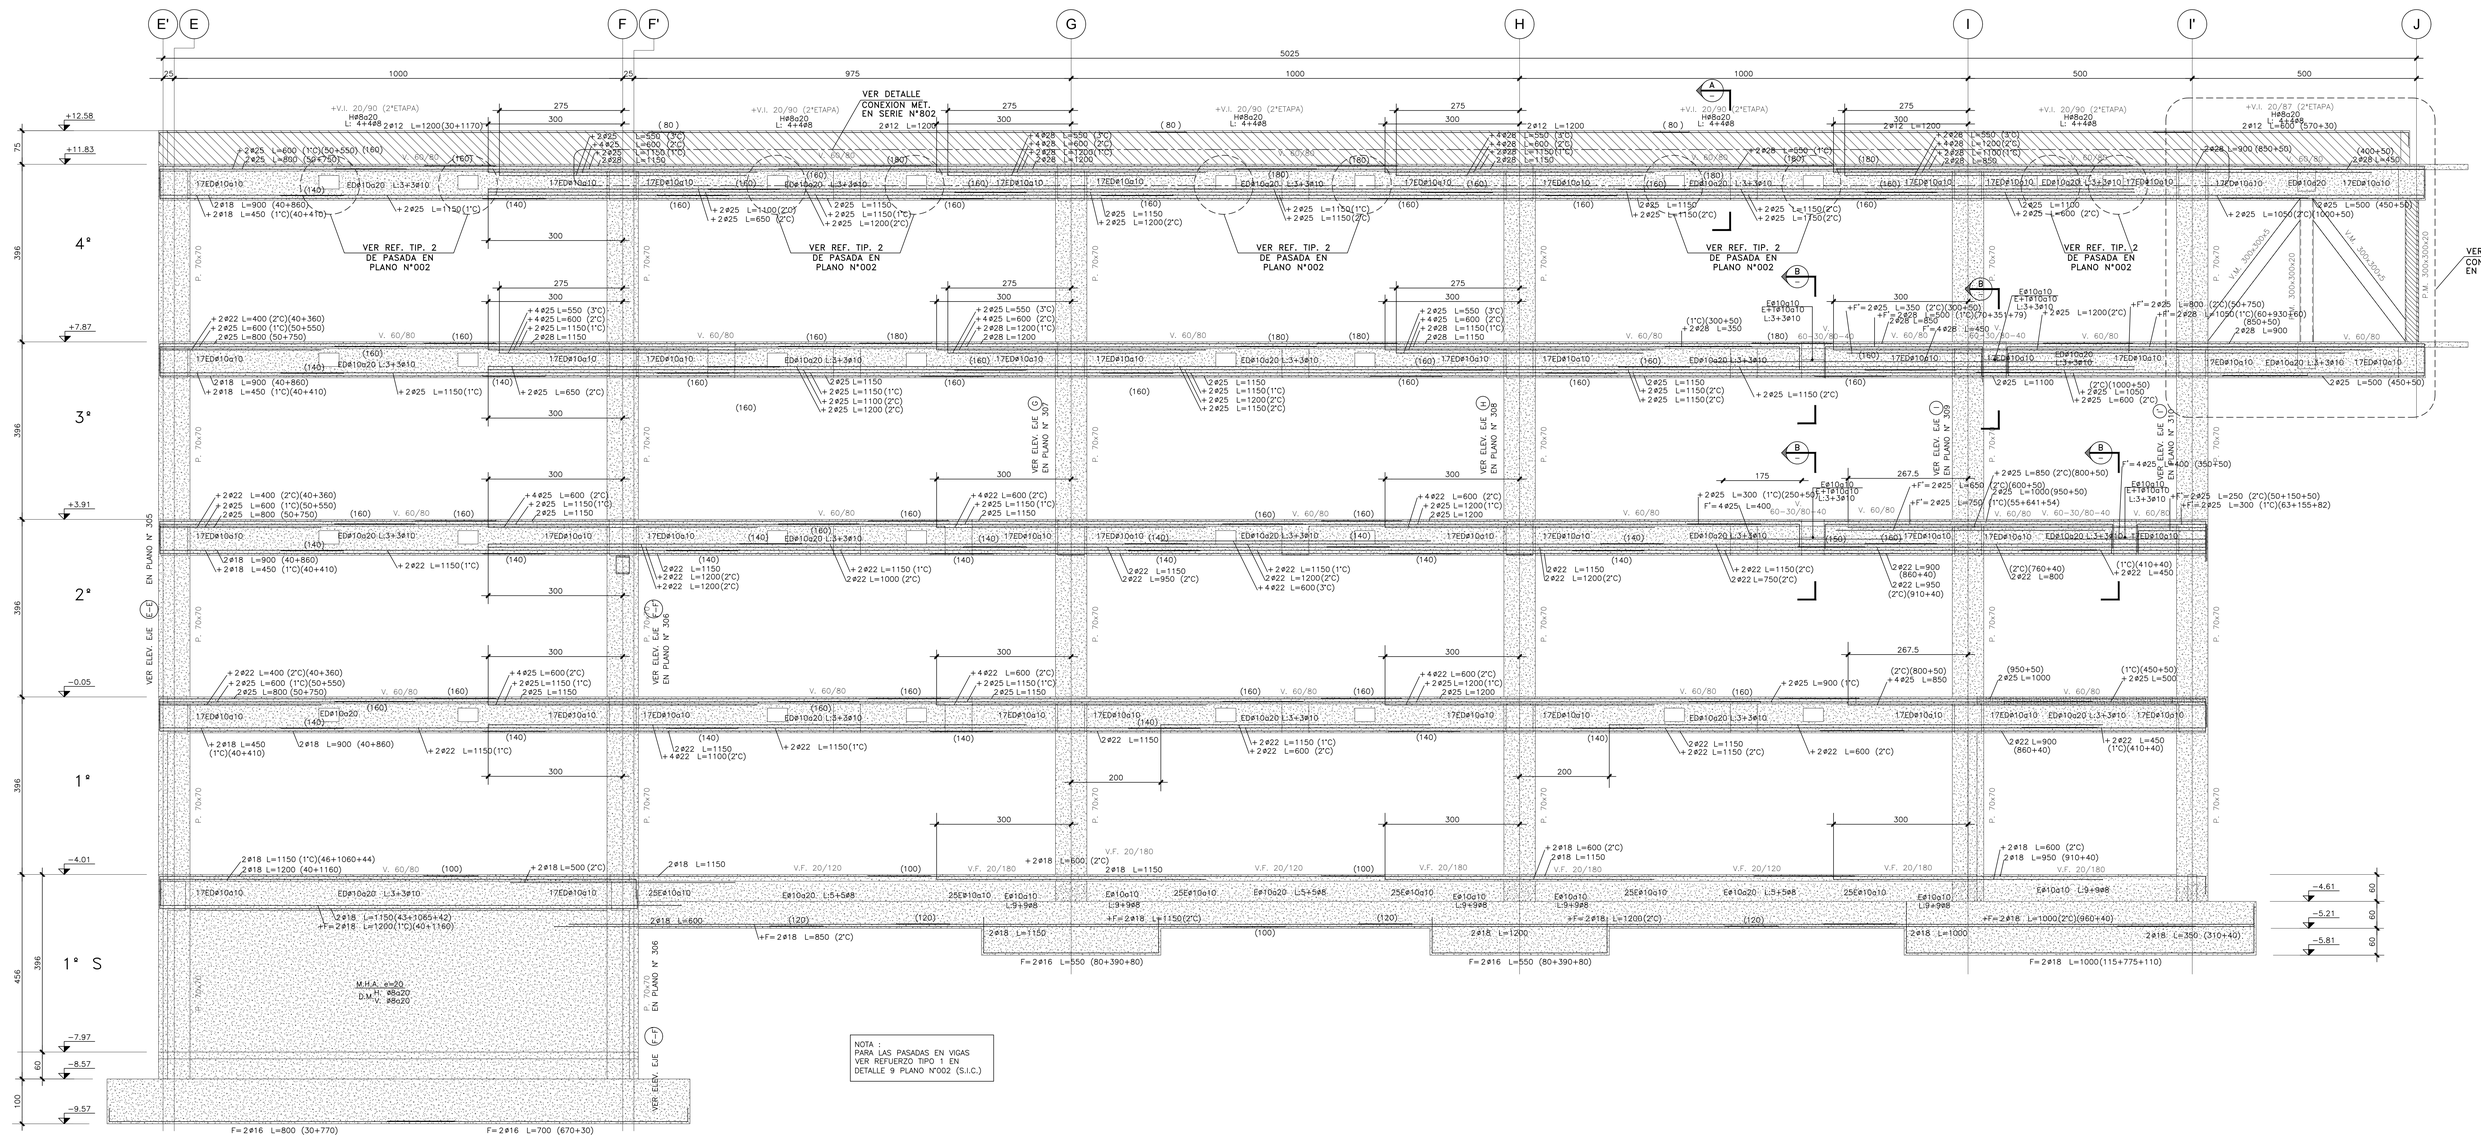


ELEVACION EJE 3−3'

ESCALA 1:50

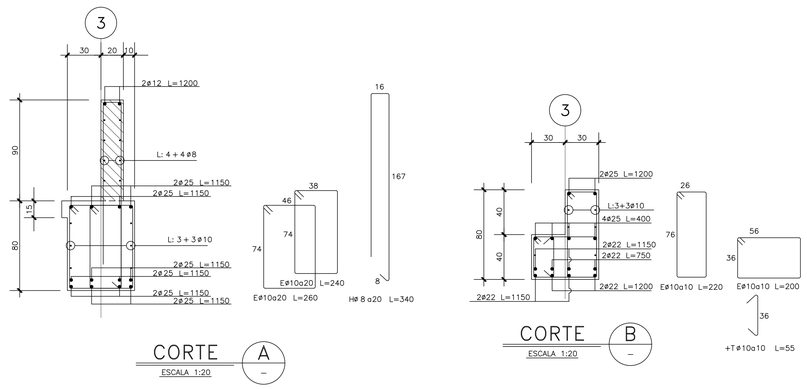

ESTADO:		APROBADO PARA:	
EN DESARROLLO	PRELIMINAR	PROPUESTA X	CONSTRUCCION

N°	REVISION	ING. / DIB.	FECHA
A	SE EMITE PARA PROPUESTA	JMC/EMF	22/02/2018

MAGDALENA 140 Piso 24 OF.2402 LAS CONDES
SANTIAGO, CHILE | FONO: +56 2 25941300
info@renelagos.com | www.renelagos.com
renelagos engineers

RENE LAGOS CONTRERAS
MARIANNE KUPFER CAUTY
GONZALO ARIAS ESPARZA
LUIS DE LA FUENTE MARTINEZ
SIMON SANHUEZA TORREALBA

PROYECTO: U. DE LOS ANDES

CONTENIDO: ELEVACION EJE 3−3'

CALCULO	DIBUJO	ESCALAS	NUMERO	REV.
J. MOLINA C.	E. MORALES F.	INDICADAS	2017_67−303	A
DISEÑO: E. MORALES F.	REVISO: M. KUPFER C.	FECHA: DICIEMBRE 2017		

07:15pm 30/01/2018 2017_67−303.dwg